



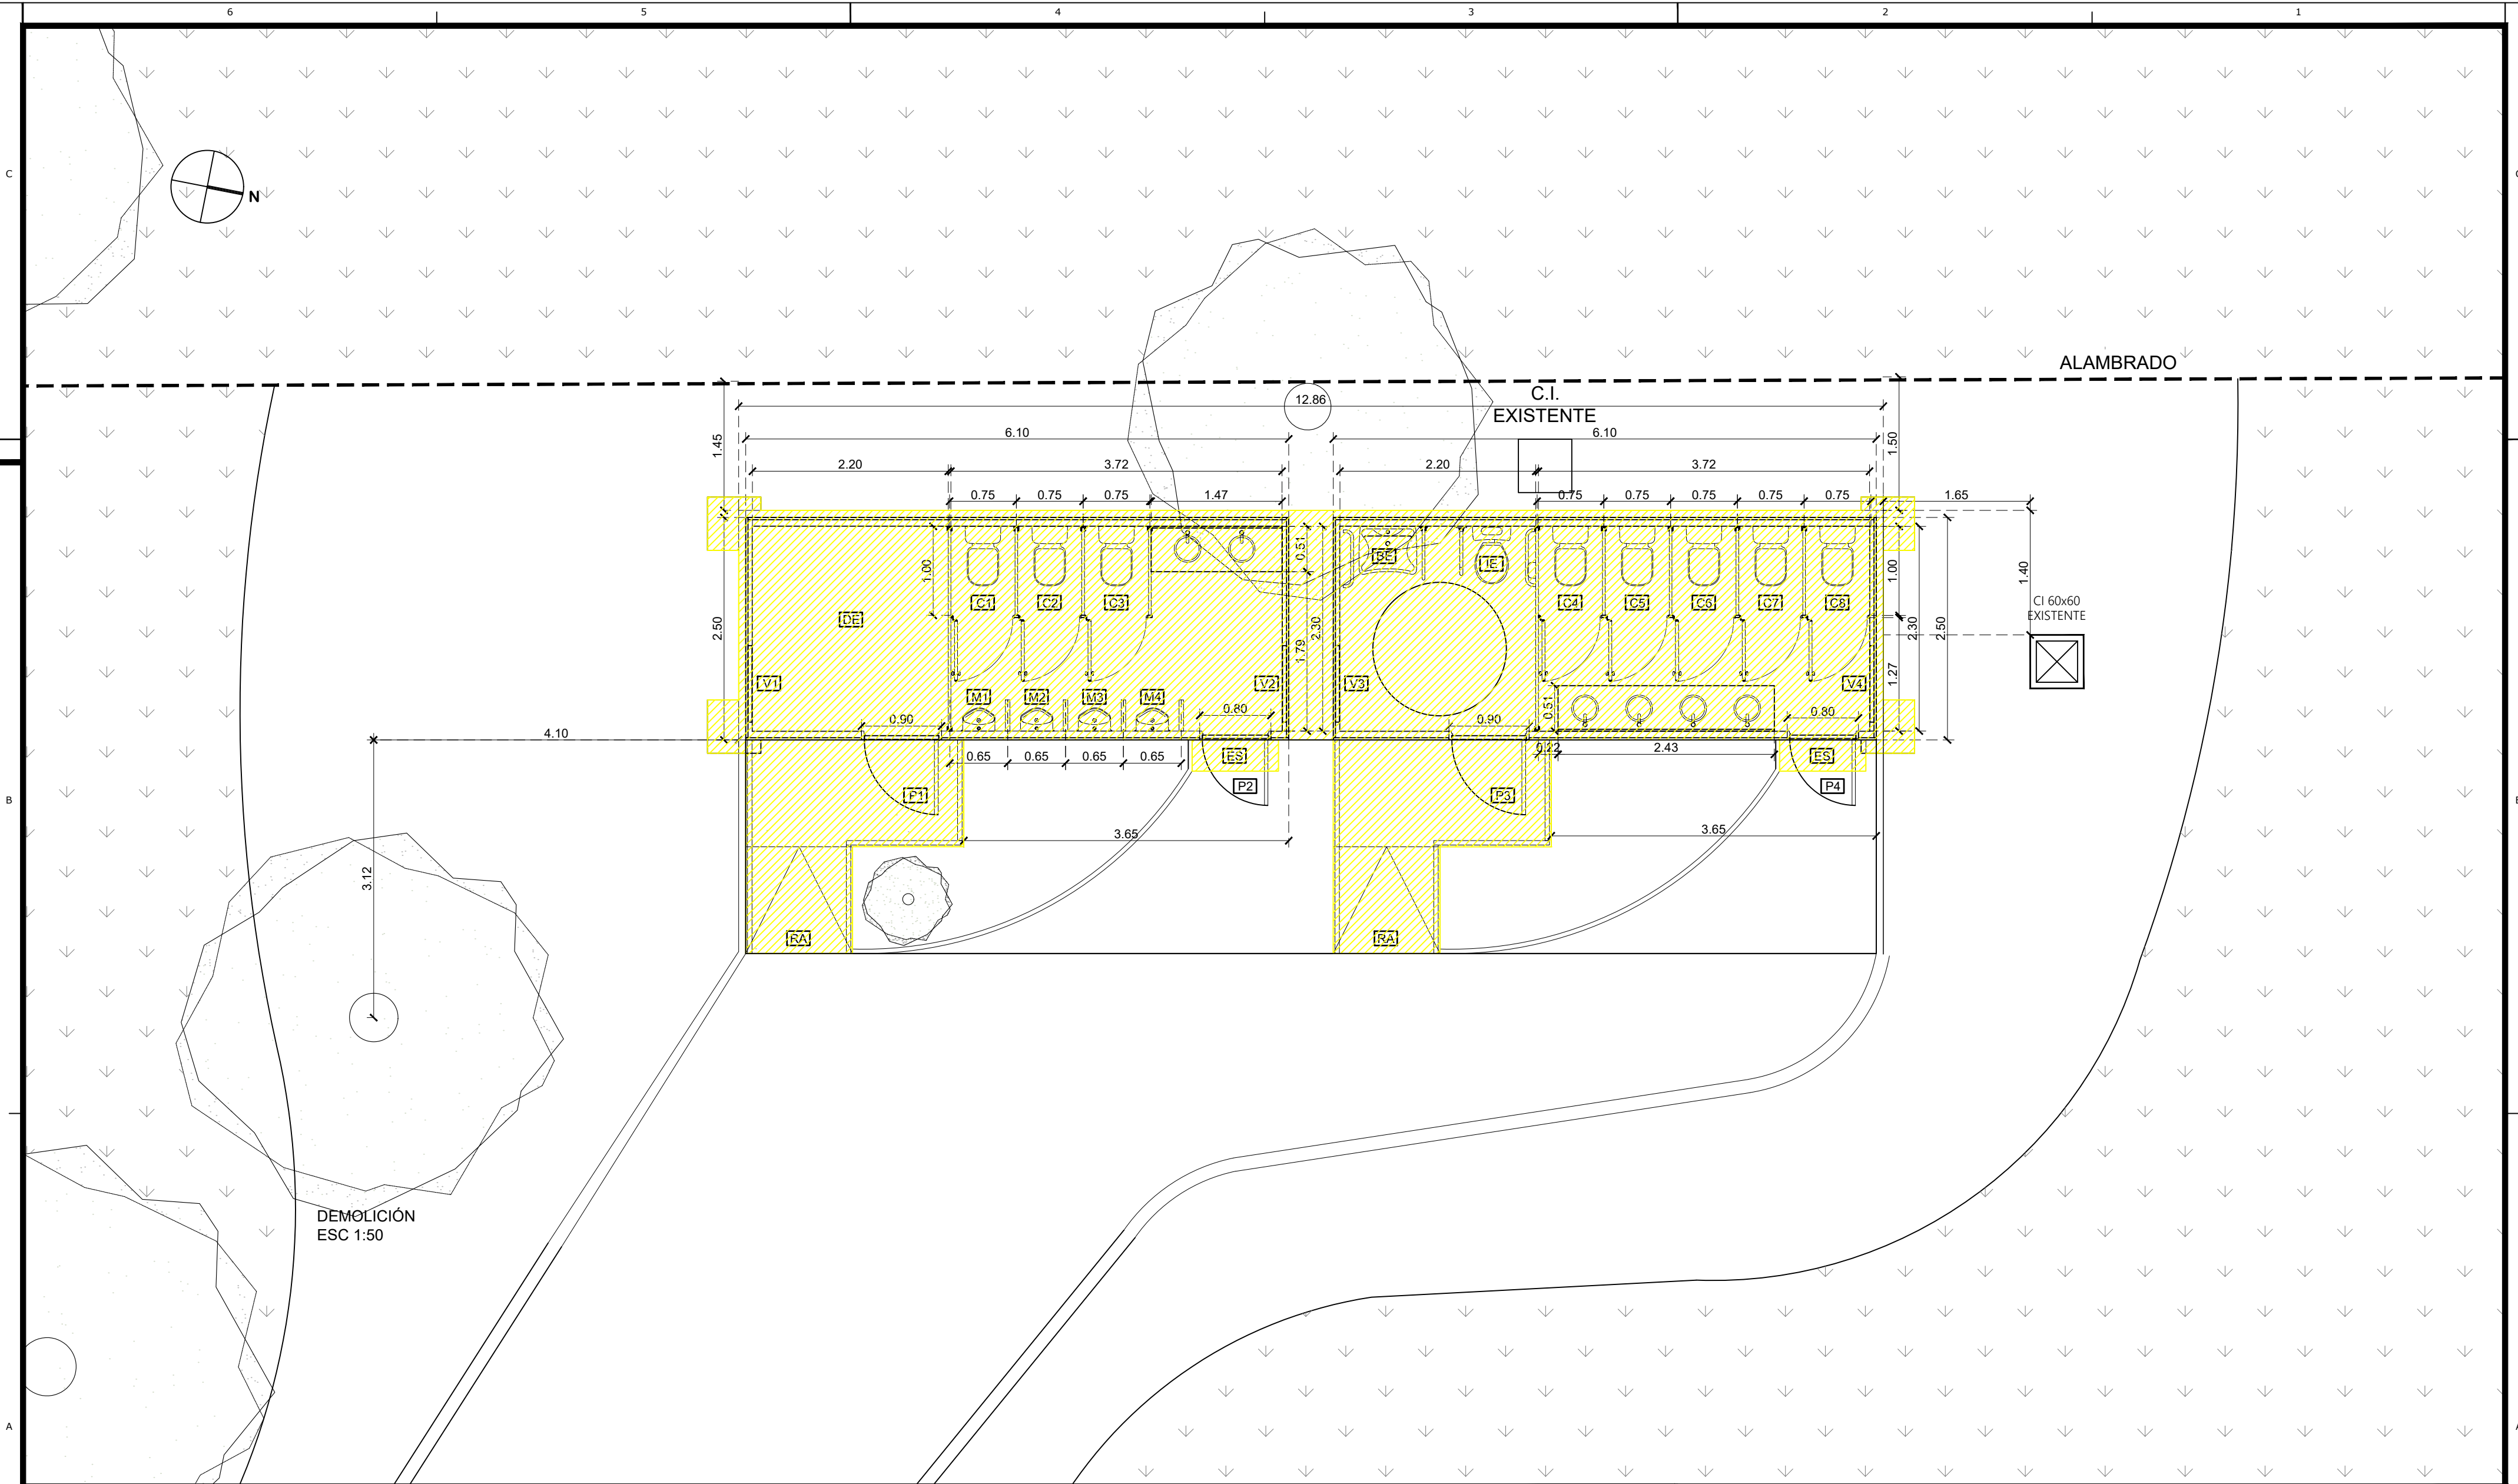

**NOTAS**

- 45 m² de demolición

|   |  |   |  |                                       |  |                                                                                       |  |
|---|--|---|--|---------------------------------------|--|---------------------------------------------------------------------------------------|--|
| NOTAS   |  | LA PRESENTE DOCUMENTACIÓN ES INDICATIVA. EL CONTRATISTA EJECUTARÁ LA DOCUMENTACIÓN CONSTRUCTIVA DE LA OBRA, GENERAL Y DE DETALLE, LA CUAL DEBERÁ SER APROBADA POR LA DIRECCIÓN GENERAL DE ÁREAS DE CONSERVACIÓN Y RESTAURACIÓN AMBIENTAL. TODAS LAS MEDIDAS Y NIVELES SERÁN VERIFICADAS EN OBRA. |  |                                       |  |                                                                                       |  |
| <b>GOBIERNO DE LA CIUDAD DE BUENOS AIRES</b><br>SUBSECRETARIA DE AMBIENTE<br>DIRECCION GENERAL DE AREAS DE CONSERVACION Y RESTAURACION AMBIENTAL |  |   |  | GERENCIA OPERATIVA DE INFRAESTRUCTURA |  |  |  |
| OBRA   |  | RESERVA ECOLÓGICA COSTANERA SUR   |  | DIBUJO                                |  |                                                                                       |  |
| PLANO   |  | DEMOLICIÓN   |  | REVISO                                |  |                                                                                       |  |
| ARCHIVO   |  | RECS - BAÑOS VIAMONTE   |  | EXPT. N°                              |  | 1F-2025-21464165-GCABA-DGACRA                                                         |  |
| ESCALA   |  |   |  | FECHA                                 |  | ENERO 2025                                                                            |  |
|   |  |   |  | N° PLANO                              |  | RECS_BV_DEM_0.1                                                                       |  |

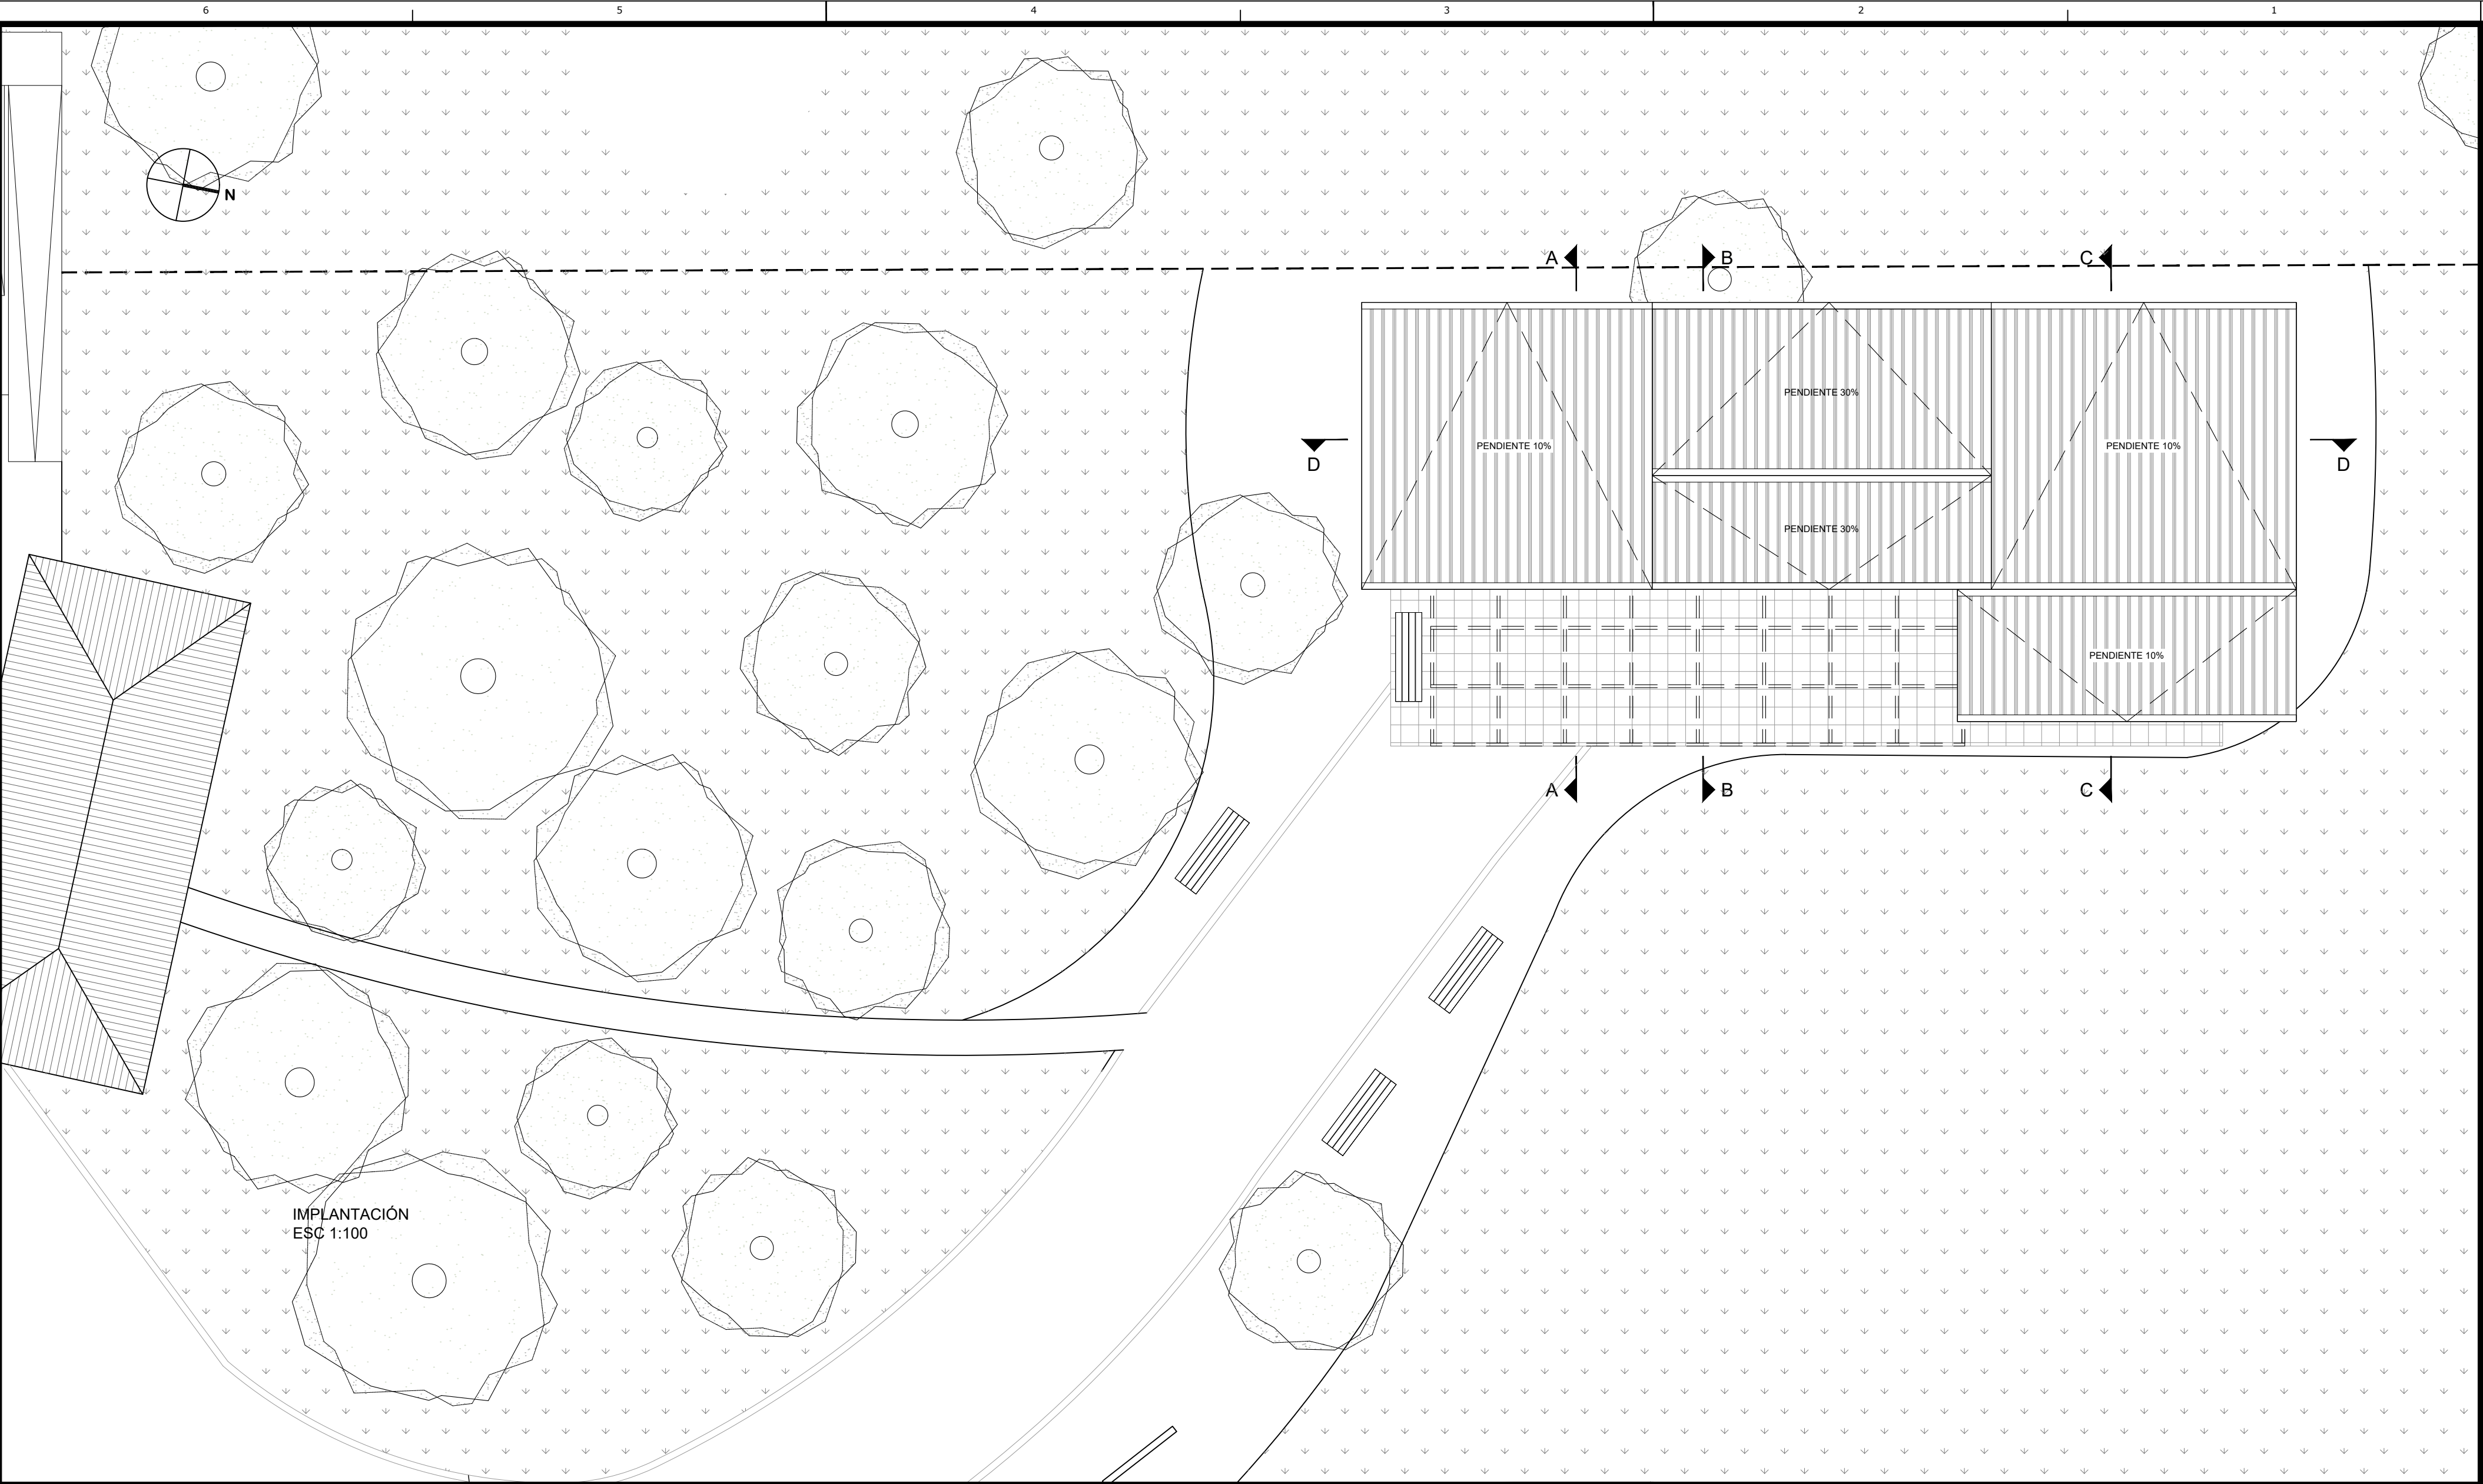


NOTAS

NOTAS

LA PRESENTE DOCUMENTACIÓN ES INDICATIVA. EL CONTRATISTA EJECUTARÁ LA DOCUMENTACIÓN CONSTRUCTIVA DE LA OBRA, GENERAL Y DE DETALLE, LA CUAL DEBERÁ SER APROBADA POR LA DIRECCIÓN GENERAL DE ÁREAS DE CONSERVACIÓN Y RESTAURACIÓN AMBIENTAL. TODAS LAS MEDIDAS Y NIVELES SERÁN VERIFICADAS EN OBRA.

|   |                       |                                 |            |                                       |  |
|---|-----------------------|---------------------------------|------------|---------------------------------------|--|
| <b>GOBIERNO DE LA CIUDAD DE BUENOS AIRES</b><br>SUBSECRETARIA DE AMBIENTE<br>DIRECCION GENERAL DE AREAS DE CONSERVACION Y RESTAURACION AMBIENTAL |                       |                                 |            | GERENCIA OPERATIVA DE INFRAESTRUCTURA |  |
| OBRA   |                       | RESERVA ECOLÓGICA COSTANERA SUR |            | DIBUJO                                |  |
| PLANO   |                       | IMPLANTACIÓN                    |            | REVISO                                |  |
| ARCHIVO   | RECS - BAÑOS VIAMONTE | EXpte. Nº                       |            | APROBO                                |  |
| ESCALA   |                       | FECHA                           | ENERO 2025 | Nº PLANO                              |  |

IF-2025-21464165-GCABA-DGACRA  
**RECS\_BV\_IMP\_1.0**

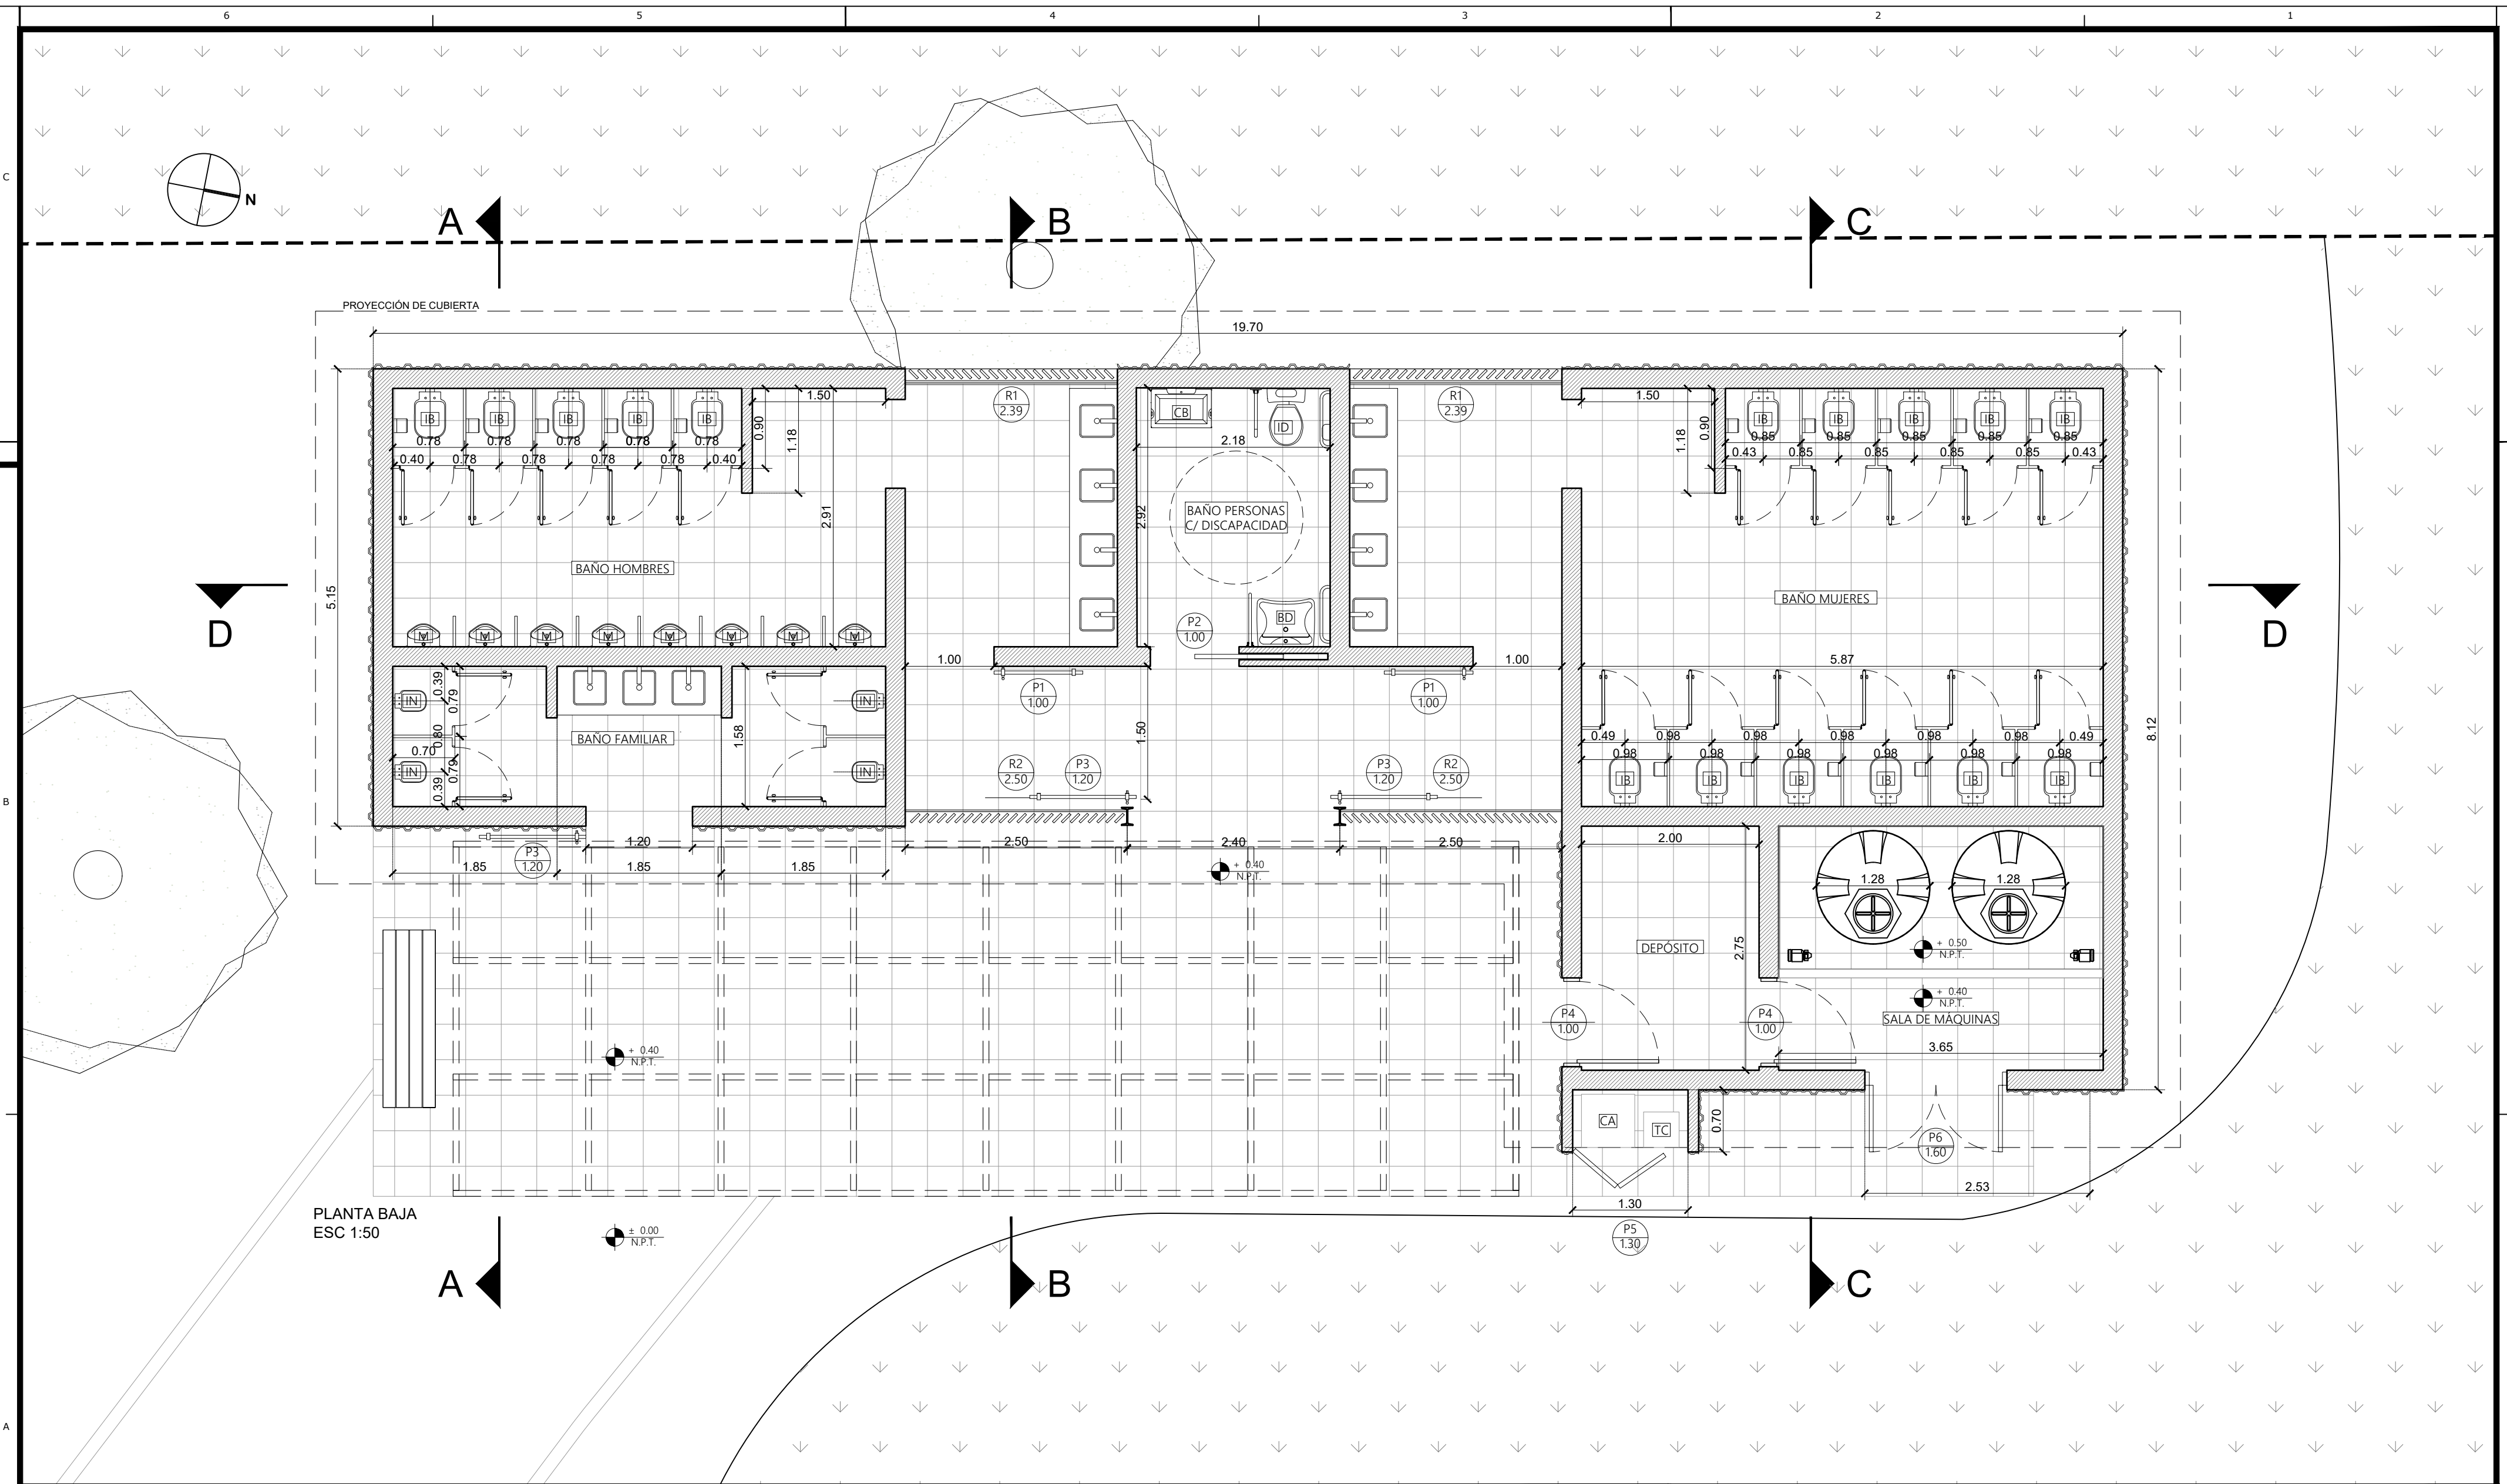

NOTAS

BAÑOS EXISTENTES

BAÑOS MUJERES

- 4 BACHAS

- 4 INODOROS

BAÑOS HOMBRES

- 2 BACHAS

- 3 INODOROS

- 4 MINGITORIOS

BAÑO DISCAPACITADOS

- 1 BACHA

- 1 INODORO

BAÑOS NUEVOS

BAÑOS MUJERES

- 3 BACHAS

- 9 INODOROS (2 NIÑAS)

BAÑOS HOMBRES

- 3 BACHAS

- 5 INODOROS (1 NIÑOS)

- 7 MINGITORIOS (2 NIÑOS)

BAÑO DISCAPACITADOS

- 1 BACHA

- 1 INODORO

- 4 DUCHAS

REFERENCIAS

CA CALENTADOR DE AGUA

TC TÓTEM CARGA CELULARES

IN INODORO P/ NIÑOS

IB INODORO CORTO TIPO BARI

ID INODORO PERSONAS C/ DISCAPACIDAD

CB CAMBIADOR DE BEBÉS

BD BACHA PERSONAS C/ DISCAPACIDAD

BA BACHA TIPO SQUARE

M MINGITORIO MURAL

NOTAS

GOBIERNO DE LA CIUDAD DE BUENOS AIRES

SUBSECRETARIA DE AMBIENTE

DIRECCION GENERAL DE AREAS DE CONSERVACION Y RESTAURACION AMBIENTAL

OBRA

RESERVA ECOLÓGICA COSTANERA SUR

PLANO

PLANTA BAJA

ARCHIVO

RECS - BAÑOS VIAMONTE

EXPTE. Nº

1F-2025-21464165-GCABA-DGACRA

ESCALA

FECHA

ENERO 2025

Nº PLANO

165-GCABA-DGACRA

GERENCIA OPERATIVA DE INFRAESTRUCTURA


DIBUJO

REVISO

APROBO


RECS\_BV\_PB\_1.1

Página 3 de 27

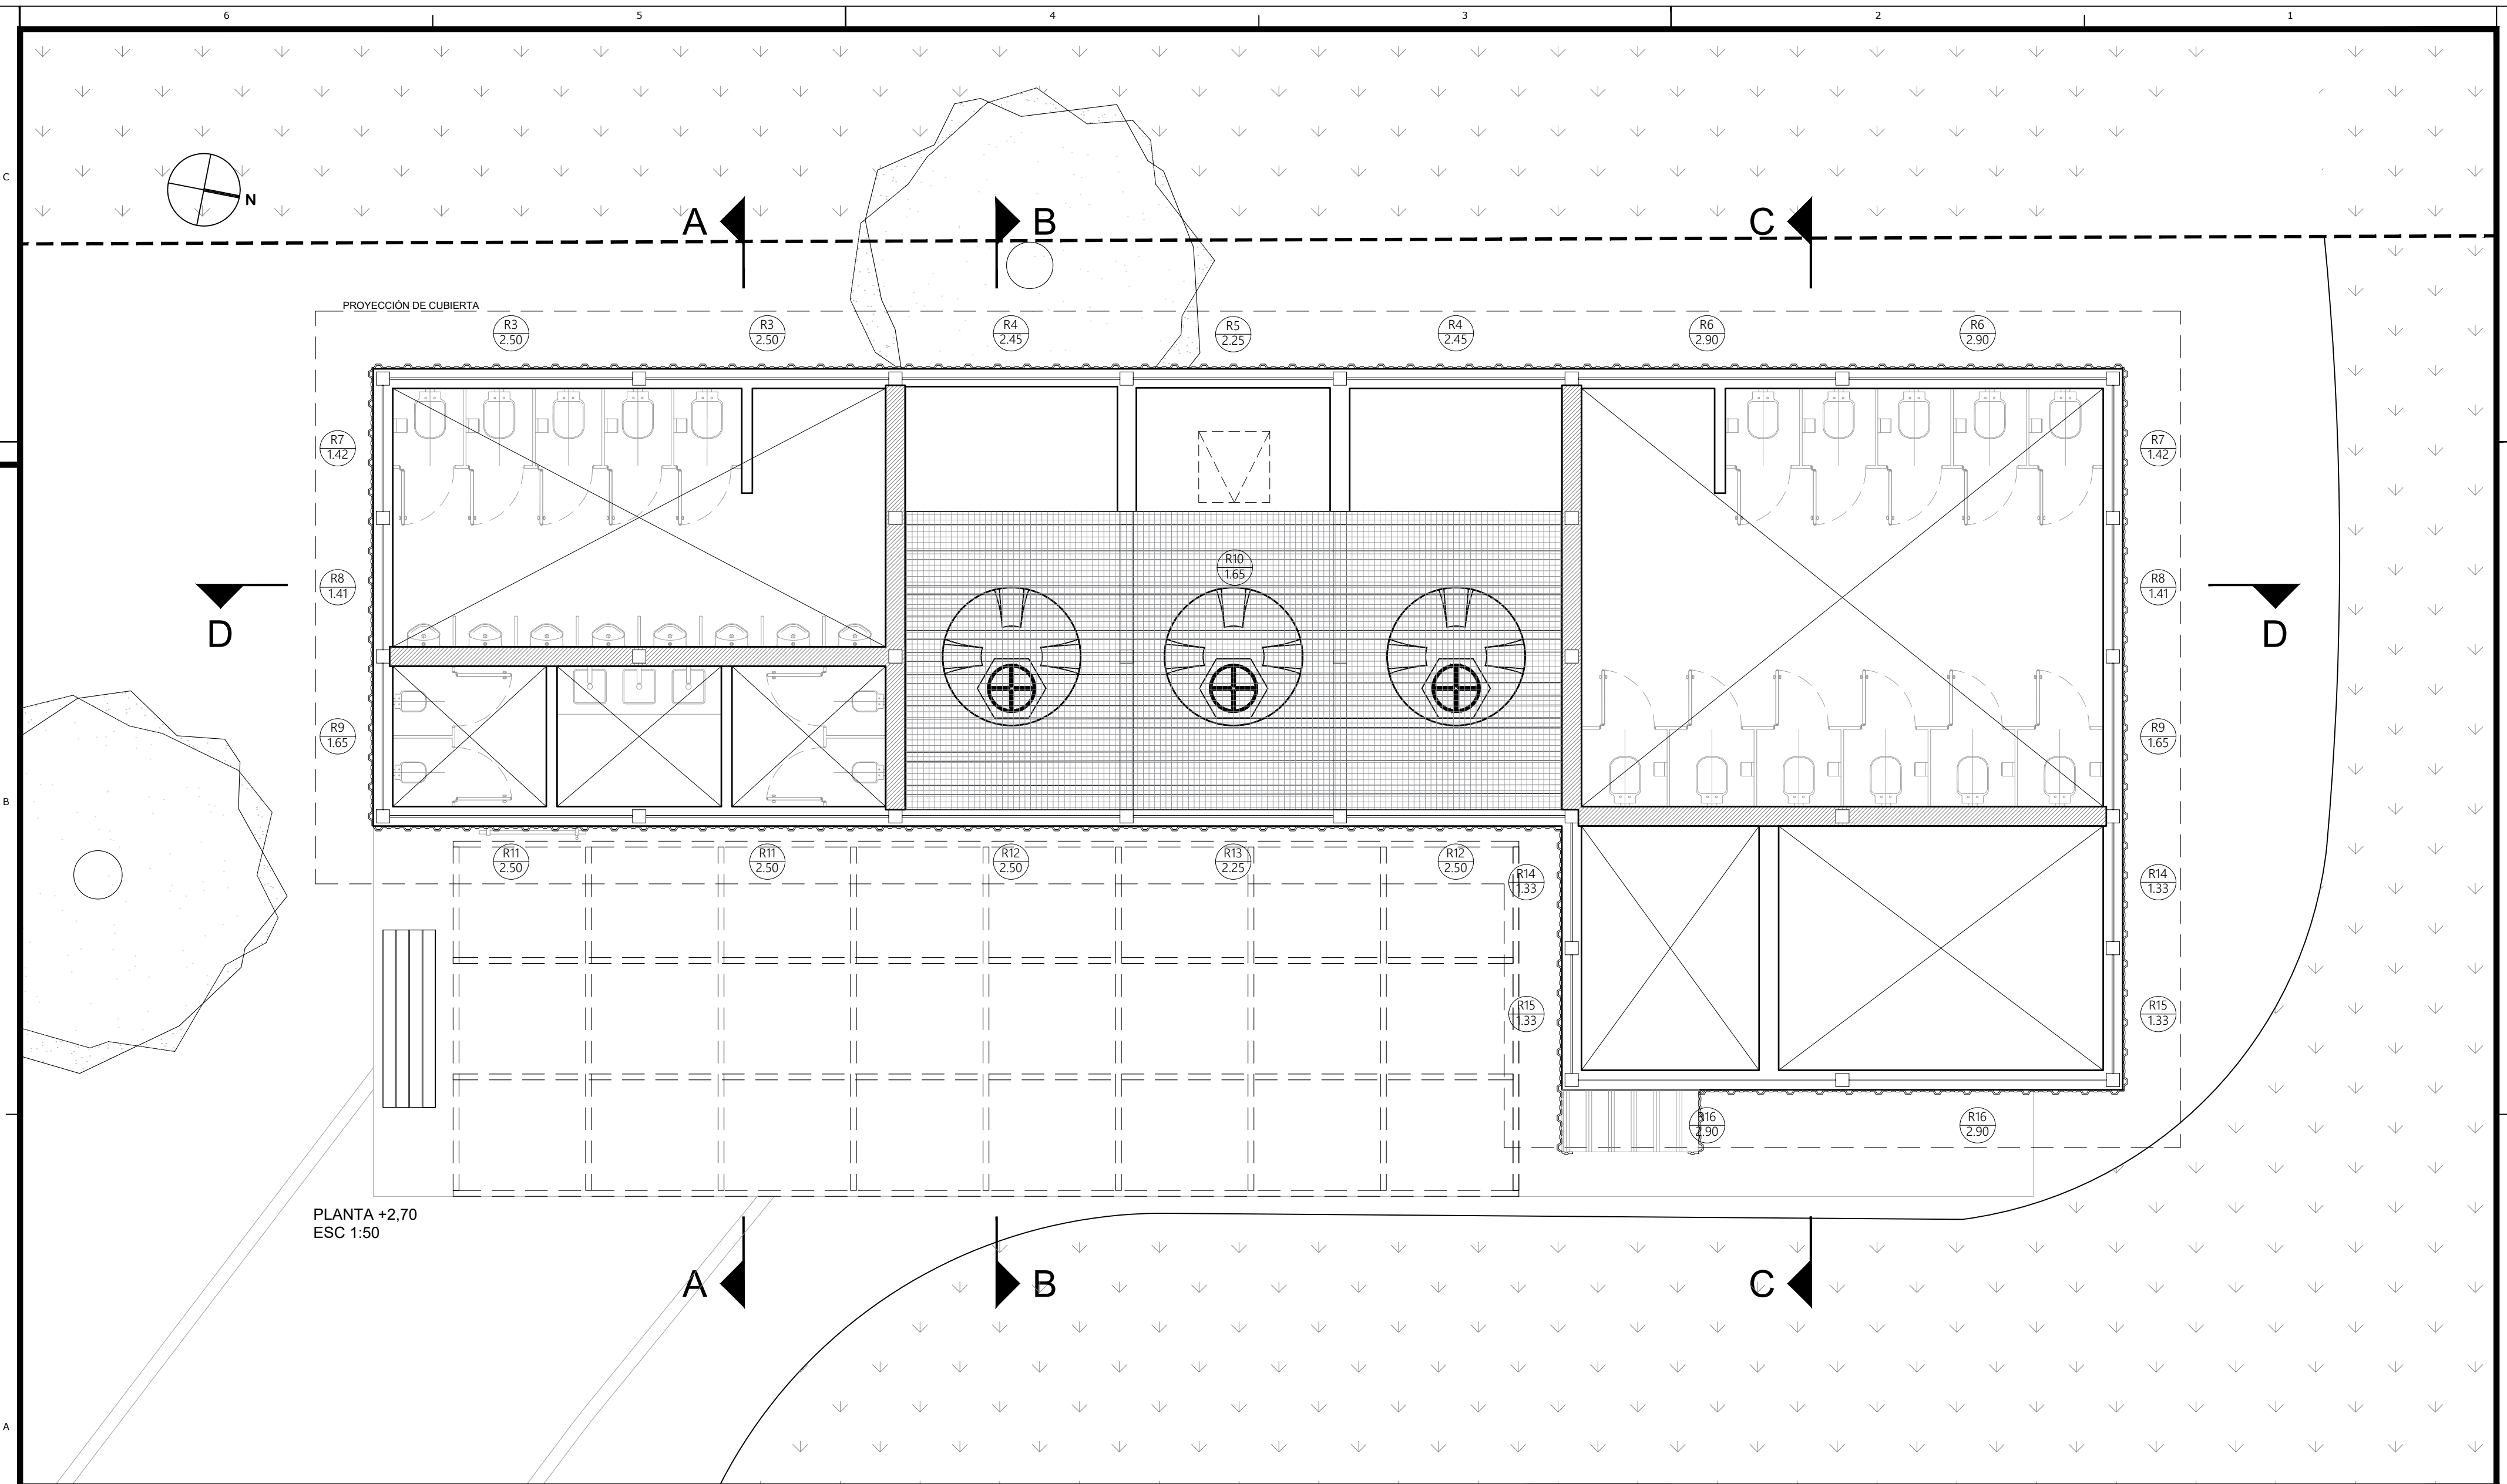

NOTAS


|   |  |                                 |            |   |  |                               |  |
|---|--|---------------------------------|------------|---|--|-------------------------------|--|
| NOTAS   |  |                                 |            | LA PRESENTE DOCUMENTACIÓN ES INDICATIVA. EL CONTRATISTA EJECUTARÁ LA DOCUMENTACIÓN CONSTRUCTIVA DE LA OBRA, GENERAL Y DE DETALLE, LA CUAL DEBERÁ SER APROBADA POR LA DIRECCIÓN GENERAL DE ÁREAS DE CONSERVACIÓN Y RESTAURACIÓN AMBIENTAL. TODAS LAS MEDIDAS Y NIVELES SERÁN VERIFICADAS EN OBRA. |  |                               |  |
| GOBIERNO DE LA CIUDAD DE BUENOS AIRES<br>SUBSECRETARIA DE AMBIENTE<br>DIRECCION GENERAL DE AREAS DE CONSERVACION Y RESTAURACION AMBIENTAL |  |                                 |            | GERENCIA OPERATIVA DE INFRAESTRUCTURA   |  |                               |  |
| OBRA   |  | RESERVA ECOLÓGICA COSTANERA SUR |            | DIBUJO   |  |                               |  |
| PLANO   |  | PLANTA +2,70                    |            | REVISO   |  |                               |  |
| ARCHIVO   |  | RECS - BAÑOS VIAMONTE           | EXpte. Nº  | APROBO   |  | IF-2025-21464165-GCABA-DGACRA |  |
| ESCALA   |  |                                 | FECHA      | Nº PLANO   |  | RECS_BV_PA_1.2                |  |
|   |  |                                 | ENERO 2025 |   |  |                               |  |

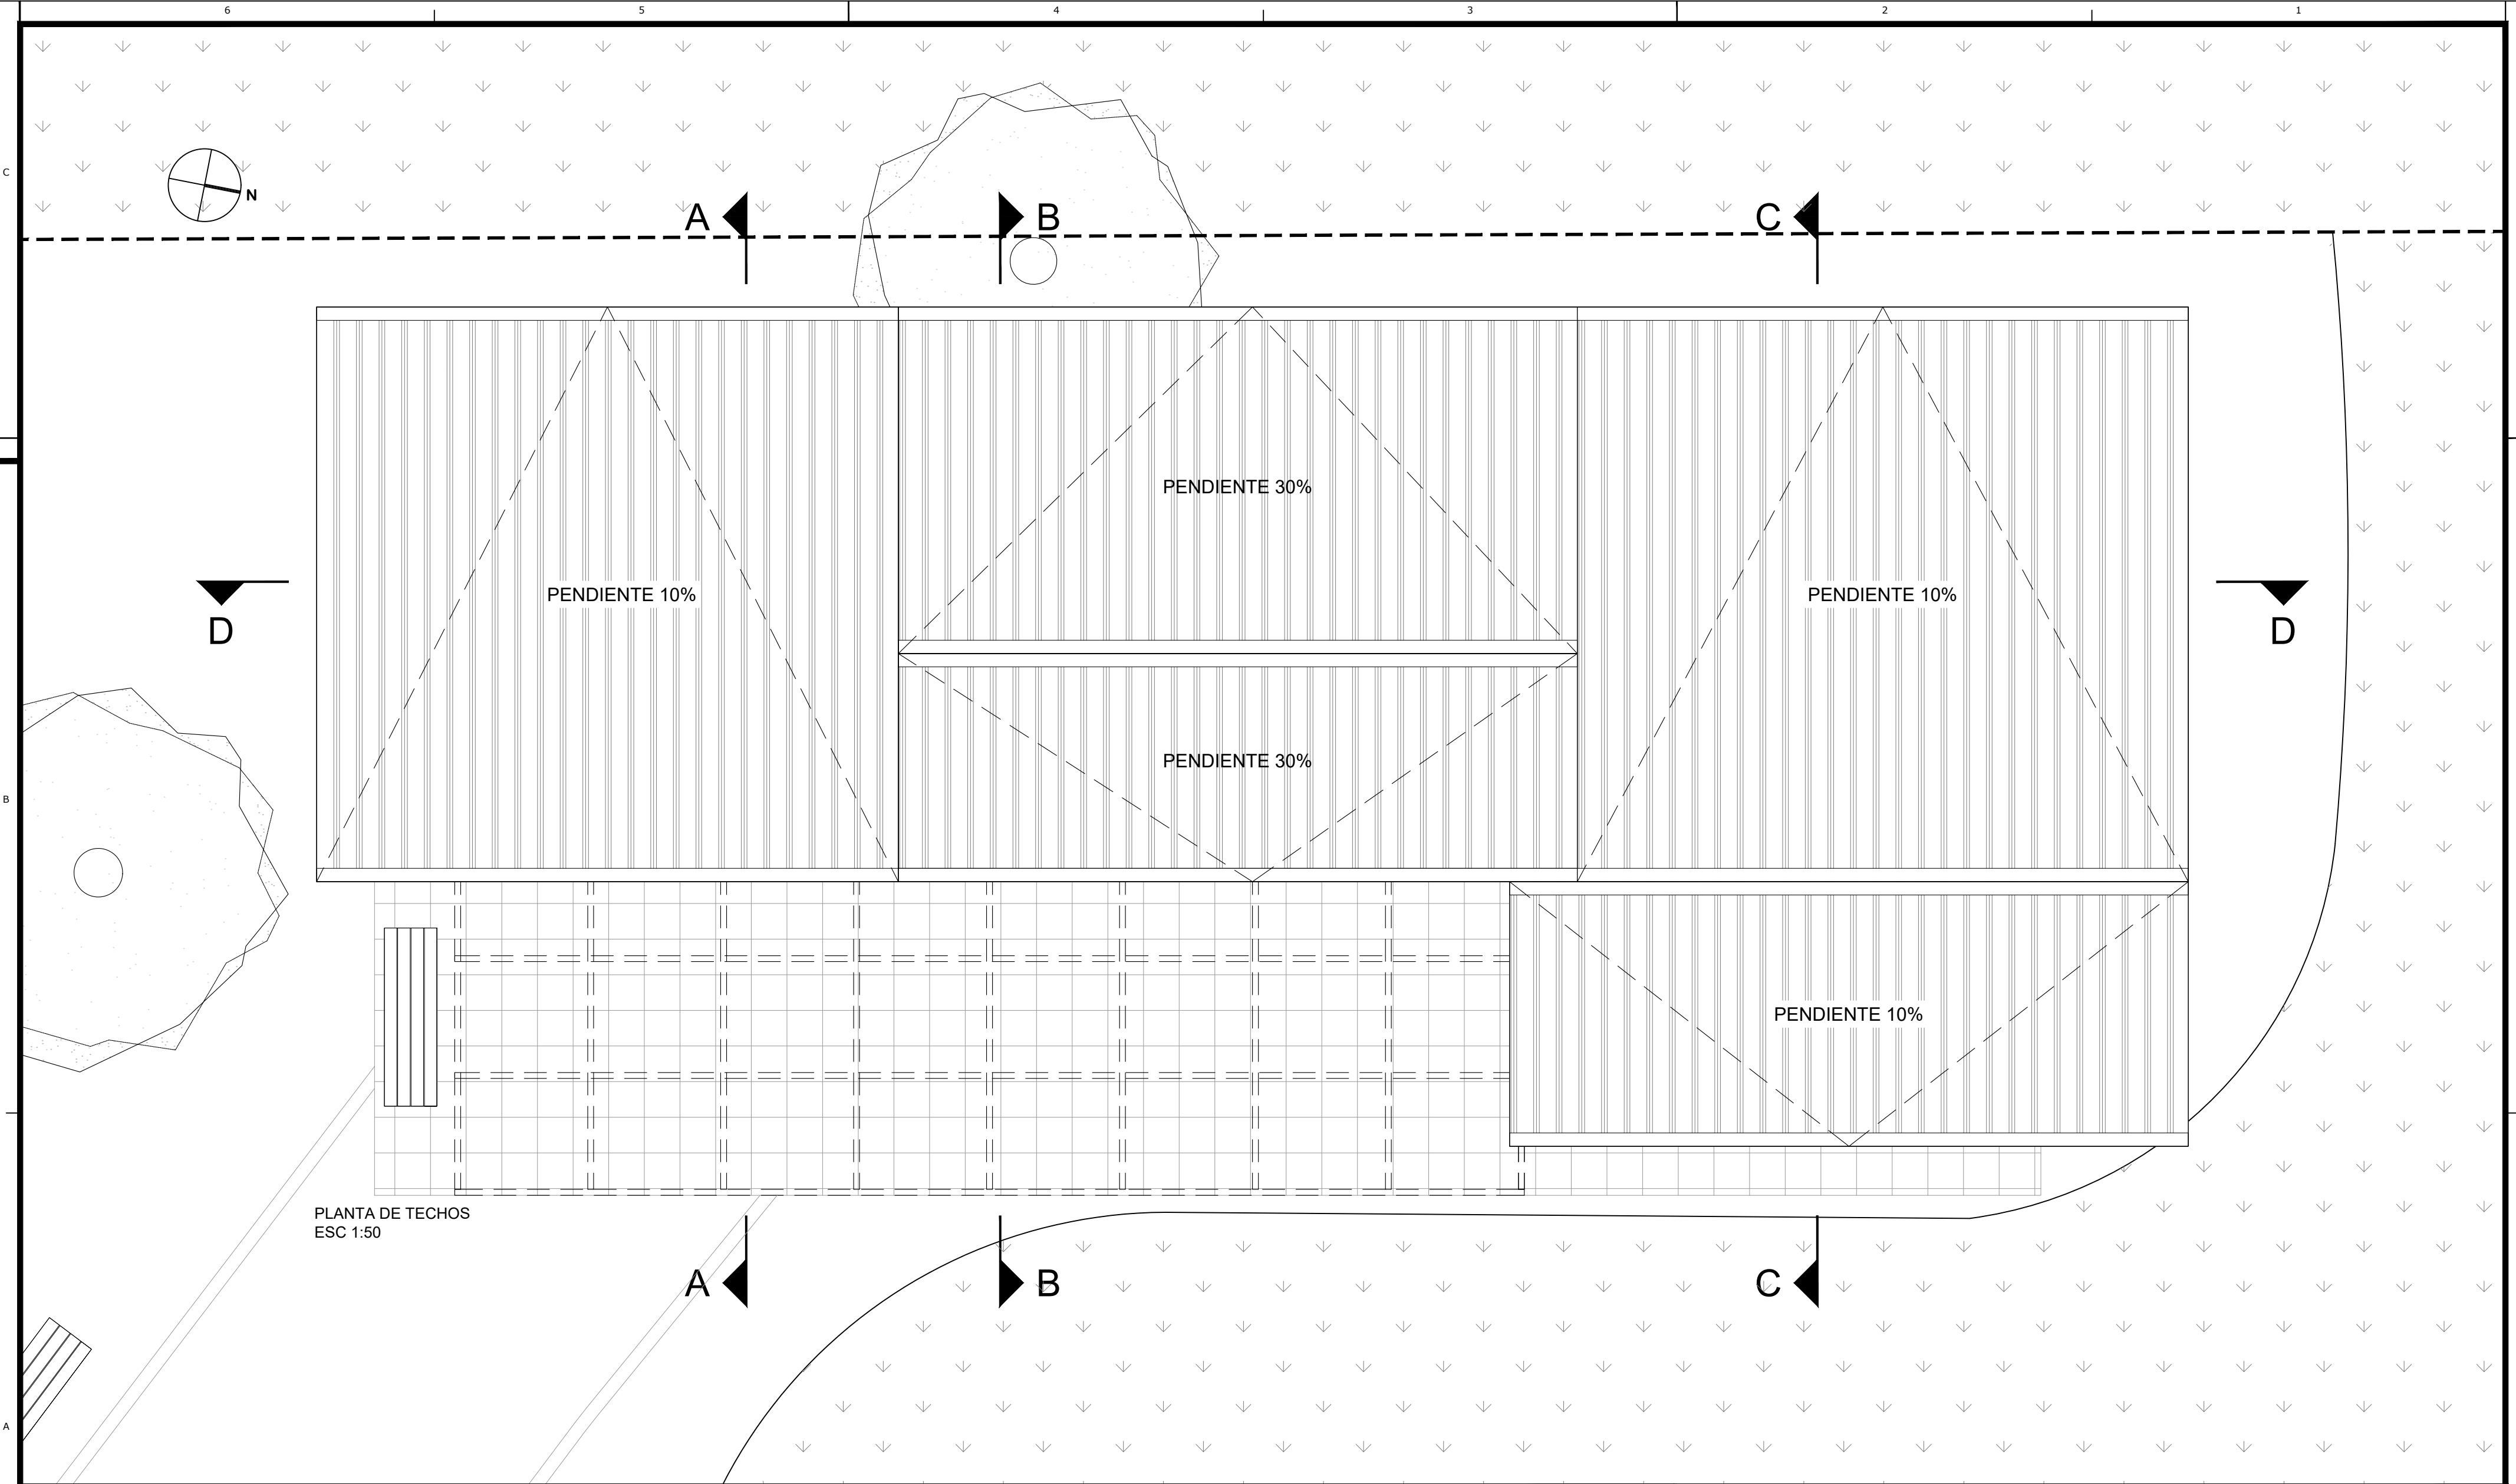


PLANTA DE TECHOS  
ESC 1:50

NOTAS


|   |  |                                 |           |   |  |                                                                                       |  |
|---|--|---------------------------------|-----------|---|--|---------------------------------------------------------------------------------------|--|
| NOTAS   |  |                                 |           | LA PRESENTE DOCUMENTACIÓN ES INDICATIVA. EL CONTRATISTA EJECUTARÁ LA DOCUMENTACIÓN CONSTRUCTIVA DE LA OBRA, GENERAL Y DE DETALLE, LA CUAL DEBERÁ SER APROBADA POR LA DIRECCIÓN GENERAL DE ÁREAS DE CONSERVACIÓN Y RESTAURACIÓN AMBIENTAL. TODAS LAS MEDIDAS Y NIVELES SERÁN VERIFICADAS EN OBRA. |  |                                                                                       |  |
| GOBIERNO DE LA CIUDAD DE BUENOS AIRES<br>SUBSECRETARIA DE AMBIENTE<br>DIRECCION GENERAL DE AREAS DE CONSERVACION Y RESTAURACION AMBIENTAL |  |                                 |           | GERENCIA OPERATIVA DE INFRAESTRUCTURA   |  |  |  |
| OBRA   |  | RESERVA ECOLÓGICA COSTANERA SUR |           | DIBUJO   |  |                                                                                       |  |
| PLANO   |  | PLANTA DE TECHOS                |           | REVISO   |  |                                                                                       |  |
| ARCHIVO   |  | RECS - BAÑOS VIAMONTE           | EXpte. Nº | 1F-2025-21464165-GCABA-DGACRA   |  | APROBO                                                                                |  |
| ESCALA   |  |                                 | FECHA     | ENERO 2025   |  | Nº PLANO                                                                              |  |
|   |  |                                 |           |   |  | RECS_BV_PT_1.3                                                                        |  |

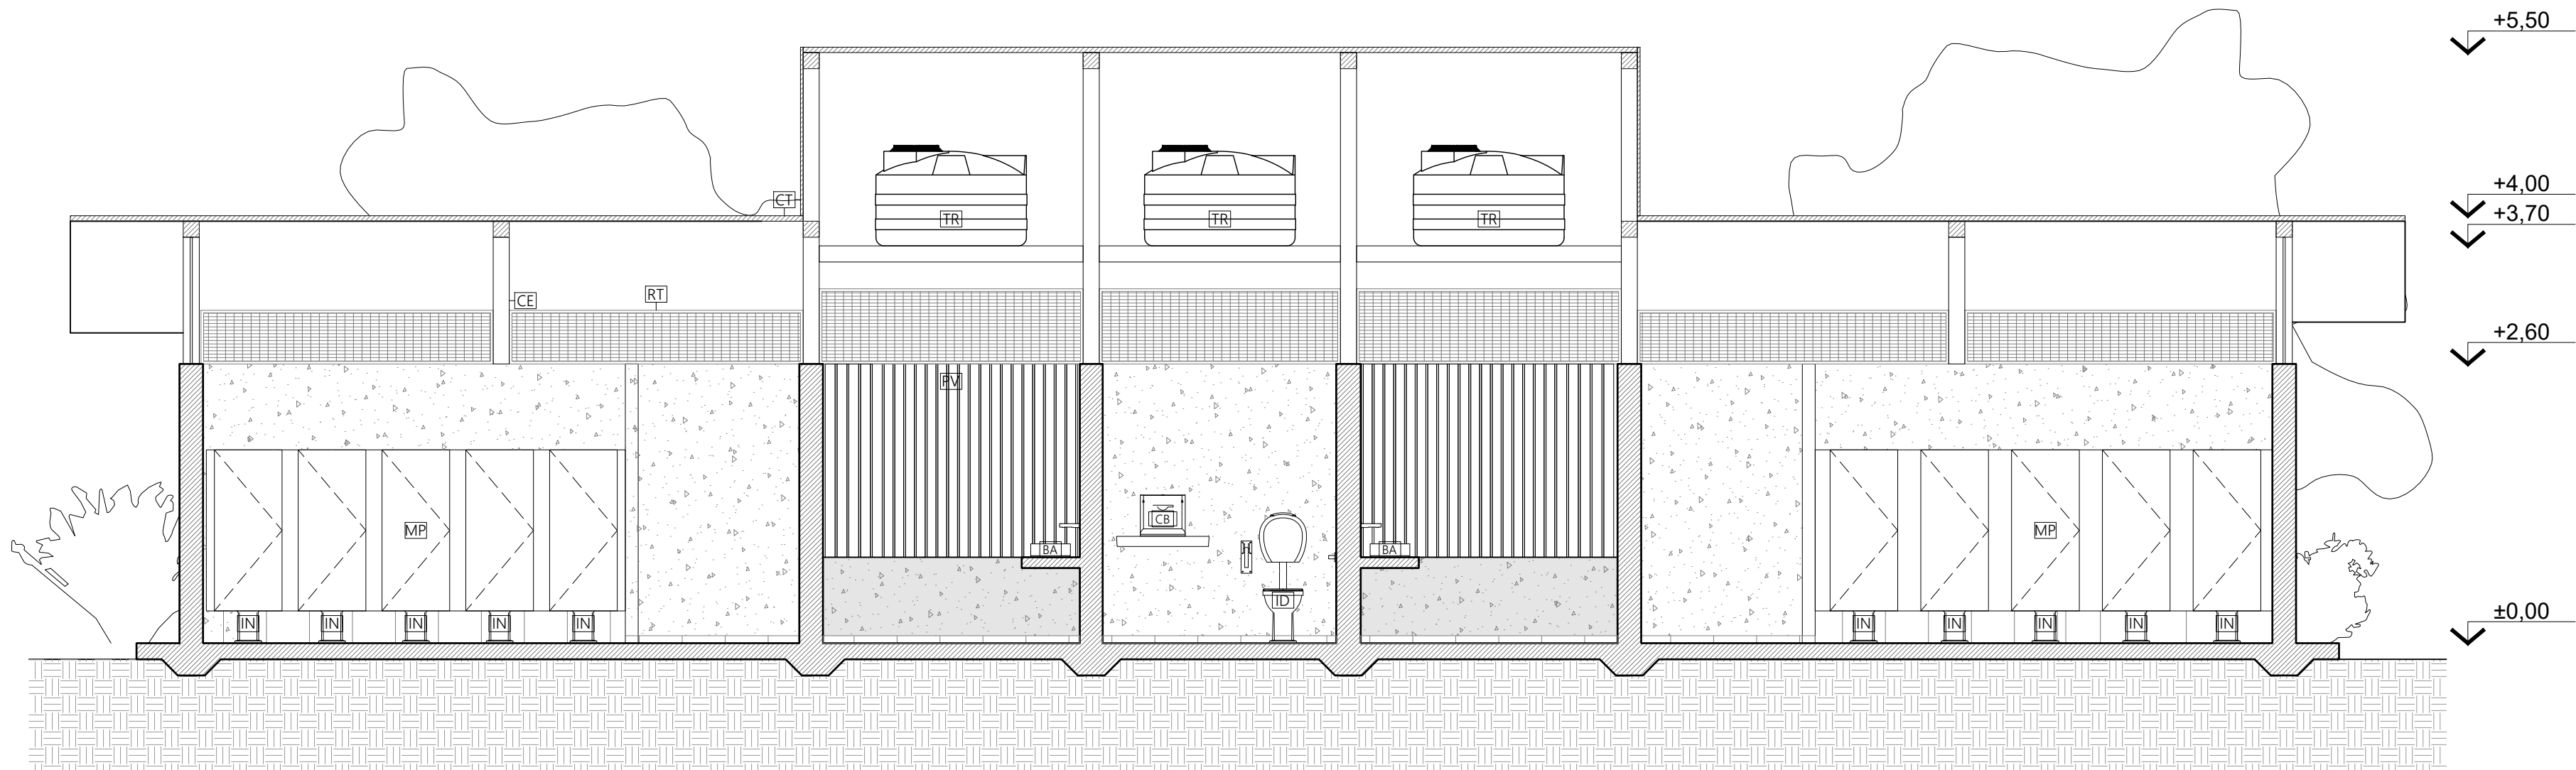

CORTE D-D  
ESC 1:50

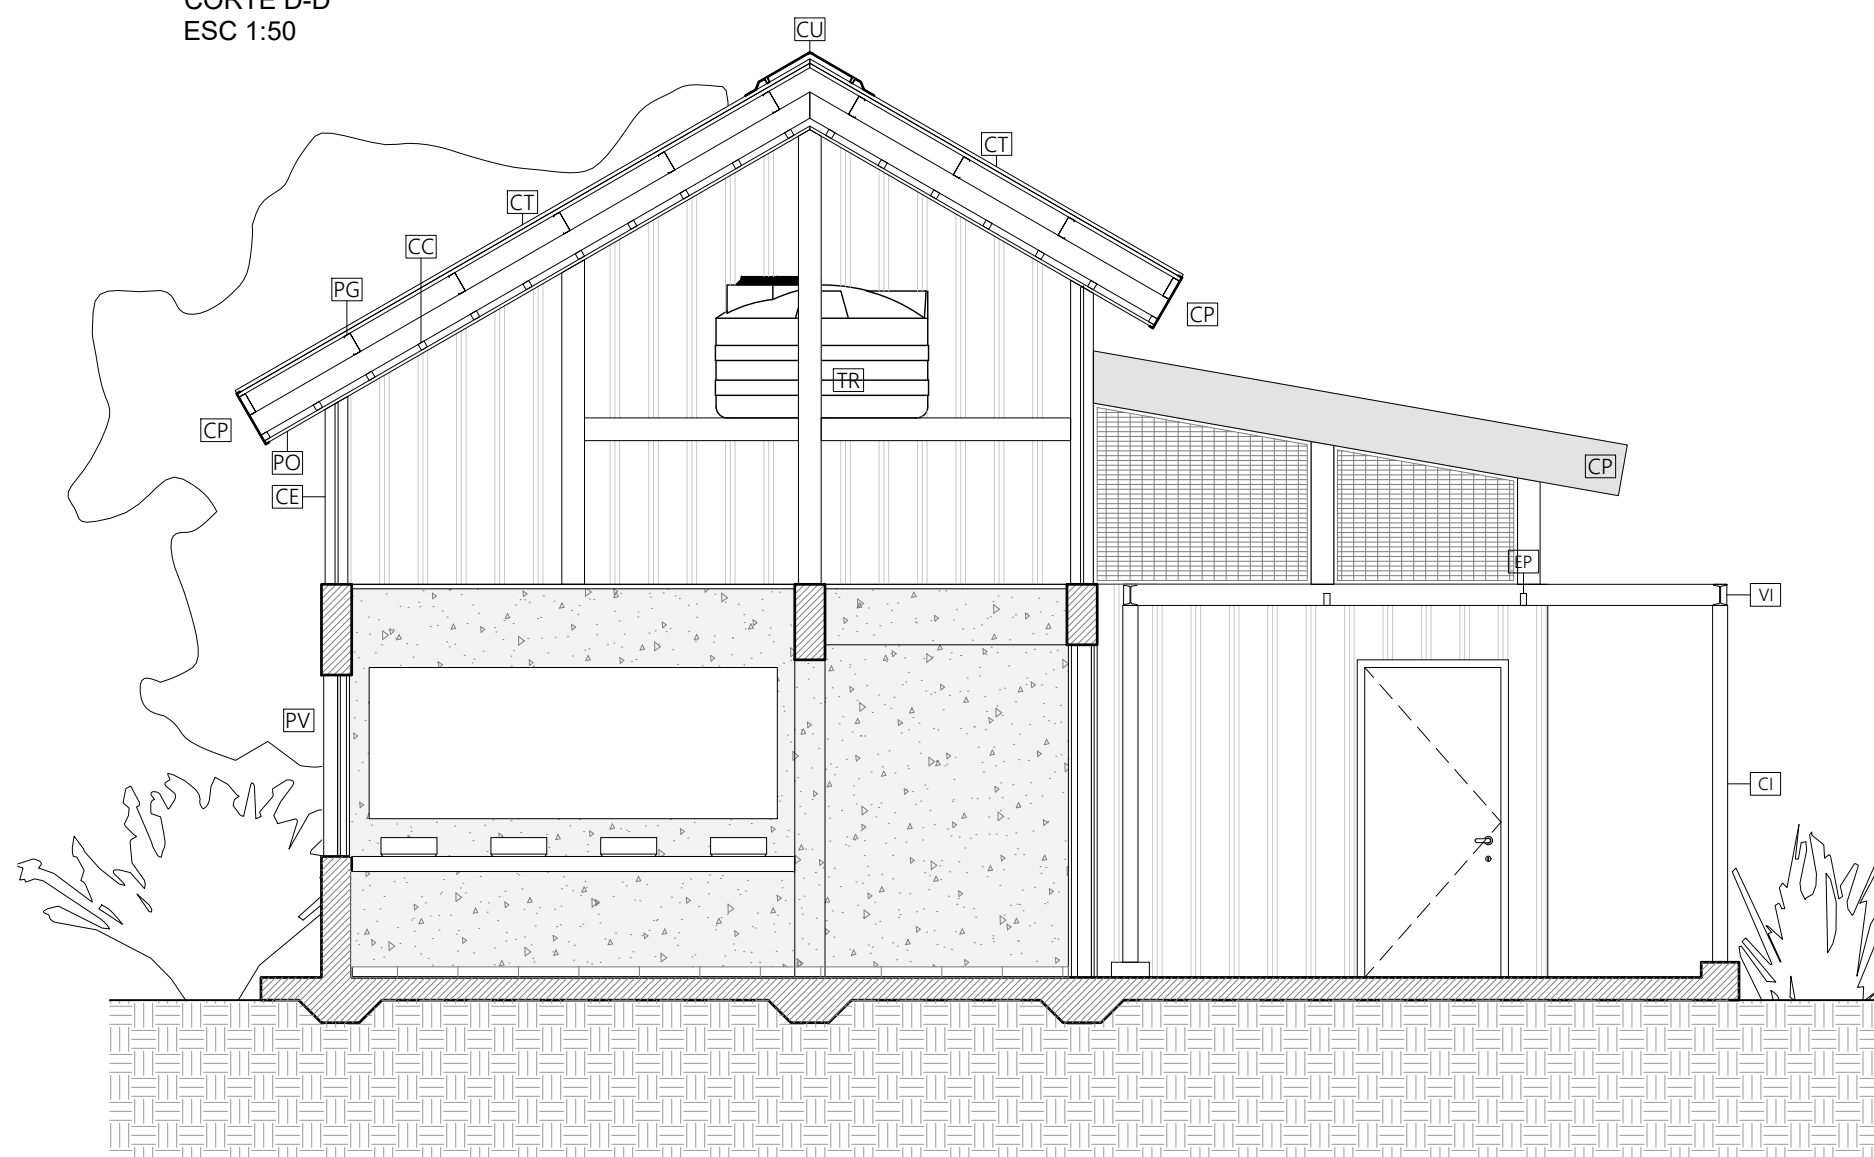

CORTE B-B  
ESC 1:50

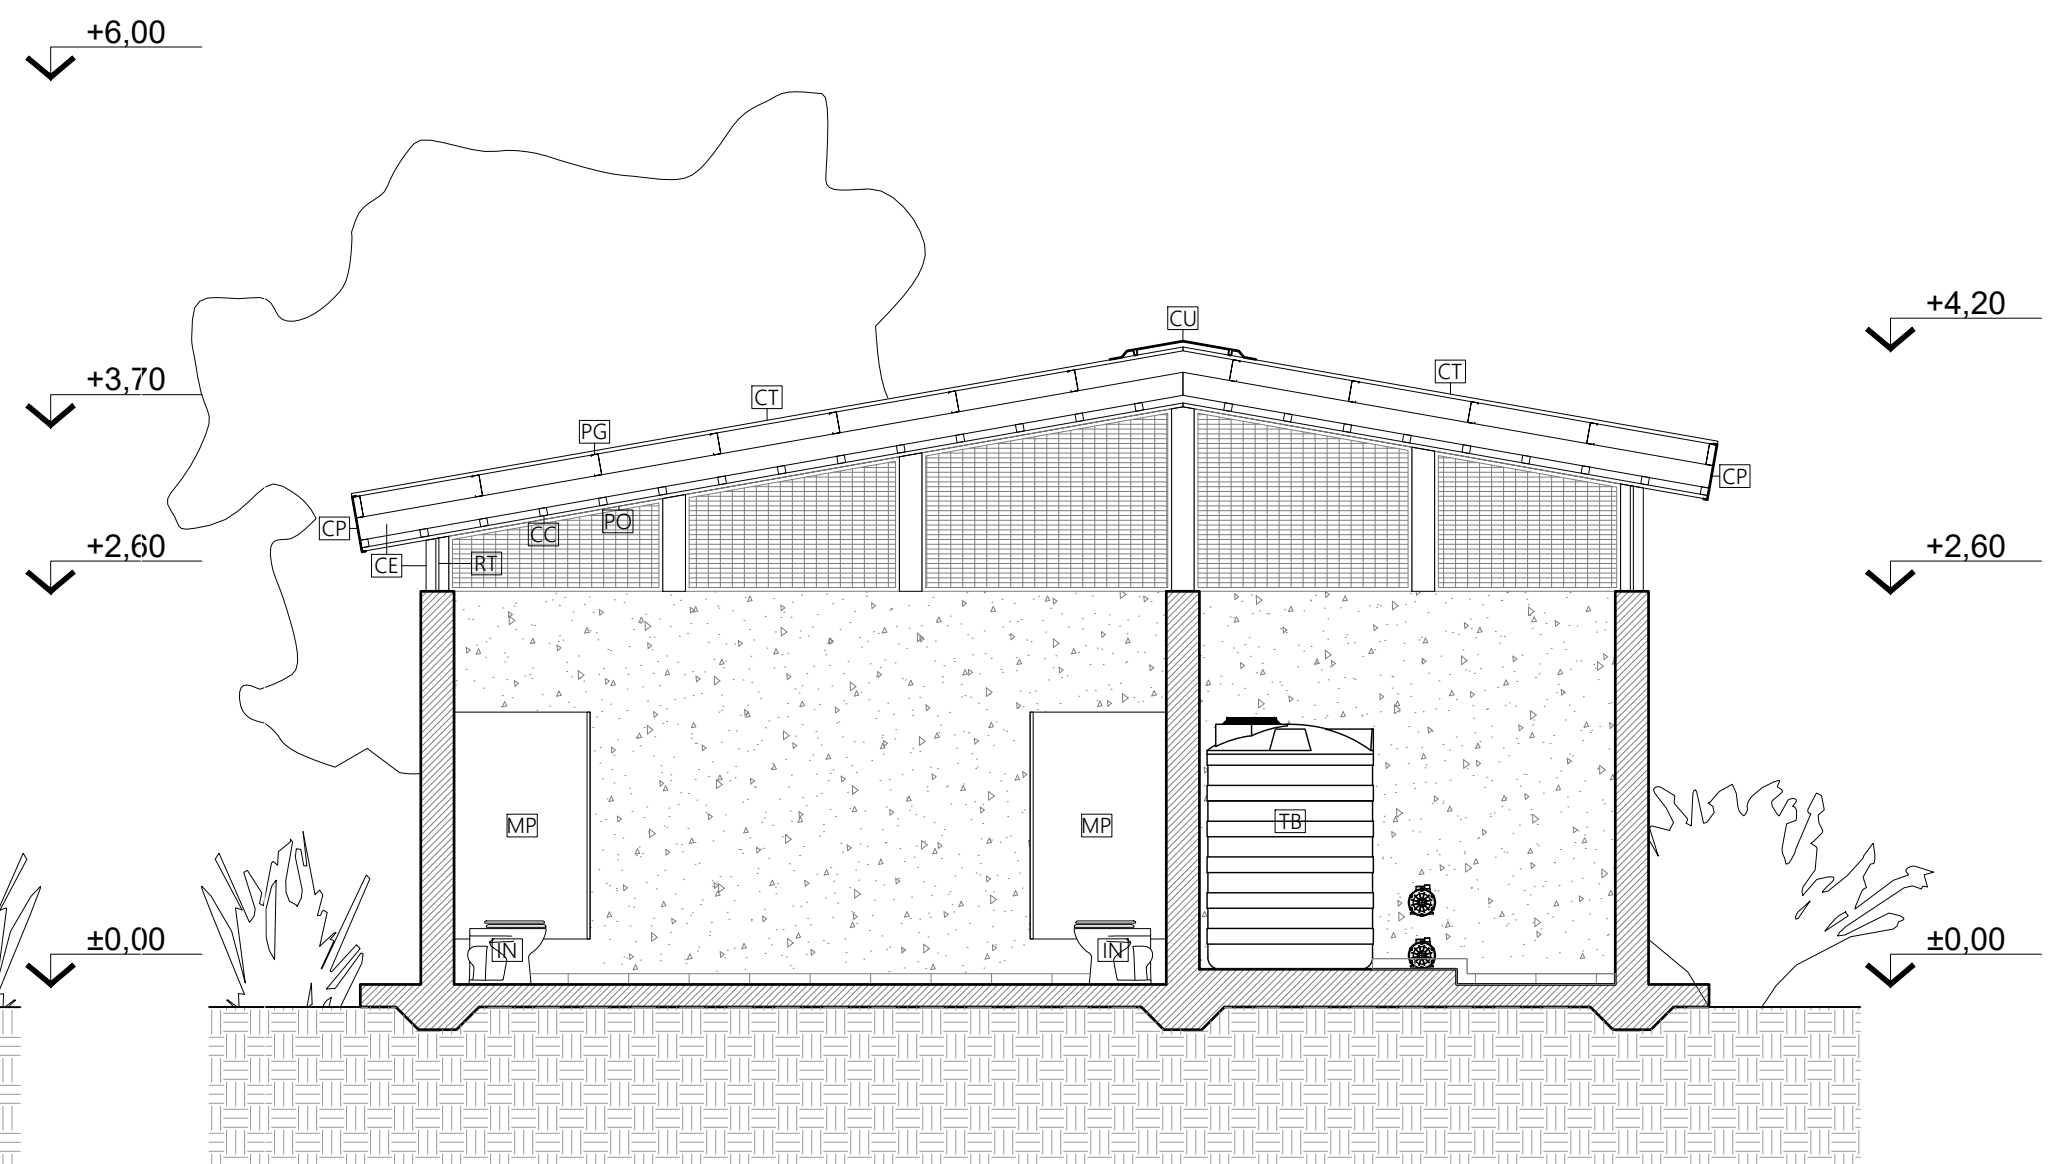

CORTE C-C  
ESC 1:50

#### REFERENCIAS


CE CAÑO ESTRUCTURAL 150 X 150 X 3,2 MM  
CC CAÑO ESTRUCTURAL 50 X 50 X 2 MM  
PG PERFIL PGC 120  
CI COLUMNA IPN 140  
VI VIGA IPN 140  
EP CAÑO ESTRUCTURAL 80 X 40 X 2 MM  
CT CHAPA TRAPEZOIDAL

CP CENEFAS PERIMETRALES  
CU CUMBRERA  
PO PLACA OSB  
RT REJA TECHNO  
MP MAMPARA SANITARIA  
IN INODORO CORTO  
IN INODORO NIÑOS


ID INODORO PERSONAS CON DISCAPACIDAD  
MM MINGITORIO MURAL  
CB CAMBIADOR BEBES  
BA BACHA TIPO SQUARE  
TB TANQUE DE BOMBEO CAP: 1500 L  
TR TANQUE DE RESERVA CHATO CAP: 1000 L  
PV PARASOLES VERTICALES WPC

|                                                                     |  |  |  |   |  |  |  |
|---------------------------------------------------------------------|--|--|--|---|--|--|--|
| NOTAS                                                               |  |  |  | LA PRESENTE DOCUMENTACIÓN ES INDICATIVA. EL CONTRATISTA EJECUTARÁ LA DOCUMENTACIÓN CONSTRUCTIVA DE LA OBRA, GENERAL Y DE DETALLE, LA CUAL DEBERÁ SER APROBADA POR LA DIRECCIÓN GENERAL DE ÁREAS DE CONSERVACIÓN Y RESTAURACIÓN AMBIENTAL. TODAS LAS MEDIDAS Y NIVELES SERÁN VERIFICADAS EN OBRA. |  |  |  |
| GOBIERNO DE LA CIUDAD DE BUENOS AIRES                               |  |  |  | SUBSECRETARÍA DE AMBIENTE   |  |  |  |
| DIRECCIÓN GENERAL DE ÁREAS DE CONSERVACIÓN Y RESTAURACIÓN AMBIENTAL |  |  |  | GERENCIA OPERATIVA DE INFRAESTRUCTURA   |  |  |  |
| OBRA                                                                |  |  |  | RESERVA ECOLÓGICA COSTANERA SUR   |  |  |  |
| PLANO                                                               |  |  |  | CORTES   |  |  |  |
| ARCHIVO                                                             |  |  |  | RECS - BAÑOS VIAMONTE   |  |  |  |
| ESCALA                                                              |  |  |  | EXPT. N°   |  |  |  |
|                                                                     |  |  |  | FECHA   |  |  |  |
|                                                                     |  |  |  | ENERO 2025   |  |  |  |
|                                                                     |  |  |  | 1F-2025-21464165-GCABA-DGACRA   |  |  |  |
|                                                                     |  |  |  | N° PLANO   |  |  |  |
|                                                                     |  |  |  | RECS_BV_COR_1.4   |  |  |  |

VISTA FRENTE  
ESC 1:50

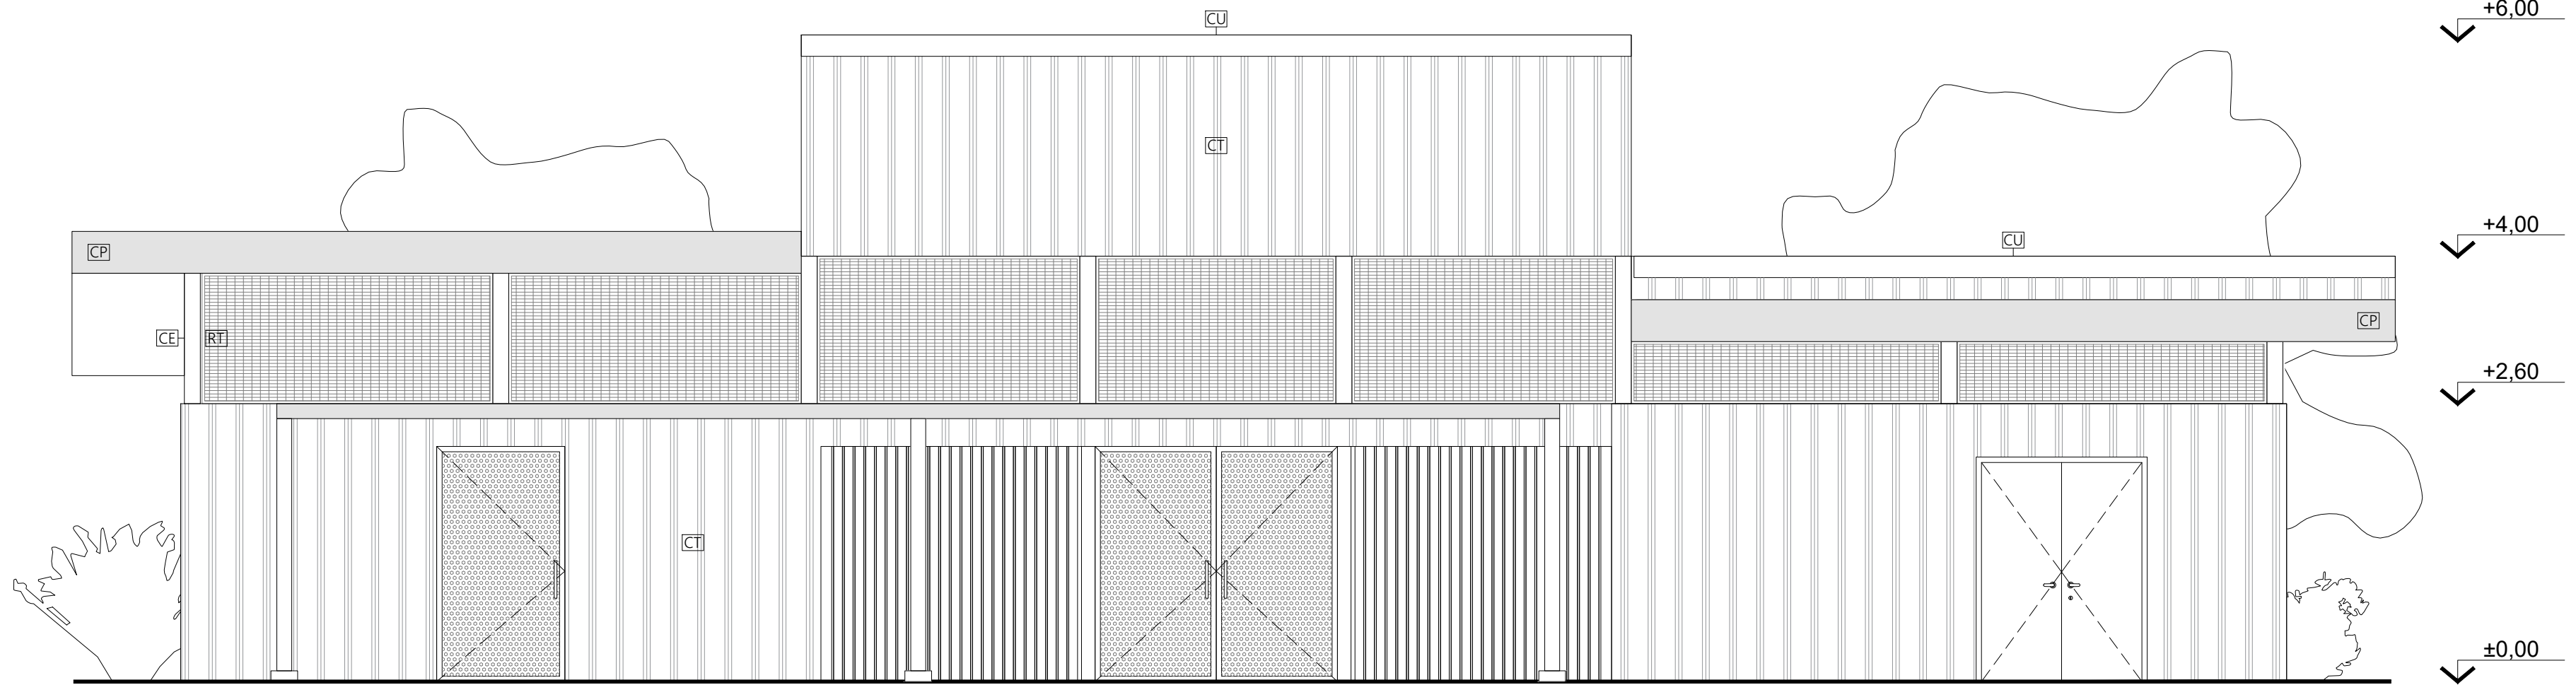

CORTE A-A  
ESC 1:50

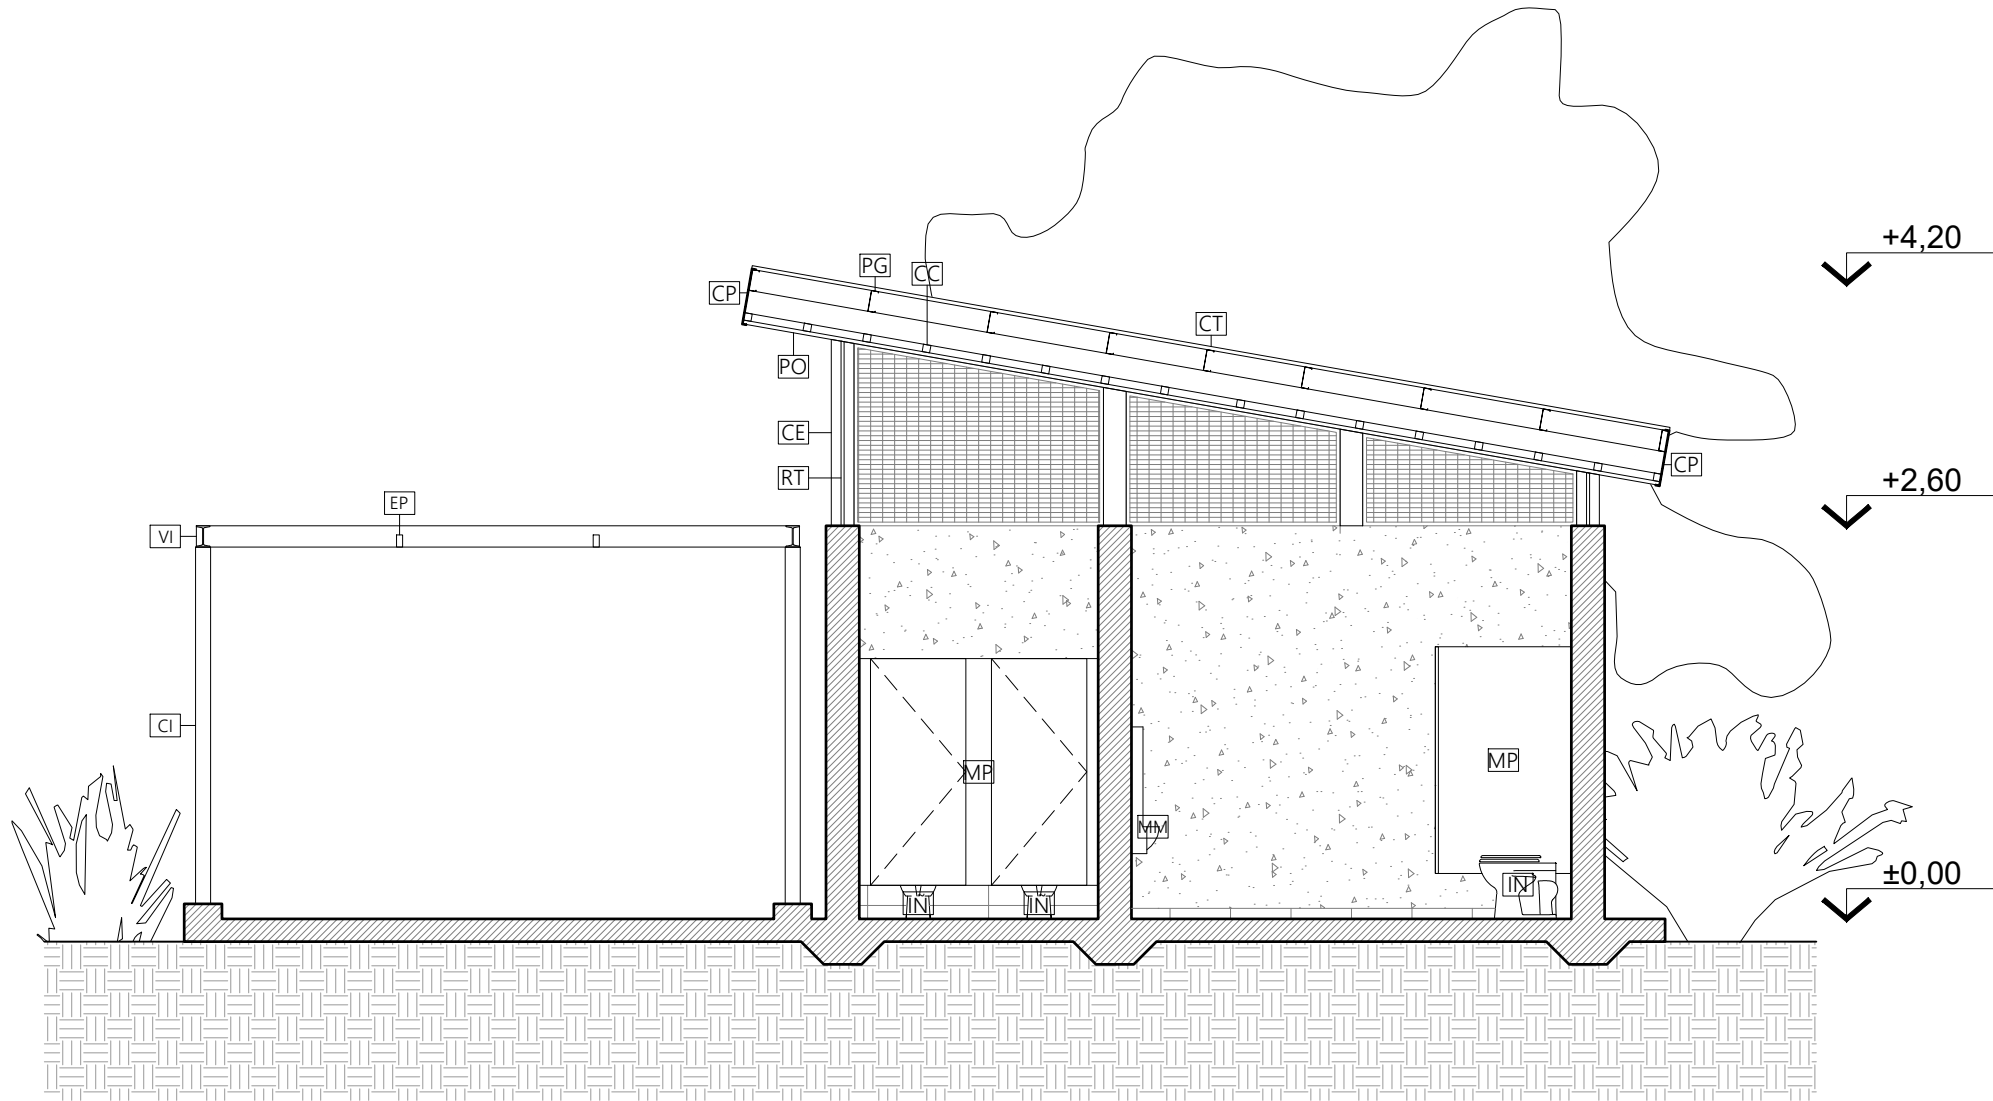


VISTA LATERAL  
ESC 1:50



REFERENCIAS

|                                                 |                               |                                                 |
|-------------------------------------------------|-------------------------------|-------------------------------------------------|
| <b>[CE]</b> CAÑO ESTRUCTURAL 150 X 150 X 3,2 MM | <b>[CP]</b> CENEFa PERIMETRAL | <b>[ID]</b> INODORO PERSONAS CON DISCAPACIDAD   |
| <b>[CC]</b> CAÑO ESTRUCTURAL 50 X 50 X 2 MM     | <b>[CU]</b> CUMBRERA          | <b>[MM]</b> MINGITORIO MURAL                    |
| <b>[PG]</b> PERFIL PGC 120                      | <b>[PO]</b> PLACA OSB         | <b>[CB]</b> CAMBIADOR BEBES                     |
| <b>[CI]</b> COLUMNA IPN 140                     | <b>[RT]</b> REJA TECHNO       | <b>[BA]</b> BACHA TIPO SQUARE                   |
| <b>[VI]</b> VIGA IPN 140                        | <b>[MP]</b> MAMPARA SANITARIA | <b>[TB]</b> TANQUE DE BOMBEO CAP: 1500 L        |
| <b>[EP]</b> CAÑO ESTRUCTURAL 80 X 40 X 2 MM     | <b>[IN]</b> INODORO CORTO     | <b>[TR]</b> TANQUE DE RESERVA CHATO CAP: 1000 L |
| <b>[CT]</b> CHAPA TRAPEZOIDAL                   | <b>[IN]</b> INODORO NIÑOS     | <b>[PV]</b> PARASOLES VERTICALES WPC            |

|   |                       |   |                                       |                 |                                                                                       |
|---|-----------------------|---|---------------------------------------|-----------------|---------------------------------------------------------------------------------------|
| NOTAS   |                       | LA PRESENTE DOCUMENTACIÓN ES INDICATIVA. EL CONTRATISTA EJECUTARÁ LA DOCUMENTACIÓN CONSTRUCTIVA DE LA OBRA, GENERAL Y DE DETALLE, LA CUAL DEBERÁ SER APROBADA POR LA DIRECCIÓN GENERAL DE ÁREAS DE CONSERVACIÓN Y RESTAURACIÓN AMBIENTAL. TODAS LAS MEDIDAS Y NIVELES SERÁN VERIFICADAS EN OBRA. |                                       |                 |                                                                                       |
| GOBIERNO DE LA CIUDAD DE BUENOS AIRES<br>SUBSECRETARIA DE AMBIENTE<br>DIRECCION GENERAL DE AREAS DE CONSERVACION Y RESTAURACION AMBIENTAL |                       |   | GERENCIA OPERATIVA DE INFRAESTRUCTURA |                 |  |
| OBRA   |                       |   | RESERVA ECOLÓGICA COSTANERA SUR       |                 |                                                                                       |
| PLANO   |                       |   | CORTES                                |                 |                                                                                       |
| ARCHIVO   | RECS - BAÑOS VIAMONTE | EXPTE. Nº   | 1F-2025-21464165-GCABA-DGACRA         |                 |                                                                                       |
| ESCALA   |                       | FECHA   | ENERO 2025                            |                 |                                                                                       |
|   |                       |   | Nº PLANO                              | RECS_BV_VIS_1.5 |                                                                                       |

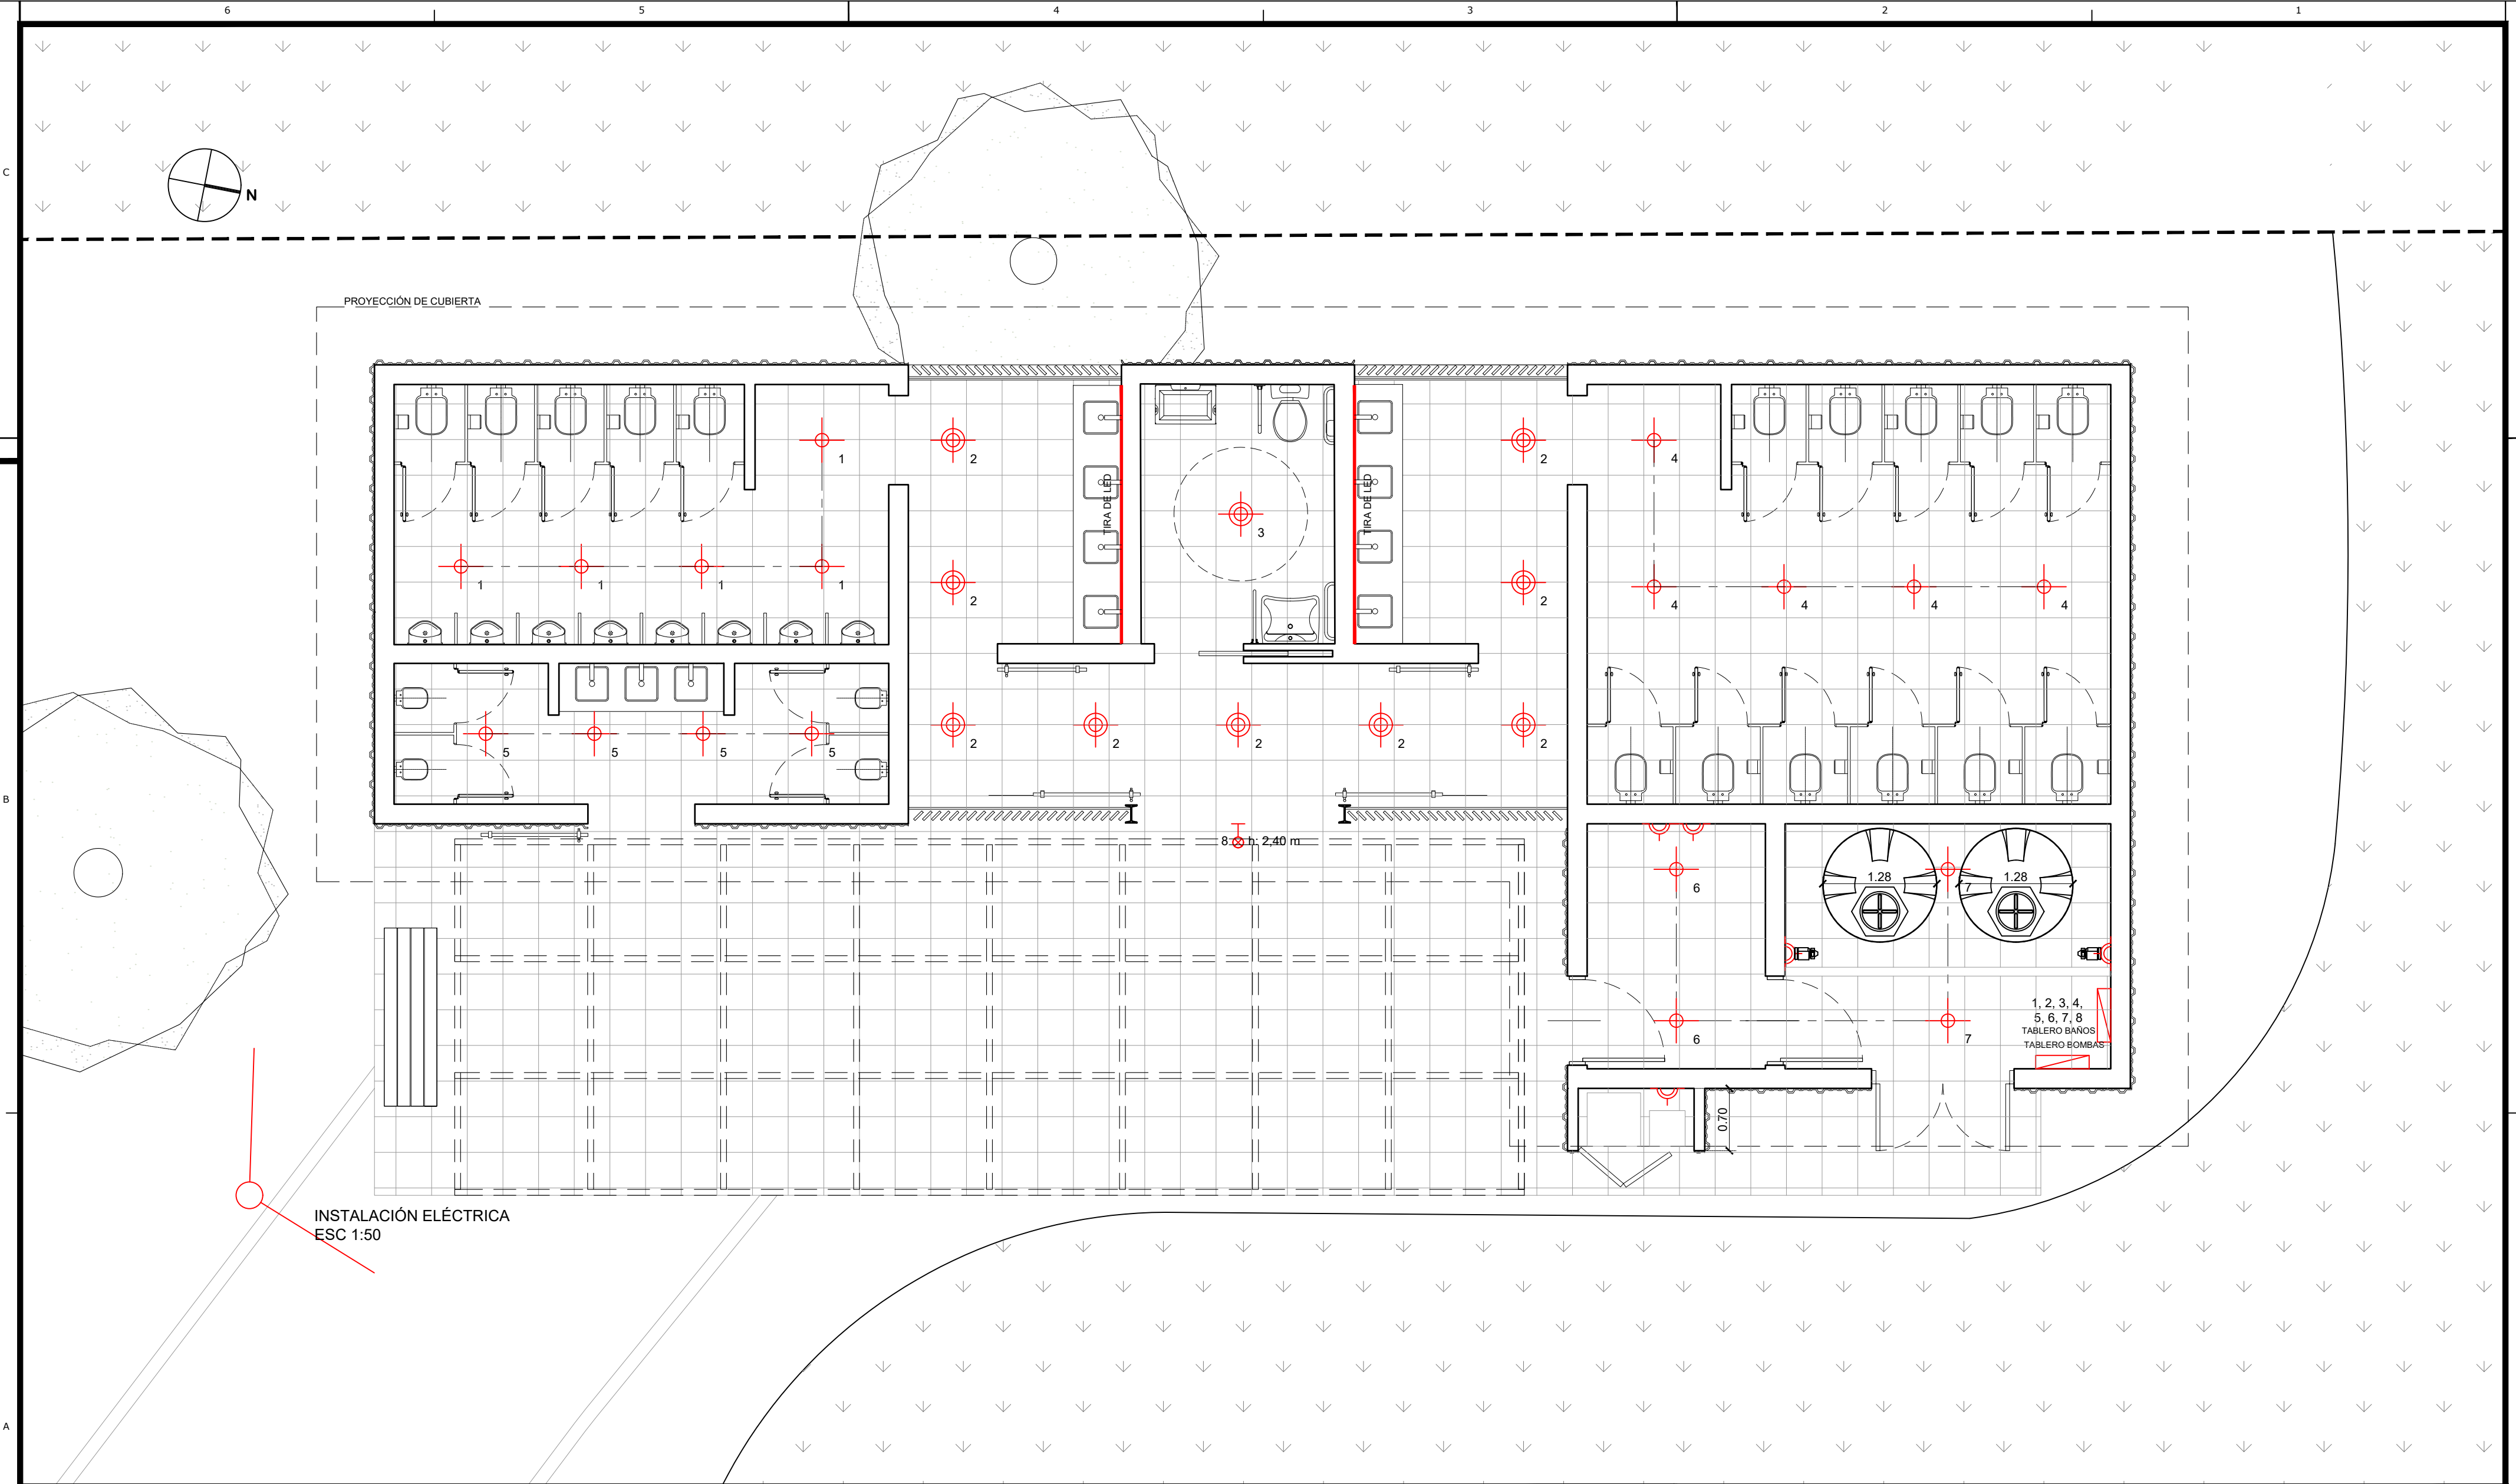

REFERENCIAS

 TOMA DOBLE

 BOCA DE ILUMINACIÓN  
APLIQUE ORIENTABLE P/ APLICAR SOBRE BANDEJAS

 BOCA DE ILUMINACIÓN  
APLIQUE P/ CIELORRASO

 TABLERO SECCIONAL

 TIRA DE LED CON FUENTE

 BOCA DE ILUMINACIÓN h: 2,40 m  
REFLECTOR C/ SENSOR DE MOVIMIENTO

 CÁMARA FIJA 120° + DOMO 360°

NOTAS

LA PRESENTE DOCUMENTACIÓN ES INDICATIVA. EL CONTRATISTA EJECUTARÁ LA DOCUMENTACIÓN CONSTRUCTIVA DE LA OBRA, GENERAL Y DE DETALLE, LA CUAL DEBERÁ SER APROBADA POR LA DIRECCIÓN GENERAL DE ÁREAS DE CONSERVACIÓN Y RESTAURACIÓN AMBIENTAL. TODAS LAS MEDIDAS Y NIVELES SERÁN VERIFICADAS EN OBRA.

GOBIERNO DE LA CIUDAD DE BUENOS AIRES

SUBSECRETARÍA DE AMBIENTE

DIRECCIÓN GENERAL DE ÁREAS DE CONSERVACIÓN Y RESTAURACIÓN AMBIENTAL

GERENCIA OPERATIVA DE INFRAESTRUCTURA



OBRA

RESERVA ECOLÓGICA COSTANERA SUR

DIBUJO

PLANO

INSTALACIÓN ELÉCTRICA

REVISO

ARCHIVO

RECS - BAÑOS VIAMONTE

EXPTE. Nº

1F-2025-21464165-GCABA-DGACRA

APROBO

ESCALA


FECHA

ENERO 2025

Nº PLANO

RECS\_BV\_IE\_2.0

Página 8 de 27


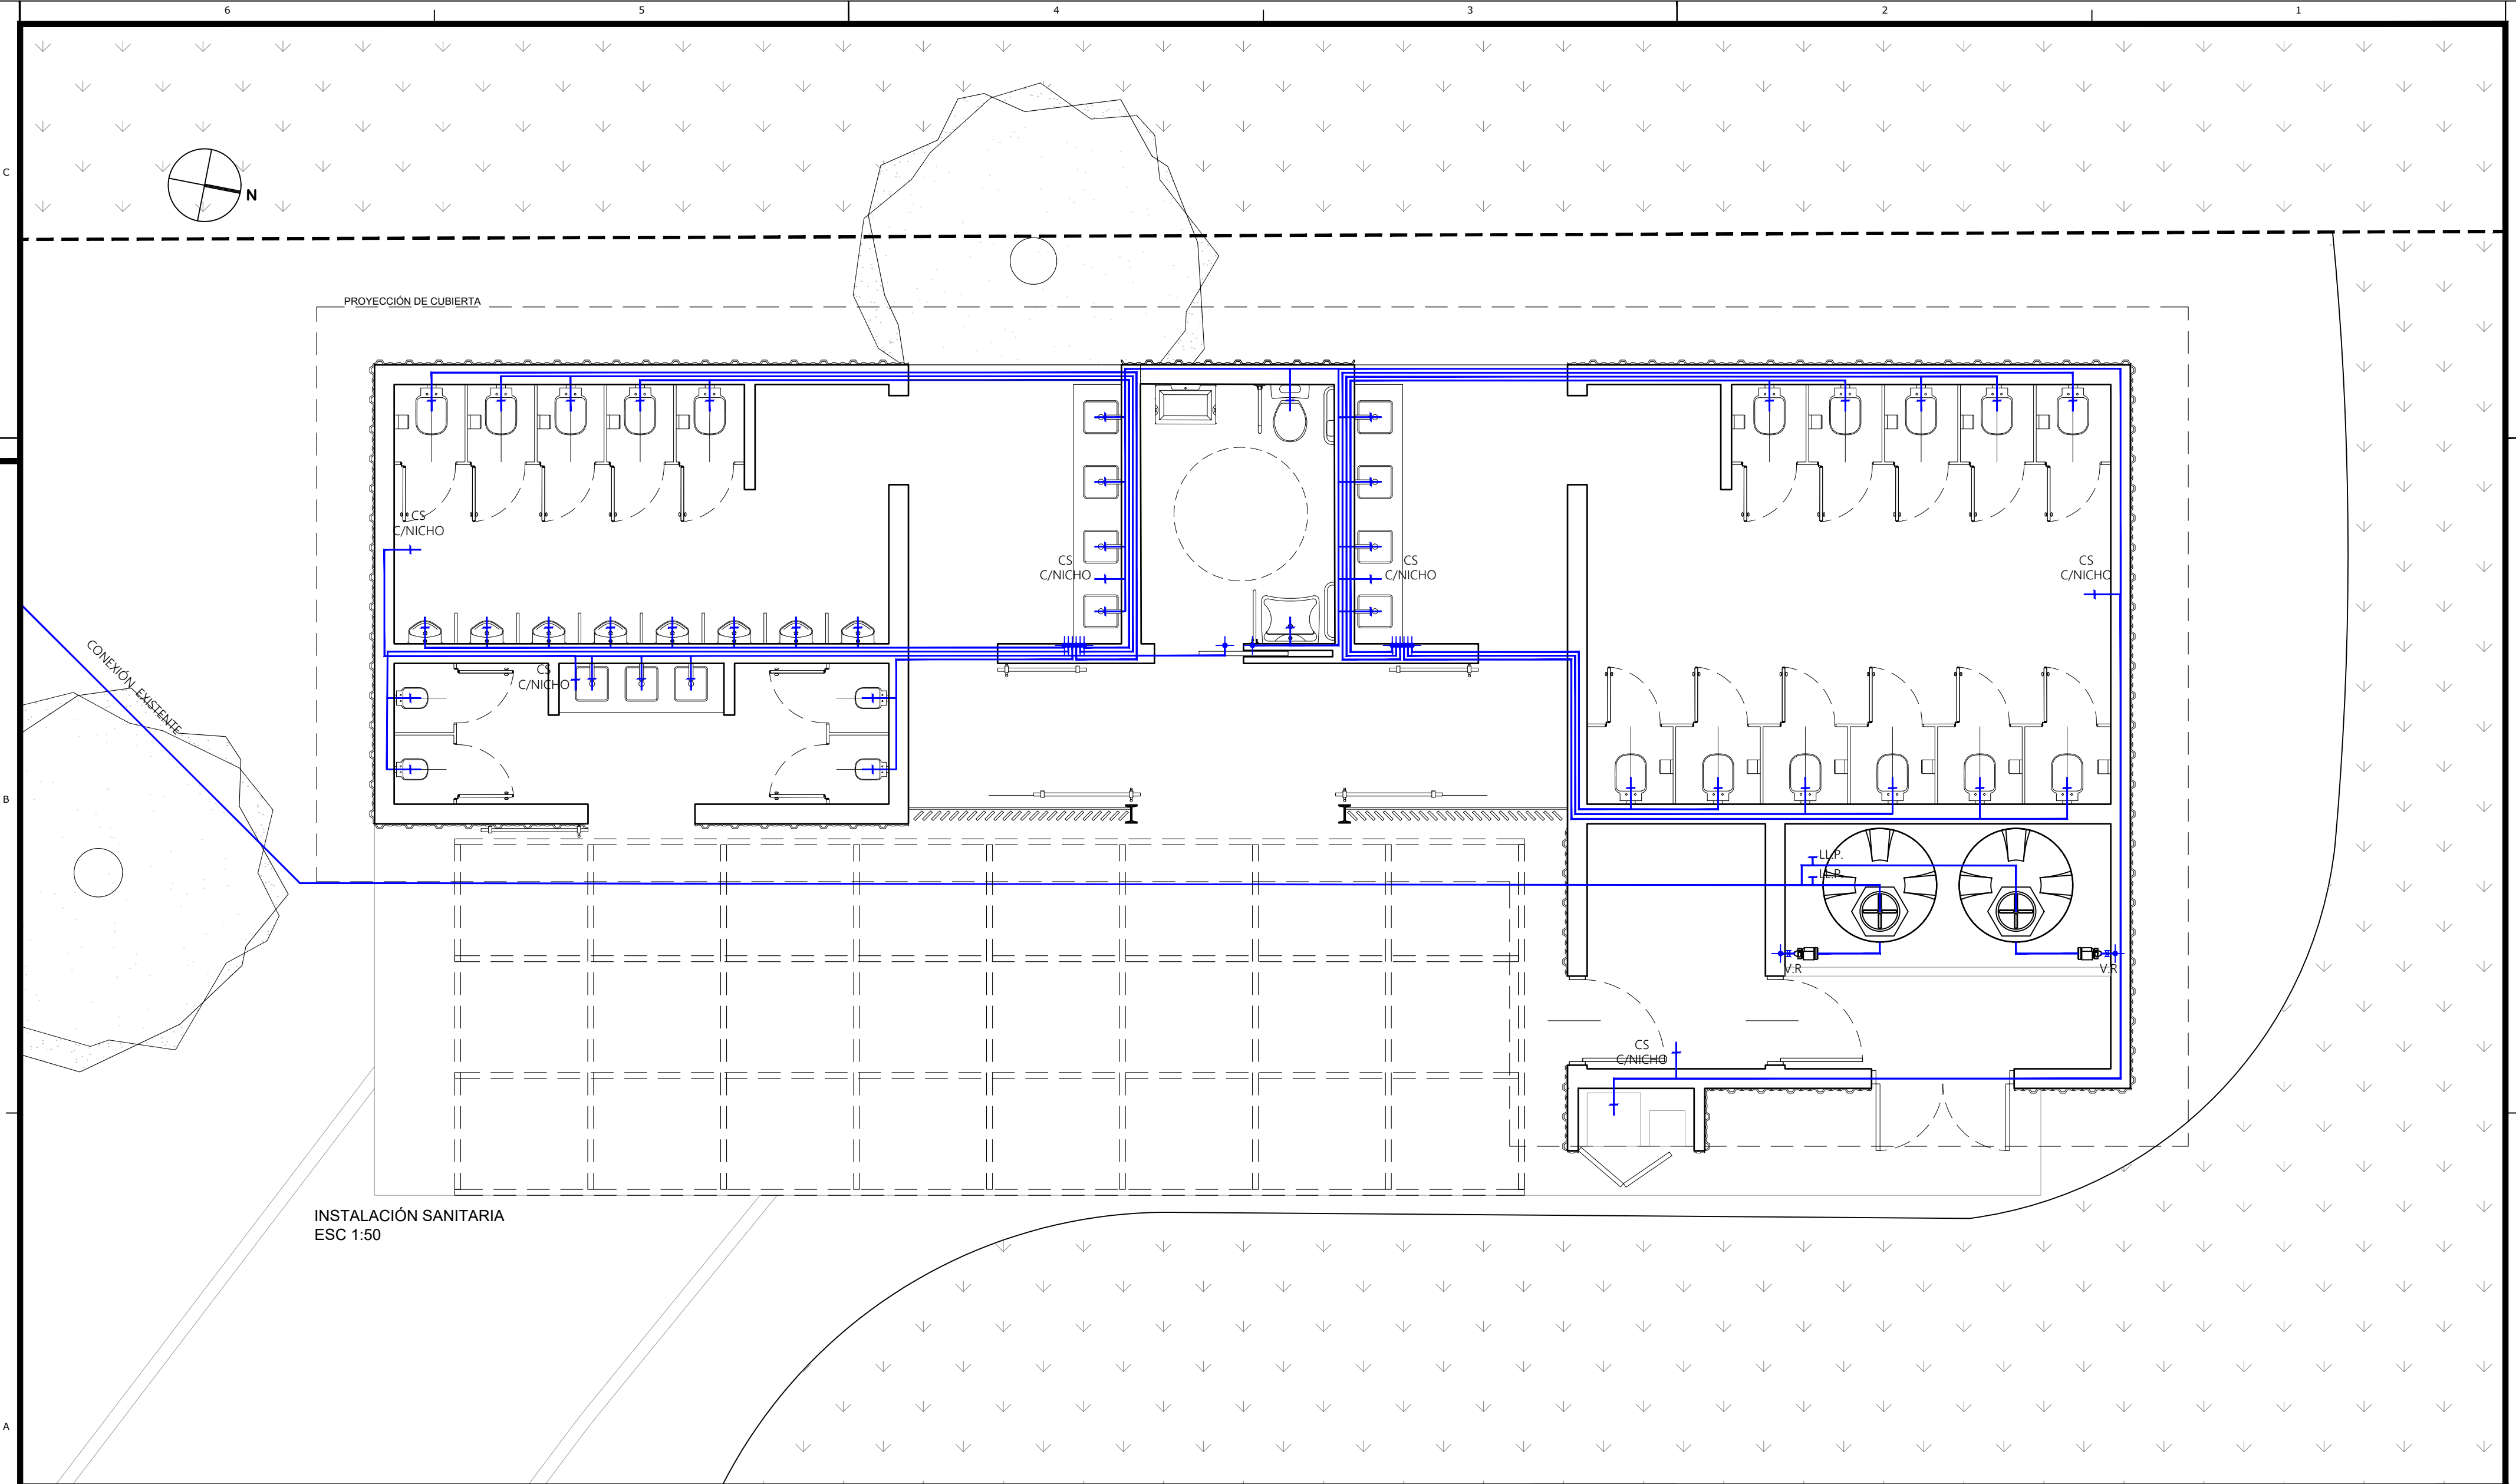


NOTAS

NOTAS


LA PRESENTE DOCUMENTACIÓN ES INDICATIVA. EL CONTRATISTA EJECUTARÁ LA DOCUMENTACIÓN CONSTRUCTIVA DE LA OBRA, GENERAL Y DE DETALLE, LA CUAL DEBERÁ SER APROBADA POR LA DIRECCIÓN GENERAL DE ÁREAS DE CONSERVACIÓN Y RESTAURACIÓN AMBIENTAL. TODAS LAS MEDIDAS Y NIVELES SERÁN VERIFICADAS EN OBRA.

|   |                       |          |                               |                                          |  |                 |
|---|-----------------------|----------|-------------------------------|------------------------------------------|--|-----------------|
| GOBIERNO DE LA CIUDAD DE BUENOS AIRES<br>SUBSECRETARIA DE AMBIENTE<br>DIRECCION GENERAL DE AREAS DE CONSERVACION Y<br>RESTAURACION AMBIENTAL |                       |          |                               | GERENCIA OPERATIVA DE<br>INFRAESTRUCTURA |  |                 |
| OBRA RESERVA ECOLÓGICA COSTANERA SUR   |                       |          |                               | DIBUJO                                   |  |                 |
| PLANO INSTALACIÓN SANITARIA   |                       |          |                               | REVISO                                   |  |                 |
|   |                       |          |                               | APROBO                                   |  |                 |
|   |                       |          |                               | Nº PLANO                                 |  |                 |
| ARCHIVO   | RECS - BAÑOS VIAMONTE | EXPT. Nº | 1F-2025-21464165-GCABA-DGACRA |                                          |  | RECS_BV_SAN_2.1 |
| ESCALA   |                       | FECHA    | ENERO 2025                    |                                          |  |                 |

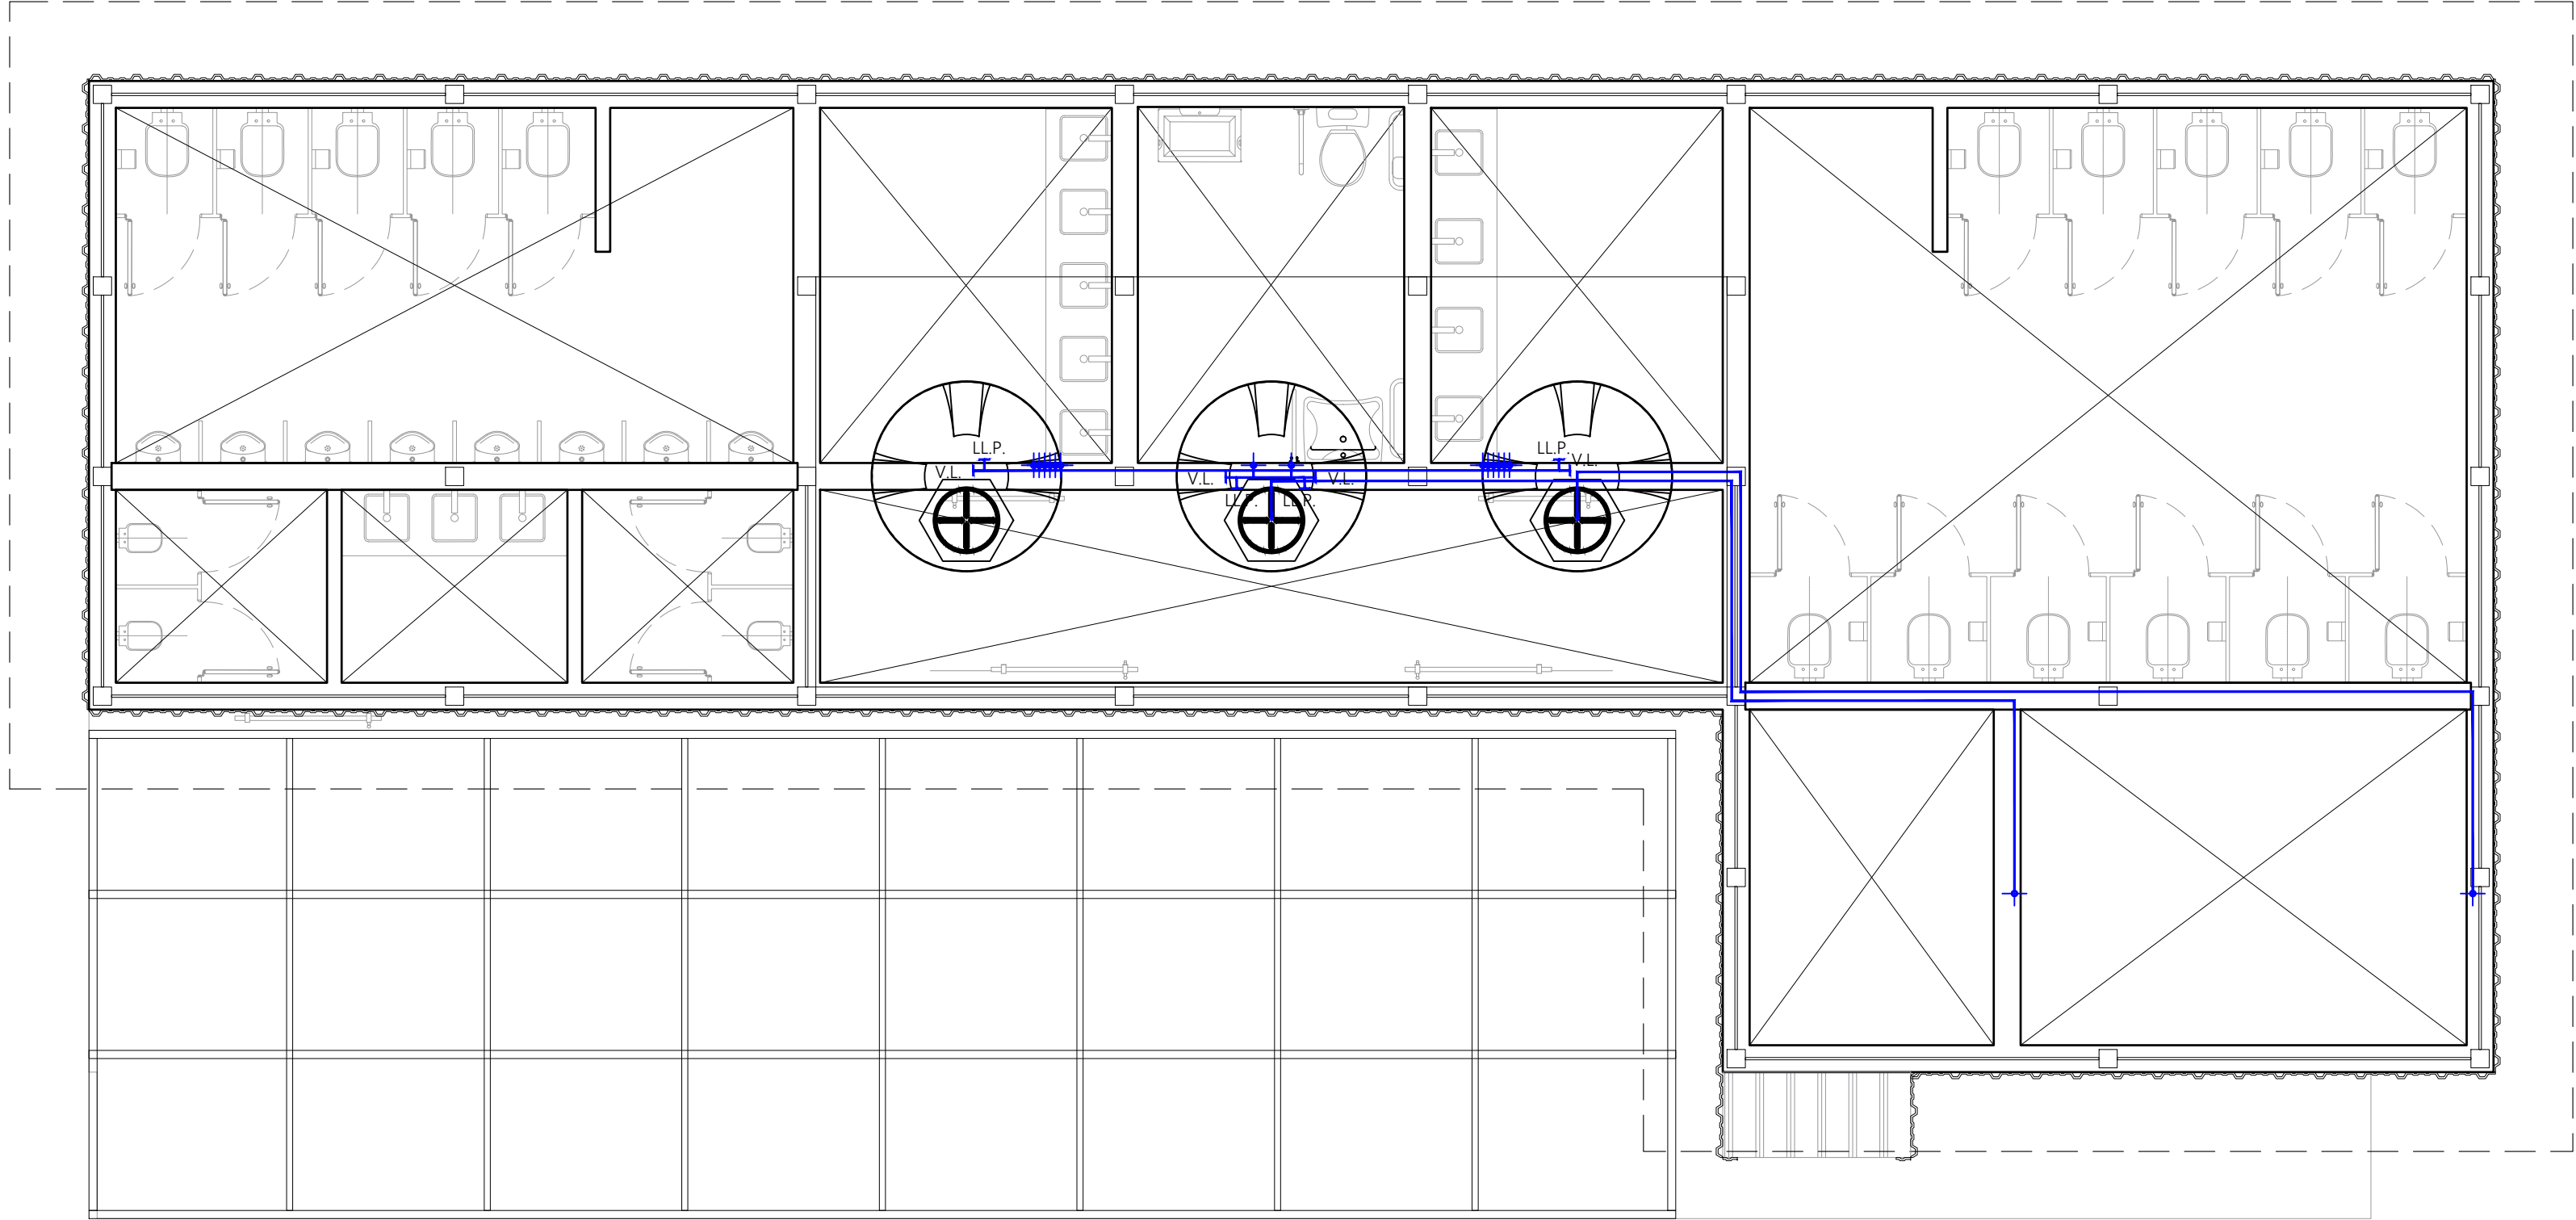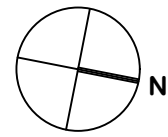


INSTALACIÓN SANITARIA +2,70  
ESC 1:50

ESQUEMA INSTALACIÓN  
SANITARIA

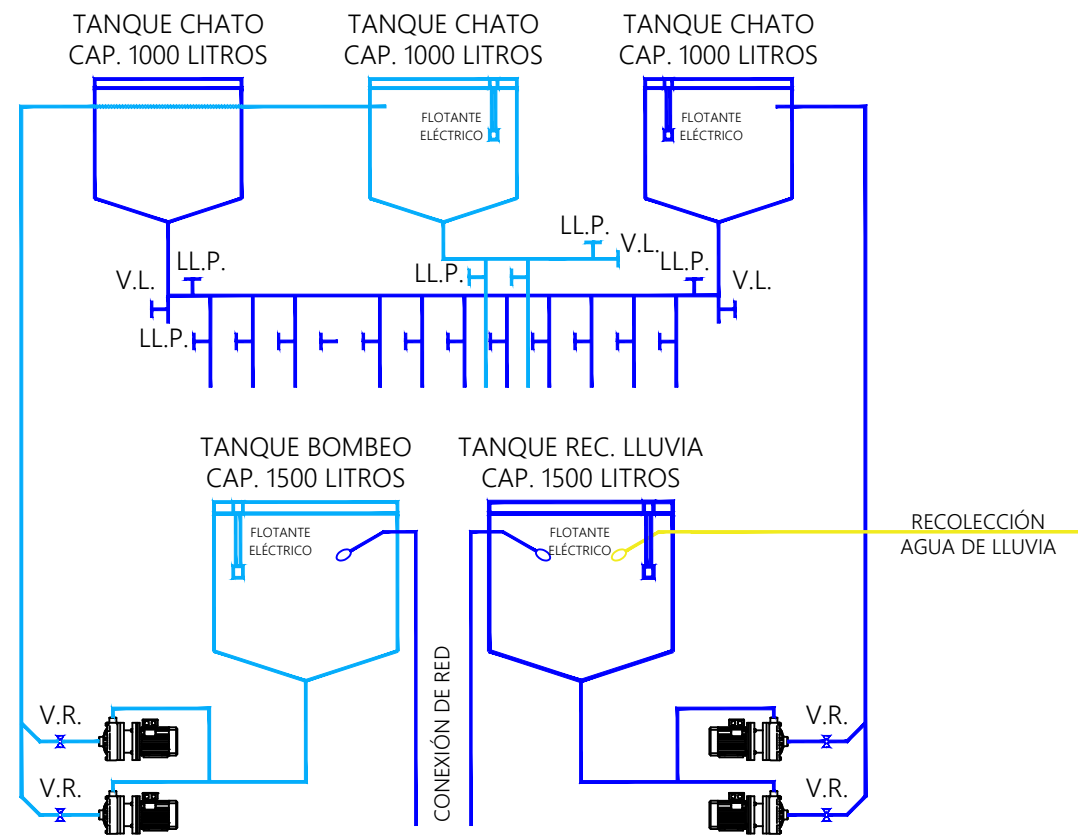

NOTAS

|   |                       |                                    |                               |   |          |                                                                                       |  |
|---|-----------------------|------------------------------------|-------------------------------|---|----------|---------------------------------------------------------------------------------------|--|
| NOTAS   |                       |                                    |                               | LA PRESENTE DOCUMENTACIÓN ES INDICATIVA. EL CONTRATISTA EJECUTARÁ LA DOCUMENTACIÓN CONSTRUCTIVA DE LA OBRA, GENERAL Y DE DETALLE, LA CUAL DEBERÁ SER APROBADA POR LA DIRECCIÓN GENERAL DE ÁREAS DE CONSERVACIÓN Y RESTAURACIÓN AMBIENTAL. TODAS LAS MEDIDAS Y NIVELES SERÁN VERIFICADAS EN OBRA. |          |                                                                                       |  |
| <b>GOBIERNO DE LA CIUDAD DE BUENOS AIRES</b><br>SUBSECRETARÍA DE AMBIENTE<br>DIRECCION GENERAL DE AREAS DE CONSERVACION Y RESTAURACION AMBIENTAL |                       |                                    |                               | <b>GERENCIA OPERATIVA DE INFRAESTRUCTURA</b>   |          |  |  |
| OBRA   |                       | RESERVA ECOLÓGICA COSTANERA SUR    |                               | DIBUJO   |          |                                                                                       |  |
| PLANO   |                       | <b>INSTALACIÓN SANITARIA +2,70</b> |                               | REVISO   |          |                                                                                       |  |
|   |                       |                                    |                               | APROBO   |          |                                                                                       |  |
| ARCHIVO   | RECS - BAÑOS VIAMONTE | EXPTE. Nº                          | 1F-2025-21464165-GCABA-DGACRA |   |          |                                                                                       |  |
| ESCALA   |                       | FECHA                              | ENERO 2025                    |   | Nº PLANO | <b>RECS_BV_SAN_2.2</b>                                                                |  |

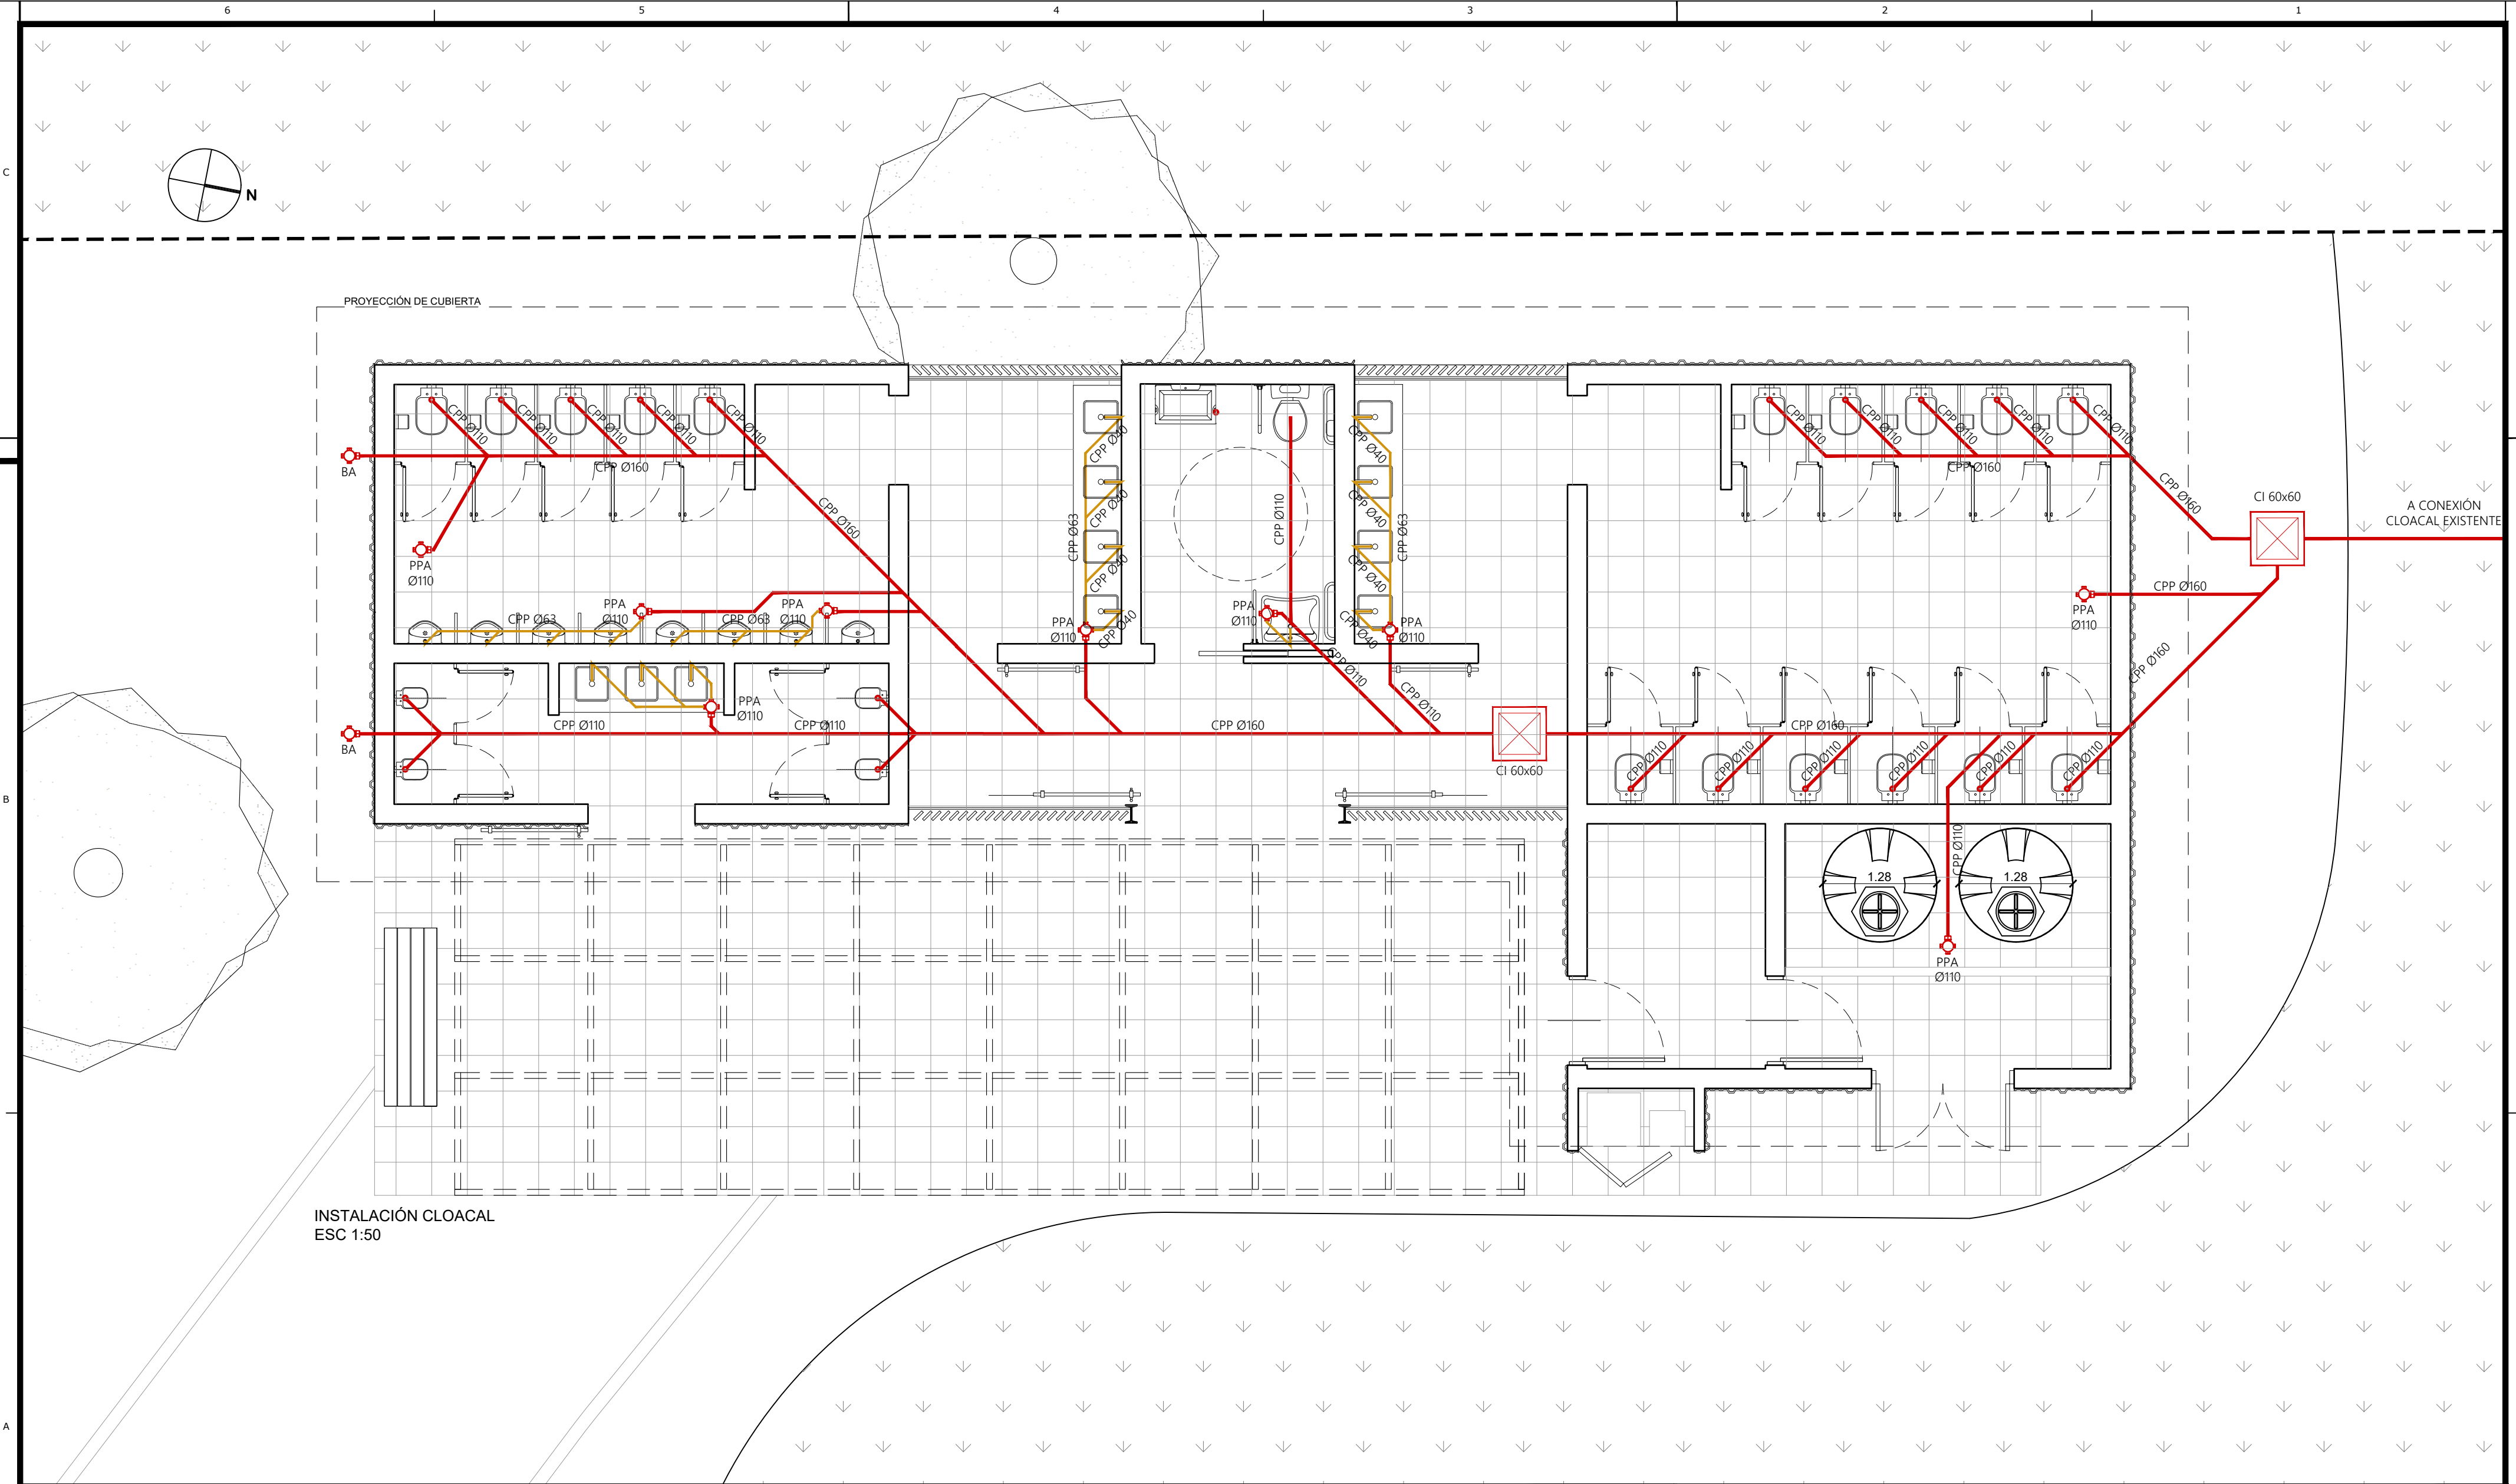

NOTAS

NOTAS

LA PRESENTE DOCUMENTACIÓN ES INDICATIVA. EL CONTRATISTA EJECUTARÁ LA DOCUMENTACIÓN CONSTRUCTIVA DE LA OBRA, GENERAL Y DE DETALLE, LA CUAL DEBERÁ SER APROBADA POR LA DIRECCIÓN GENERAL DE ÁREAS DE CONSERVACIÓN Y RESTAURACIÓN AMBIENTAL. TODAS LAS MEDIDAS Y NIVELES SERÁN VERIFICADAS EN OBRA.

**GOBIERNO DE LA CIUDAD DE BUENOS AIRES**  
SUBSECRETARÍA DE AMBIENTE  
DIRECCIÓN GENERAL DE ÁREAS DE CONSERVACIÓN Y  
RESTAURACIÓN AMBIENTAL

GERENCIA OPERATIVA DE  
INFRAESTRUCTURA



OBRA RESERVA ECOLÓGICA COSTANERA SUR

DIBUJO

PLANO

**INSTALACIÓN CLOACAL**

REVISO

ARCHIVO

RECS - BAÑOS VIAMONTE

EXPTE. Nº

1F-2025-21464165-GCABA-DGACRA

ESCALA


FECHA

OCTUBRE 2024

APROBO


Nº PLANO

**RECS\_BV\_CLO\_2.3**

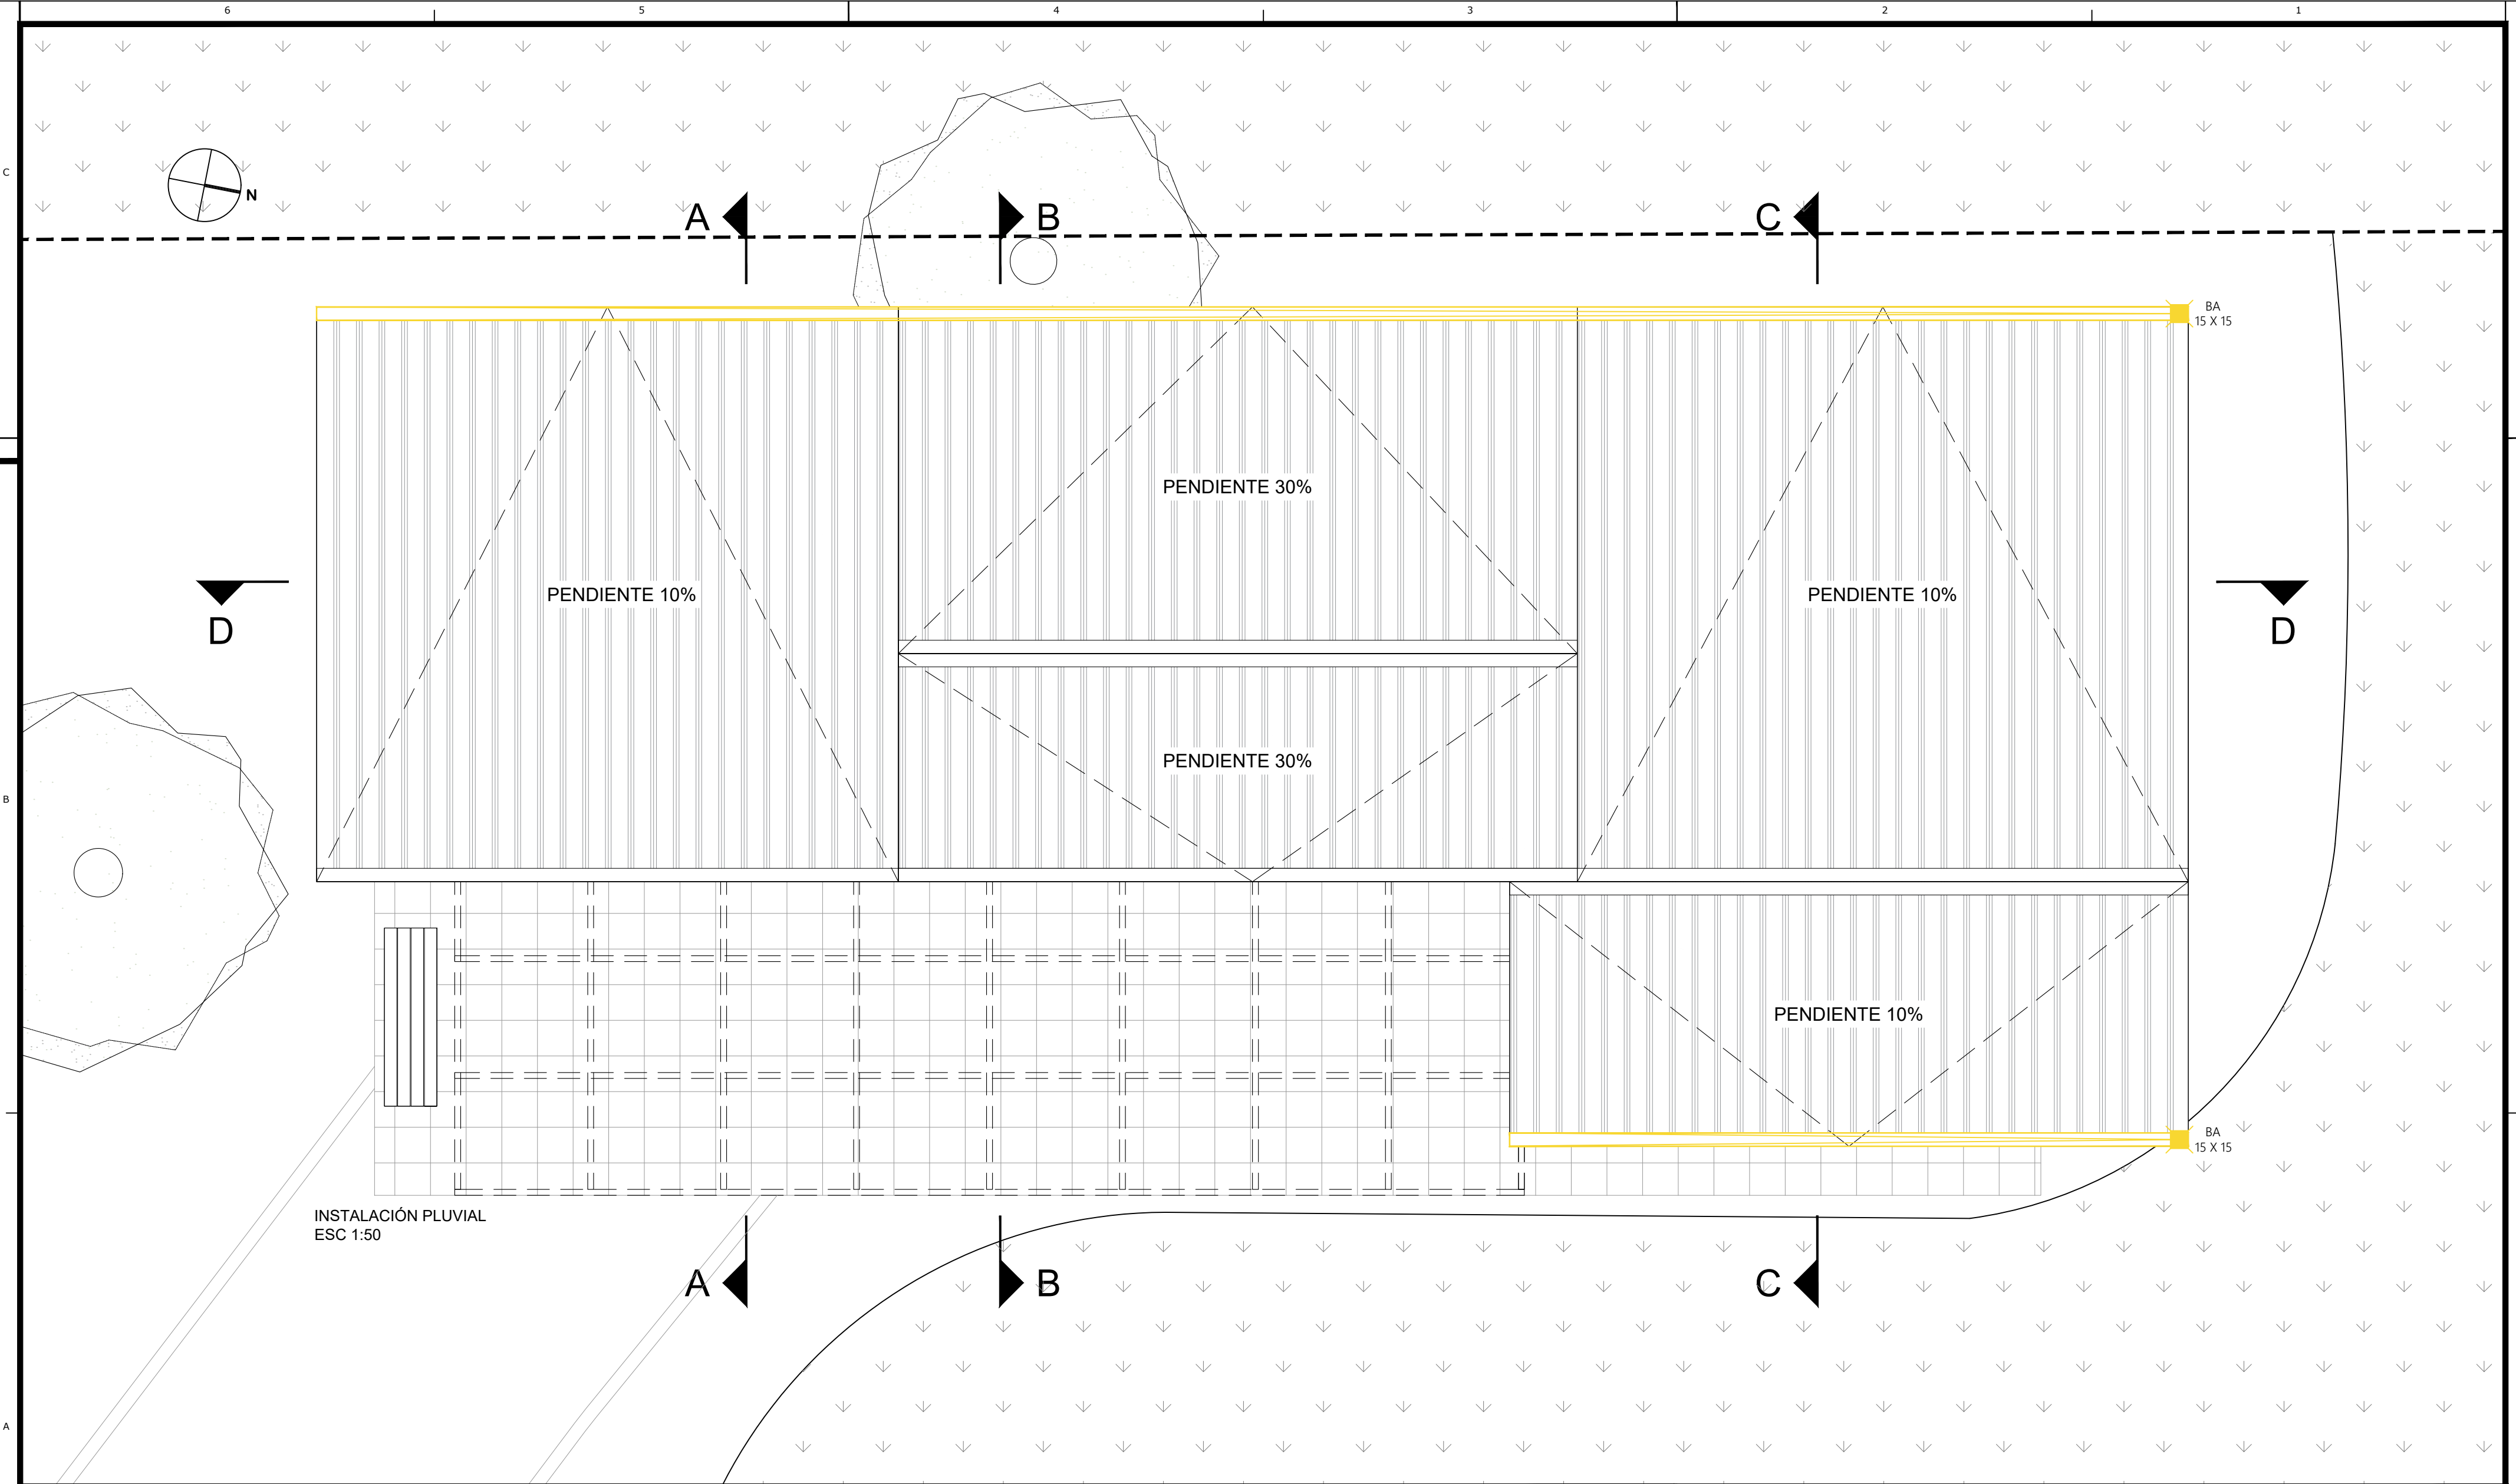

NOTAS

|   |  |                                 |  |   |  |                               |  |
|---|--|---------------------------------|--|---|--|-------------------------------|--|
| NOTAS   |  |                                 |  | LA PRESENTE DOCUMENTACIÓN ES INDICATIVA. EL CONTRATISTA EJECUTARÁ LA DOCUMENTACIÓN CONSTRUCTIVA DE LA OBRA, GENERAL Y DE DETALLE, LA CUAL DEBERÁ SER APROBADA POR LA DIRECCIÓN GENERAL DE ÁREAS DE CONSERVACIÓN Y RESTAURACIÓN AMBIENTAL. TODAS LAS MEDIDAS Y NIVELES SERÁN VERIFICADAS EN OBRA. |  |                               |  |
| GOBIERNO DE LA CIUDAD DE BUENOS AIRES<br>SUBSECRETARIA DE AMBIENTE<br>DIRECCION GENERAL DE AREAS DE CONSERVACION Y RESTAURACION AMBIENTAL |  |                                 |  | GERENCIA OPERATIVA DE INFRAESTRUCTURA   |  |                               |  |
| OBRA   |  | RESERVA ECOLÓGICA COSTANERA SUR |  | DIBUJO   |  |                               |  |
| PLANO   |  | INSTALACIÓN PLUVIAL             |  | REVISO   |  |                               |  |
| ARCHIVO   |  | RECS - BAÑOS VIAMONTE           |  | EXPTE. Nº   |  | 1F-2025-21464165-GCABA-DGACRA |  |
| ESCALA   |  |                                 |  | FECHA   |  | ENERO 2025                    |  |
|   |  |                                 |  | Nº PLANO   |  | RECS_BV_PLU_2.4               |  |

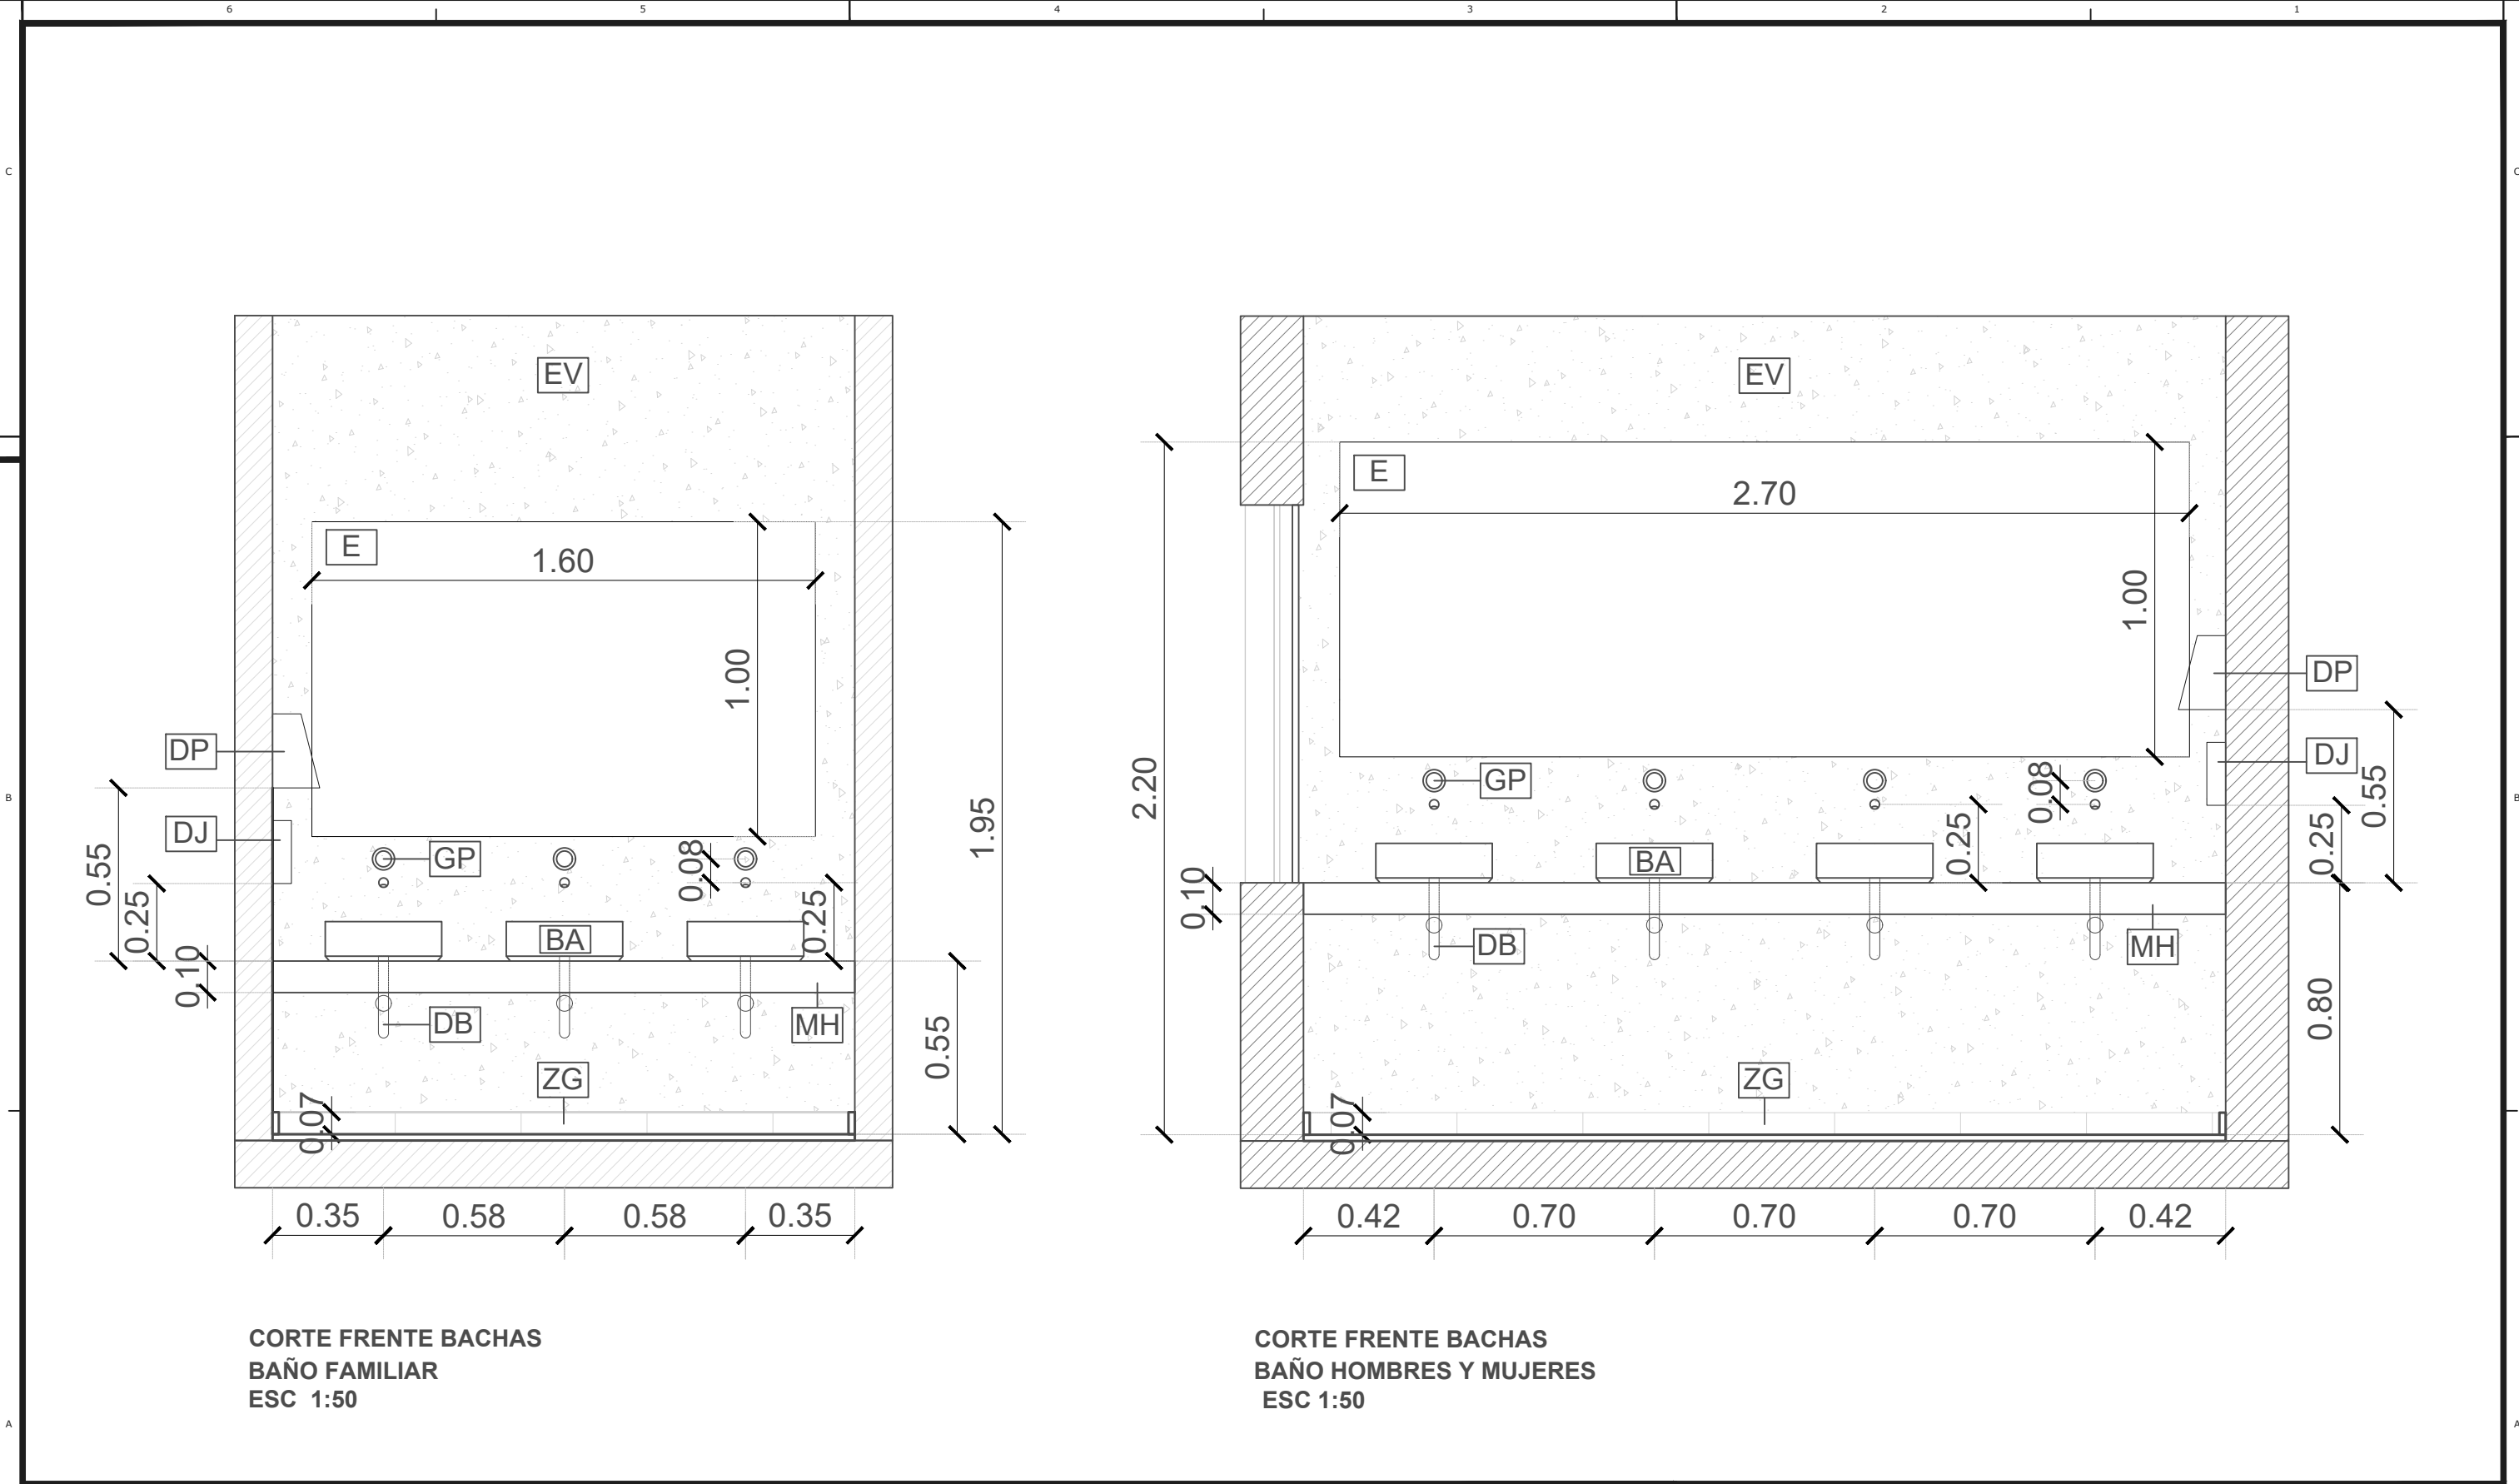

CORTE FRENTE BACHAS  
BAÑO FAMILIAR  
ESC 1:50

CORTE FRENTE BACHAS  
BAÑO HOMBRES Y MUJERES  
ESC 1:50

REFERENCIAS

- [MH]

MESADA H°A° CON TRAFORO Ø5CM CENTRADO EN DESAGÜE DE BACHA
- [BA]

BACHA DE APOYAR 0.38 X 0.38 X 0.12
- [GP]

GRIFERÍA DE PARED P/ BACHA ANTIVANDÁLICA - PULSADOR Y CANILLA INDEPENDIENTES
- [DB]

CAÑERÍA DESCARGA BACHA - CROMADA CON SIFÓN
- [E]

ESPEJO FLOAT 6 MM
- [DJ]


DISPENSER DE JABÓN LÍQUIDO 900 ML
- [DP]

DISPENSER DE PAPEL HIGIENICO 500 PAPELES
- [ZG]


ZÓCALO GRANÍTICO 0.40 X 0.07
- [EV]

ESTUCO VENECIANO

|                                                                     |  |   |  |                                       |                     |
|---------------------------------------------------------------------|--|---|--|---------------------------------------|---------------------|
| NOTAS                                                               |  | LA PRESENTE DOCUMENTACIÓN ES INDICATIVA. EL CONTRATISTA EJECUTARÁ LA DOCUMENTACIÓN CONSTRUCTIVA DE LA OBRA, GENERAL Y DE DETALLE, LA CUAL DEBERÁ SER APROBADA POR LA DIRECCIÓN GENERAL DE ÁREAS DE CONSERVACIÓN Y RESTAURACIÓN AMBIENTAL. TODAS LAS MEDIDAS Y NIVELES SERÁN VERIFICADAS EN OBRA. |  |                                       |                     |
| GOBIERNO DE LA CIUDAD DE BUENOS AIRES                               |  | SUBSECRETARÍA DE AMBIENTE   |  | GERENCIA OPERATIVA DE INFRAESTRUCTURA |                     |
| DIRECCIÓN GENERAL DE ÁREAS DE CONSERVACIÓN Y RESTAURACIÓN AMBIENTAL |  | TEL: 2025-21464165   |  | GCABA-DGACRA                          |                     |
| OBRA                                                                |  | RESERVA ECOLÓGICA COSTANERA SUR   |  | DIBUJO                                |                     |
| PLANO                                                               |  | DETALLES BAÑO FAMILIAR Y ANTEBAÑO   |  | REVISO                                |                     |
| ARCHIVO                                                             |  | RECS - BAÑOS VIAMONTE   |  | APROBO                                |                     |
| ESCALA                                                              |  | EXPTE. Nº   |  | Nº PLANO                              | RECS_BV_DET_SAN_3.0 |
|                                                                     |  | FECHA   |  | Página 13 de 27                       |                     |
|                                                                     |  |   |  | ENERO 2025                            |                     |

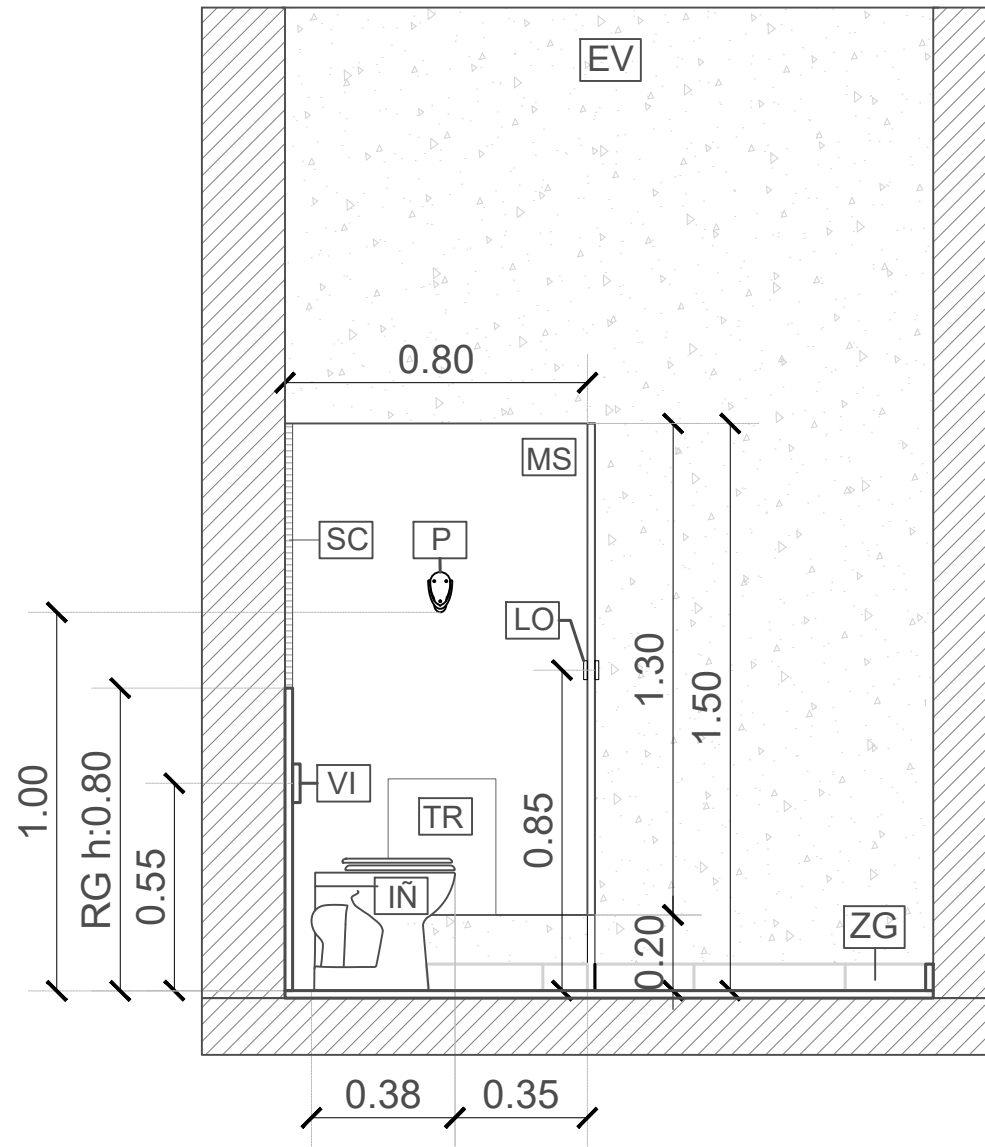

CORTE INODOROS  
BAÑO FAMILIAR  
ESC 1:50

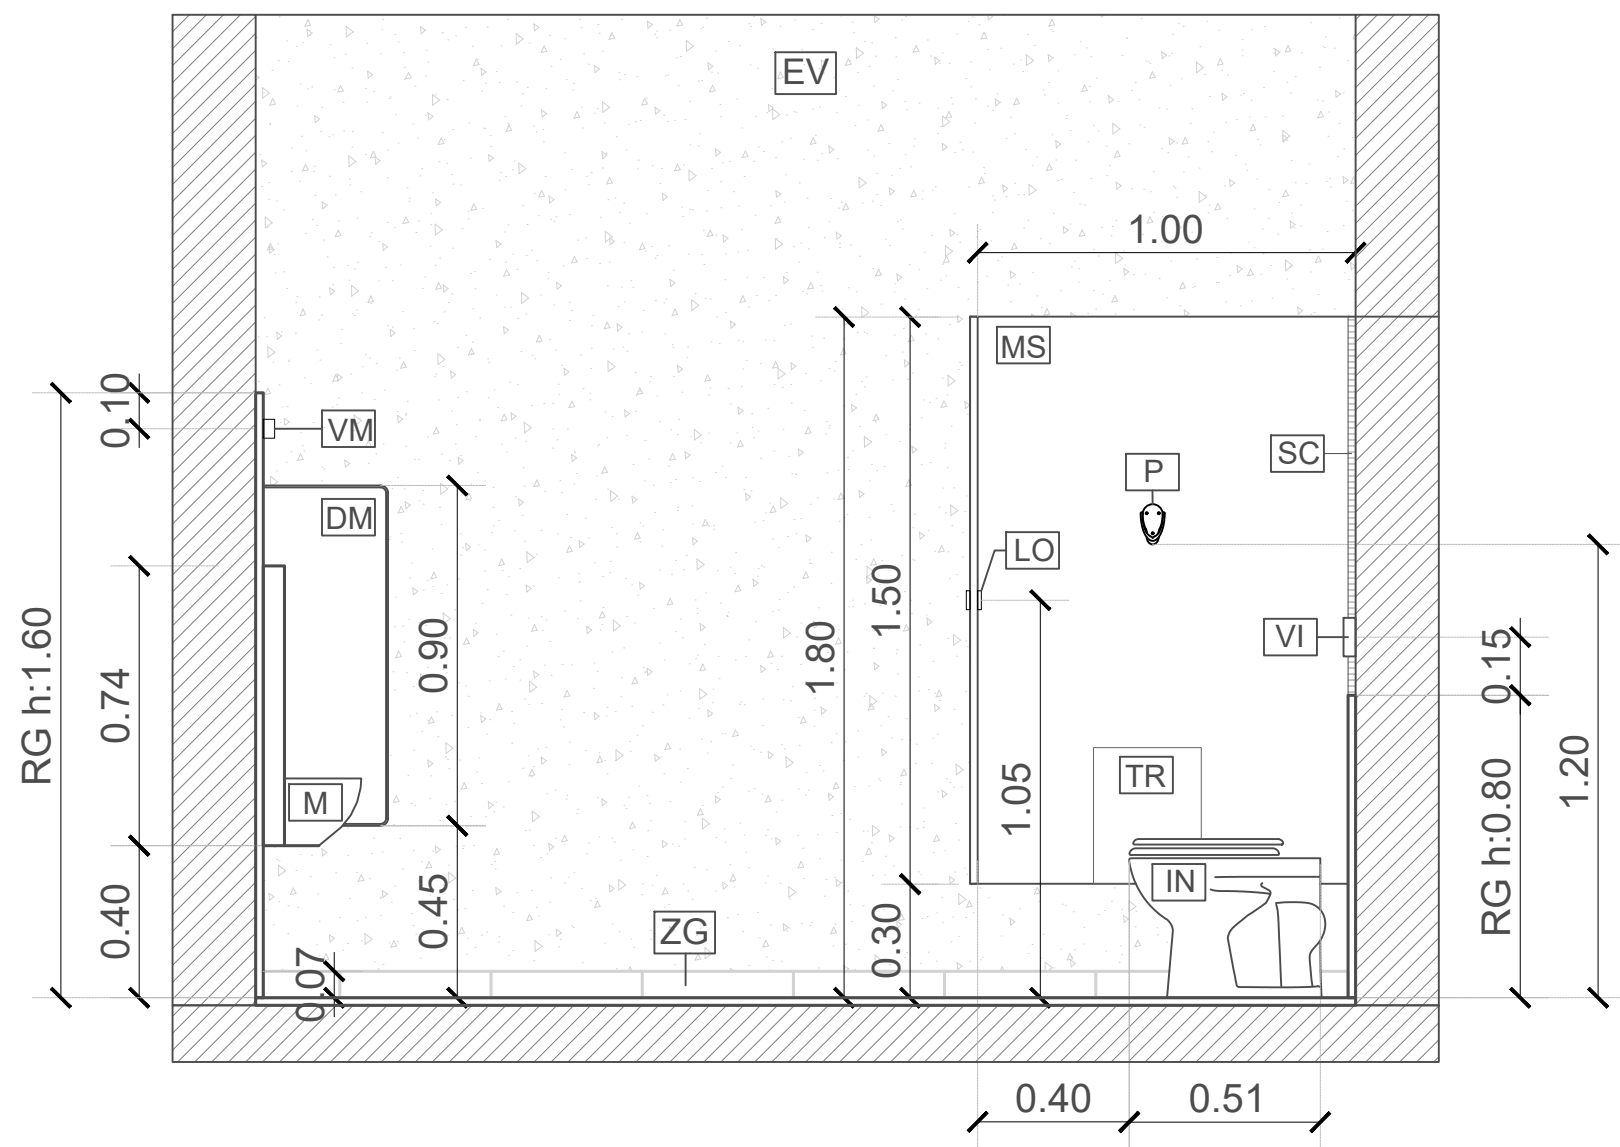


CORTE INODOROS  
BAÑO HOMBRES  
ESC 1:50

REFERENCIAS

|           |                                             |           |                                                                                      |
|-----------|---------------------------------------------|-----------|--------------------------------------------------------------------------------------|
| <b>IN</b> | INODORO CORTO                               | <b>MS</b> | MAMPARAS DIVISORIAS PARA SANITARIOS DE MELAMINA 18 MM OLMO FINLANDES - LINEA NORDICA |
| <b>IN</b> | INODORO PARA NIÑOS                          | <b>MM</b> | MAMPARAS DIVISORIAS PARA MINGITORIO DE MELAMINA 18 MM OLMO FINLANDES - LINEA NORDICA |
| <b>M</b>  | MINGITORIO MURAL - ANTIVÁNDALICO            | <b>SC</b> | SUPLEMENTO CIERRE VARILLA ALUMINIO - CUBRIMIENTO ESPESOR REVESTIMIENTO               |
| <b>VI</b> | VALVULAS PARA INODORO - ANTIVANDALICAS      | <b>RG</b> | REVESTIMIENTO GRANÍTICO 0.40 X 0.40                                                  |
| <b>VM</b> | VALVULAS PARA MINGITORIO - ANTIVANDALICAS   | <b>ZG</b> | ZÓCALO GRANÍTICO 0.40 X 0.07                                                         |
| <b>TR</b> | TACHO DE RESIDUO 14 LTS DE ACERO INOXIDABLE | <b>EV</b> | ESTUCO VENECIANO                                                                     |
| <b>P</b>  | PERCHERO ZINC CROMADO HASTA 10 KG           | <b>LO</b> | TRABA LIBRE / OCUPADO                                                                |

|                                       |  |   |  |
|---------------------------------------|--|---|--|
| NOTAS                                 |  | LA PRESENTE DOCUMENTACIÓN ES INDICATIVA. EL CONTRATISTA EJECUTARÁ LA DOCUMENTACIÓN CONSTRUCTIVA DE LA OBRA, GENERAL Y DE DETALLE, LA CUAL DEBERÁ SER APROBADA POR LA DIRECCIÓN GENERAL DE ÁREAS DE CONSERVACIÓN Y RESTAURACIÓN AMBIENTAL. TODAS LAS MEDIDAS Y NIVELES SERÁN VERIFICADAS EN OBRA. |  |
| GOBIERNO DE LA CIUDAD DE BUENOS AIRES |  | GERENCIA OPERATIVA DE INFRAESTRUCTURA   |  |
| SUBSECRETARÍA DE AMBIENTE             |  | DIRECCIÓN GENERAL DE ÁREAS DE CONSERVACIÓN Y RESTAURACIÓN AMBIENTAL   |  |
| OBRA                                  |  | RESERVA ECOLÓGICA COSTANERA SUR   |  |
| PLANO                                 |  | DETALLE BAÑO FAMILIAR Y BAÑO HOMBRES   |  |
| ARCHIVO                               |  | RECS - BAÑOS VIAMONTE   |  |
| ESCALA                                |  | Página 14 de 27   |  |
|                                       |  | Nº PLANO   |  |
|                                       |  | RECS_BV_DET_SAN_3.1   |  |

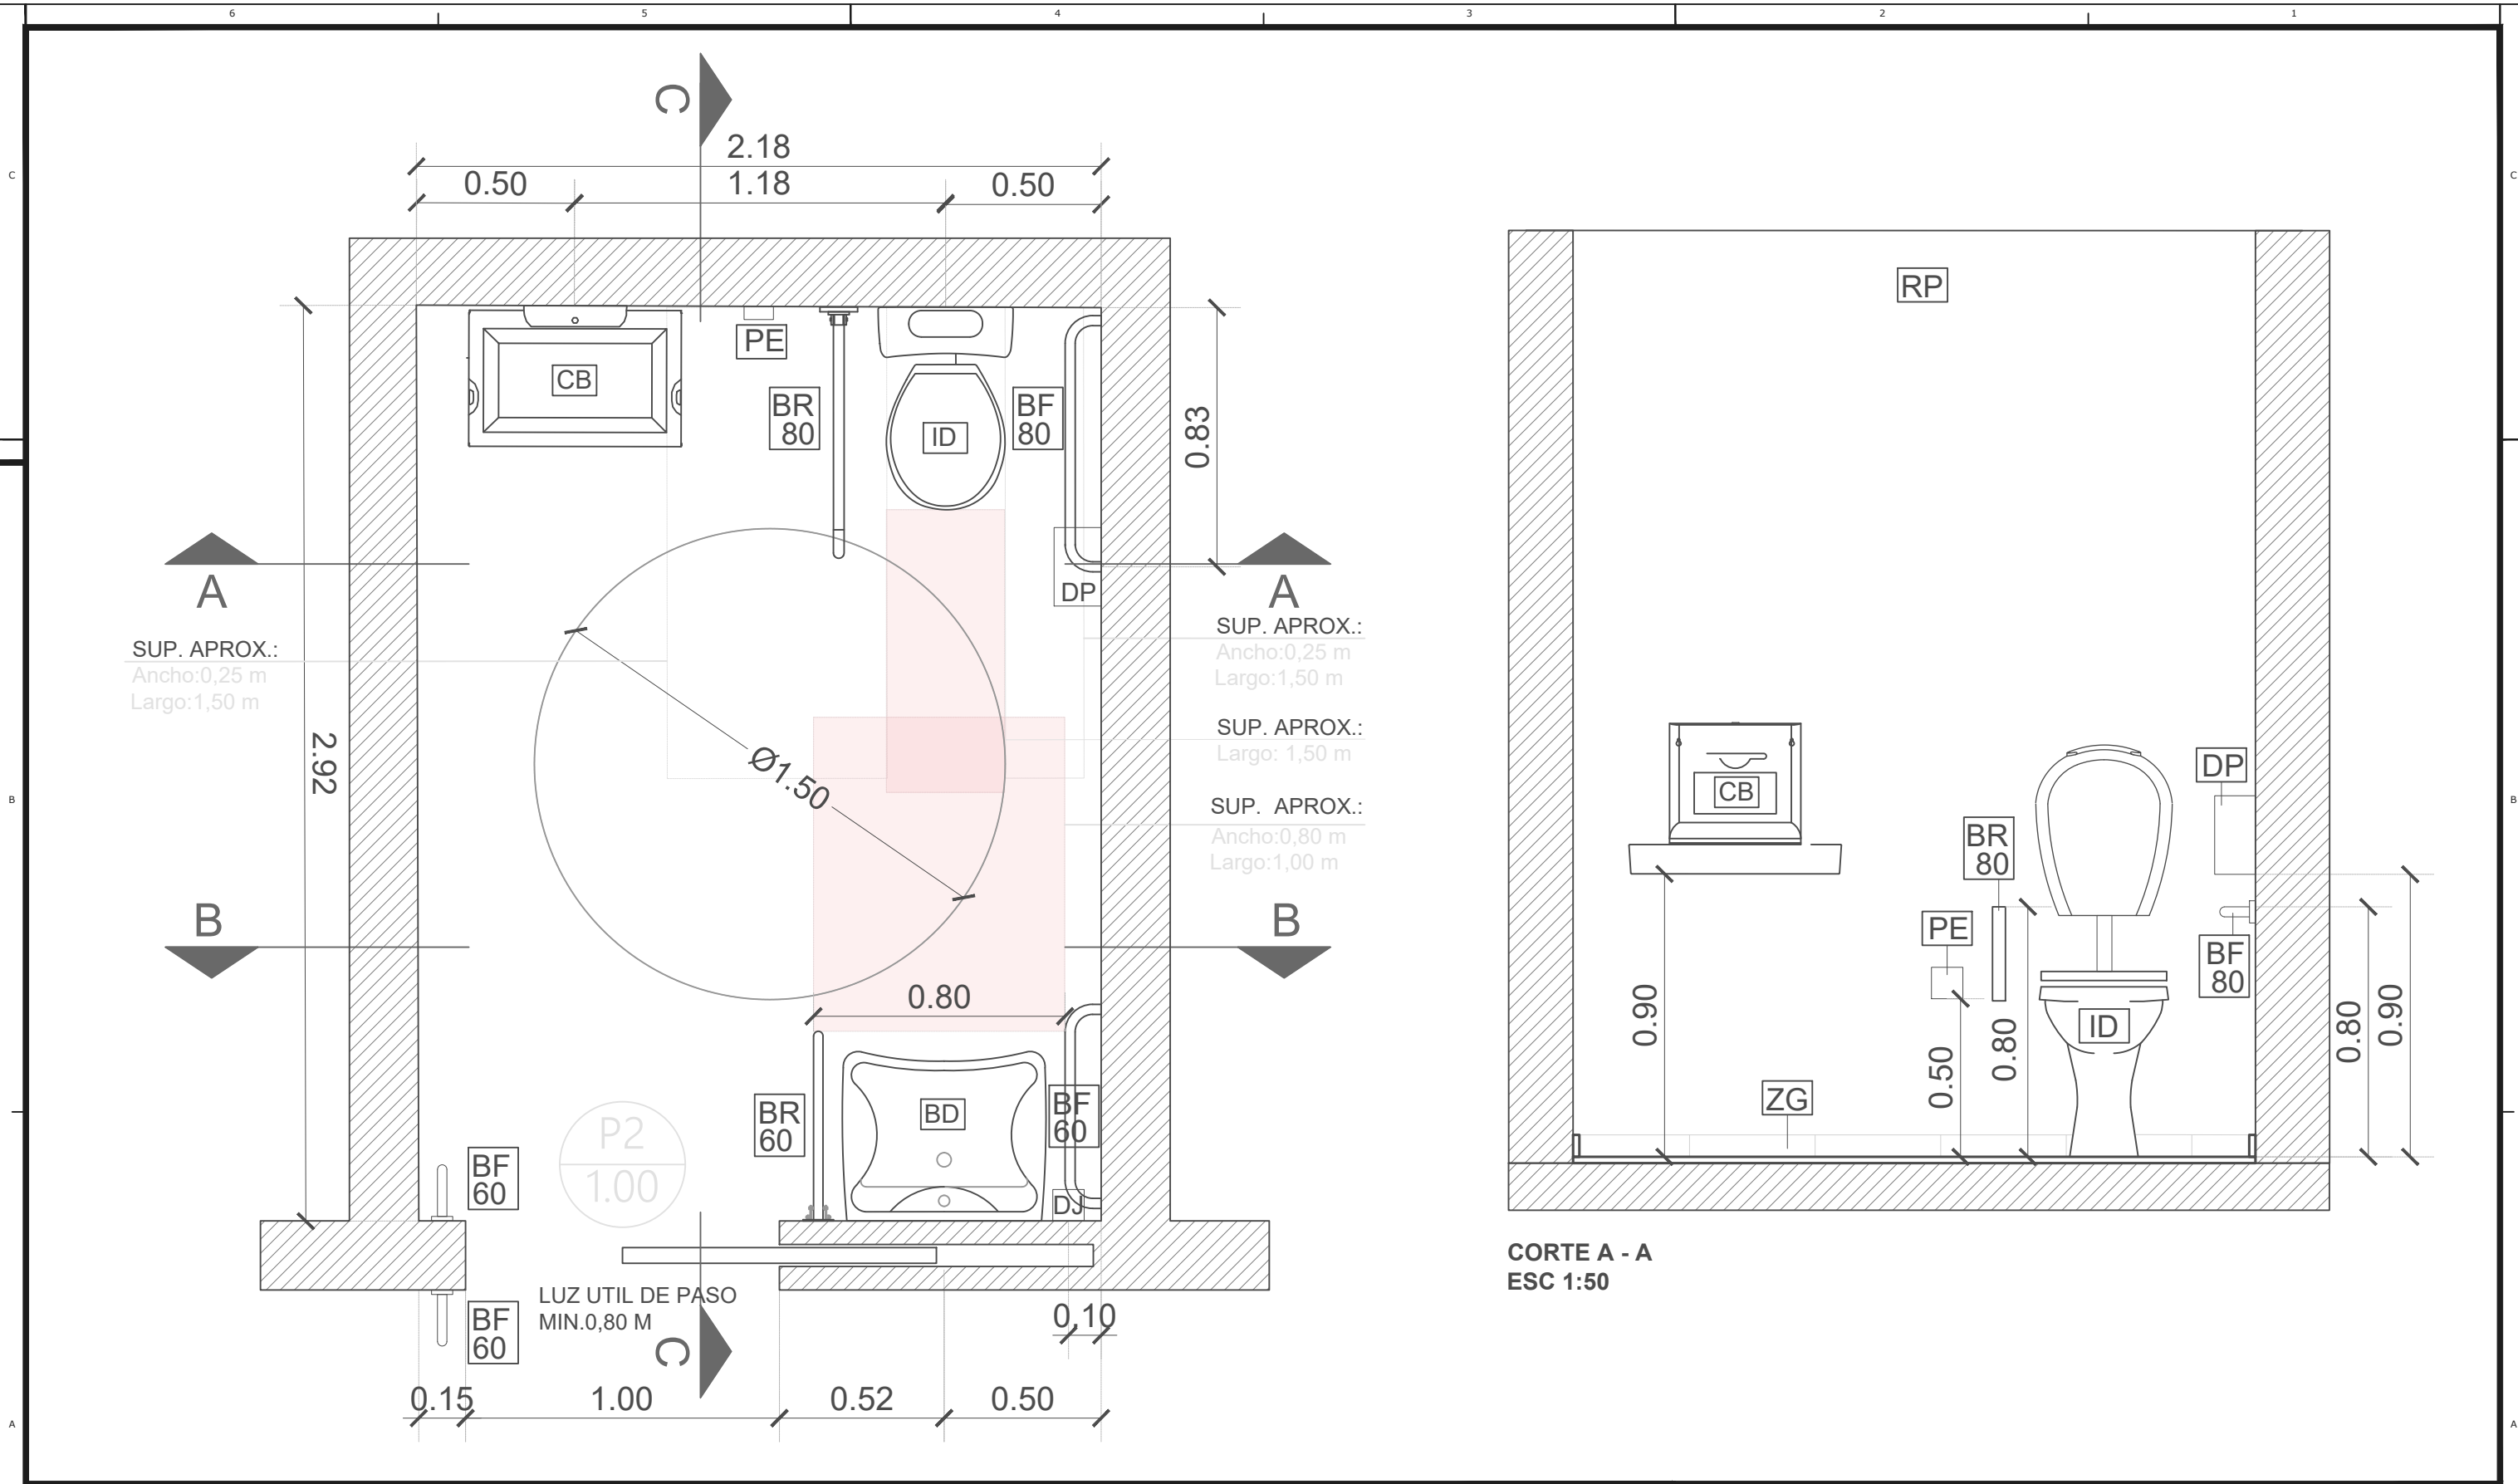


CORTE A - A  
ESC 1:50


REFERENCIAS

- |                                                         |                                                        |                                |
|---------------------------------------------------------|--------------------------------------------------------|--------------------------------|
| [BD] BACHA PARA PERSONAS CON DISCAPACIDAD               | [DJ] DISPENSER DE JABON DE MANOS LIQUIDO               | [BR 60] BARRAL REBATIBLE 60 CM |
| [ID] INODORO CON MOCHILA PARA PERSONAS CON DISCAPACIDAD | [DP] DISPENSER DE PAPEL HIGIENICO 400 ML               | [BR 80] BARRAL REBATIBLE 80 CM |
| [CB] CAMBIADOR DE BEBE                                  | [ED] ESPEJO INCLINADO a 10°                            | [BF 60] BARRAL FIJO 60 CM      |
| [PE] PULSADOR DE EMERGENCIA: ALARMA LUMINICA-SONORA     | [GD] GRIFERIA MONOCOMANDO Y MANGO DE PALANCA A PRESION | [BF 80] BARRAL FIJO 80 CM      |
| [ZG] ZOCALO GRANITICO 0.40 X 0.07                       | [P] PERCHERO ZINC CROMADO HASTA 10 KG                  |                                |
|                                                         | [RP] REVESTIMIENTO PINTURA LATEX                       |                                |

|                                       |  |  |   |  |  |
|---------------------------------------|--|--|---|--|--|
| NOTAS                                 |  |  | LA PRESENTE DOCUMENTACIÓN ES INDICATIVA. EL CONTRATISTA EJECUTARÁ LA DOCUMENTACIÓN CONSTRUCTIVA DE LA OBRA, GENERAL Y DE DETALLE, LA CUAL DEBERÁ SER APROBADA POR LA DIRECCIÓN GENERAL DE ÁREAS DE CONSERVACIÓN Y RESTAURACIÓN AMBIENTAL. TODAS LAS MEDIDAS Y NIVELES SERÁN VERIFICADAS EN OBRA. |  |  |
| GOBIERNO DE LA CIUDAD DE BUENOS AIRES |  |  | GERENCIA OPERATIVA DE INFRAESTRUCTURA   |  |  |
| SUBSECRETARIA DE AMBIENTE             |  |  | DIRECCION GENERAL DE AREAS DE CONSERVACION Y RESTAURACION AMBIENTAL   |  |  |
| OBRA                                  |  |  | RESERVA ECOLOGICA COSTANERA SUR   |  |  |
| PLANO                                 |  |  | DETALLE BAÑO PERSONAS CON DISCAPACIDAD   |  |  |
| ARCHIVO                               |  |  | RECS - BAÑOS VIAMONTE   |  |  |
| ESCALA                                |  |  | ENERO 2025   |  |  |
| EXpte. Nº                             |  |  | Página 15 de 27   |  |  |
| FECHA                                 |  |  | Nº PLANO   |  |  |
|                                       |  |  | RECS_BV_DET_SAN_3.2   |  |  |

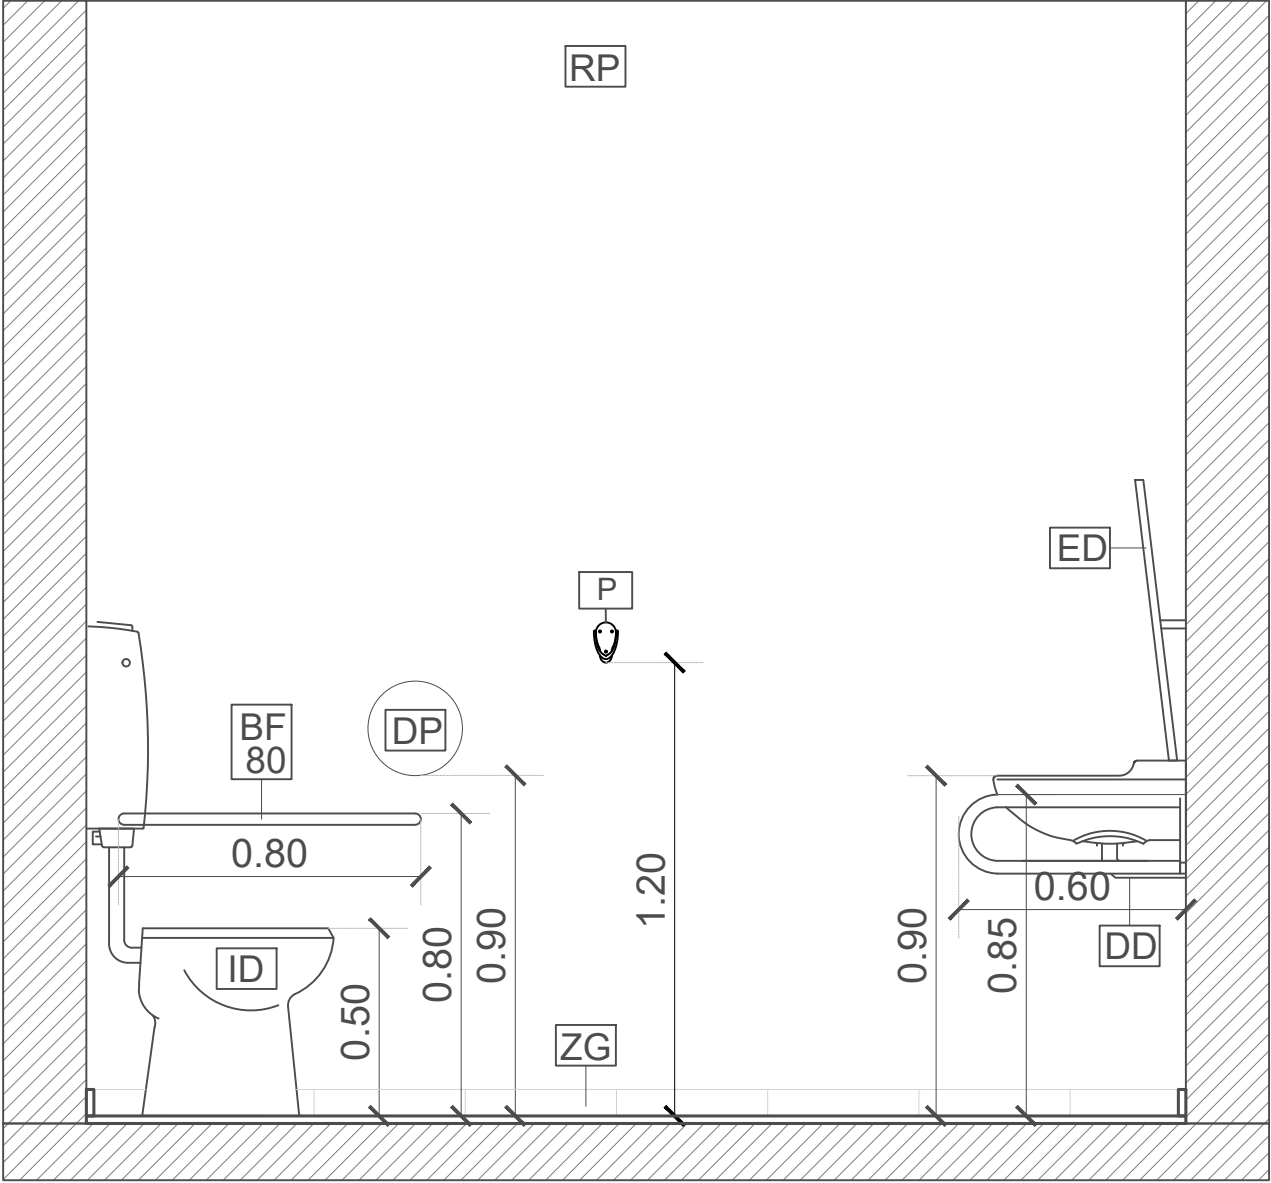

CORTE B - B  
ESC 1:50

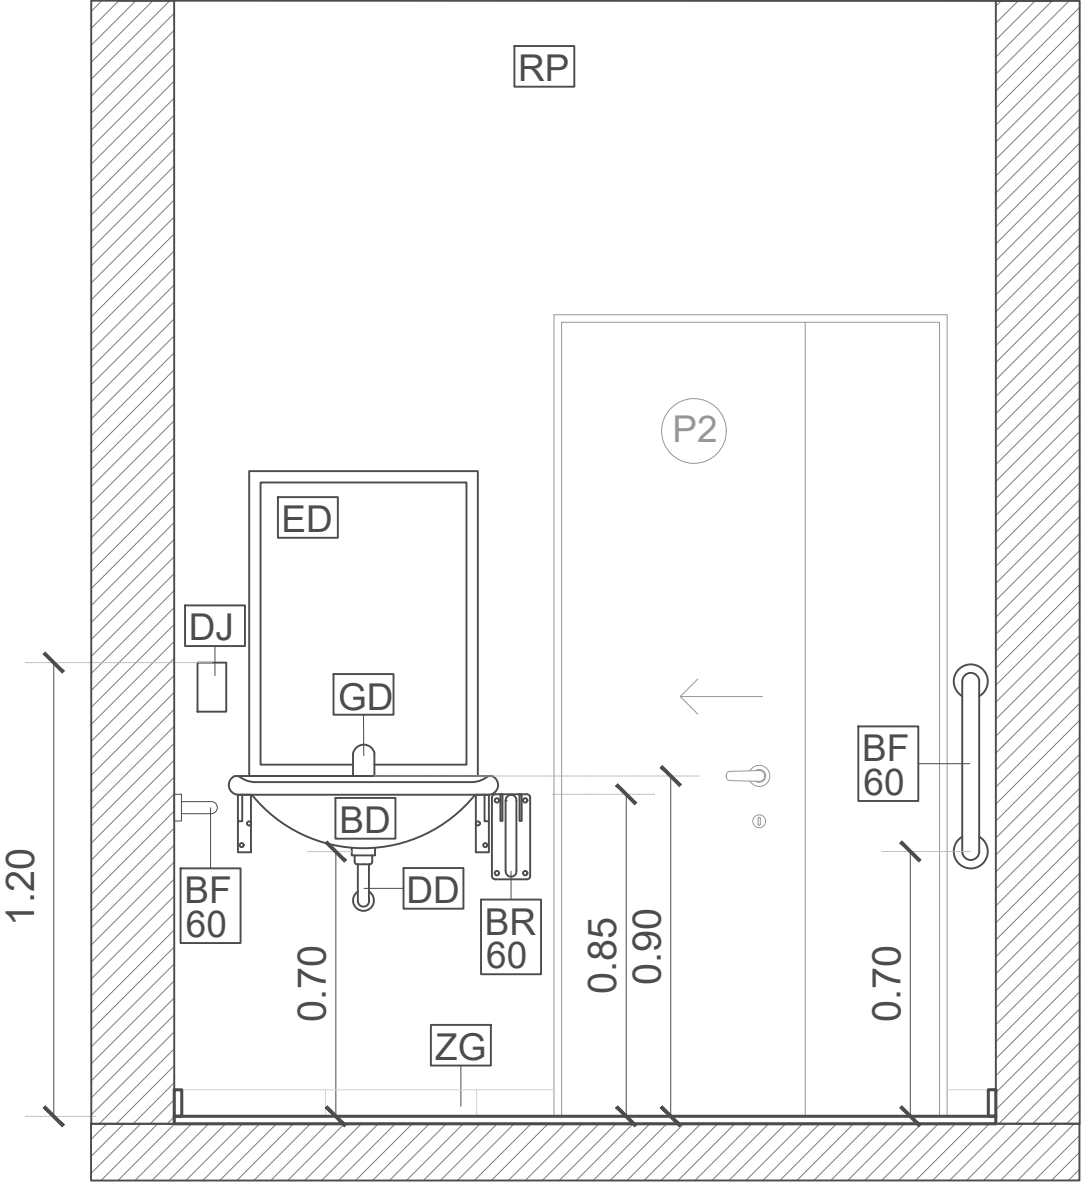

CORTE C - C  
ESC 1:50

NOTAS

REFERENCIAS

BD

BACHA PARA PERSONAS CON DISCAPACIDAD

ID

INODORO CON MOCHILA PARA PERSONAS CON DISCAPACIDAD

CB

CAMBIADOR DE BEBE

PE

PULSADOR DE EMERGENCIA: ALARMA LUMINICA-SONORA

ZG

ZOCALO GRANITICO 0.40 X 0.07

DD

DESAGUE DE ACERO INOXIDABLE

DJ

DISPENSER DE JABON DE MANOS LIQUIDO

DP

DISPENSER DE PAPEL HIGIENICO 400 ML

ED

ESPEJO INCLINADO a 10°

GD

GRIFERIA MONOCOMANDO Y MANGO DE PALANCA A PRESION

P

PERCHERO ZINC CROMADO HASTA 10 KG

RP

REVESTIMIENTO PINTURA LATEX

BR 60

BARRAL REBATIBLE 60 CM

BR 80

BARRAL REBATIBLE 80 CM

BF 60

BARRAL FIJO 60 CM

BF 80

BARRAL FIJO 80 CM

NOTAS

LA PRESENTE DOCUMENTACIÓN ES INDICATIVA. EL CONTRATISTA EJECUTARÁ LA DOCUMENTATCIÓN CONSTRUCTIVA DE LA OBRA, GENERAL Y DE DETALLE, LA CUAL DEBERÁ SER APROBADA POR LA DIRECCIÓN GENERAL DE ÁREAS DE CONSERVACIÓN Y RESTAURACIÓN AMBIENTAL. TODAS LAS MEDIDAS Y NIVELES SERÁN VERIFICADAS EN OBRA.

GOBIERNO DE LA CIUDAD DE BUENOS AIRES

SUBSECRETARIA DE AMBIENTE

DIRECCION GENERAL DE AREAS DE CONSERVACION Y RESTAURACION AMBIENTAL

TEL: 2025-21464165

GCABA-DGACRA

OBRA

RESERVA ECOLÓGICA COSTANERA SUR

DIBUJO

PLANO

DETALLE BAÑO PERSONAS CON DISCAPACIDAD

REVISO

ARCHIVO

RECS - BAÑOS VIAMONTE

EXPT. Nº

ESCALA


FECHA

ENERO 2025


Página 16 de 27

Nº PLANO


RECS\_BV\_DET\_SAN\_3.3

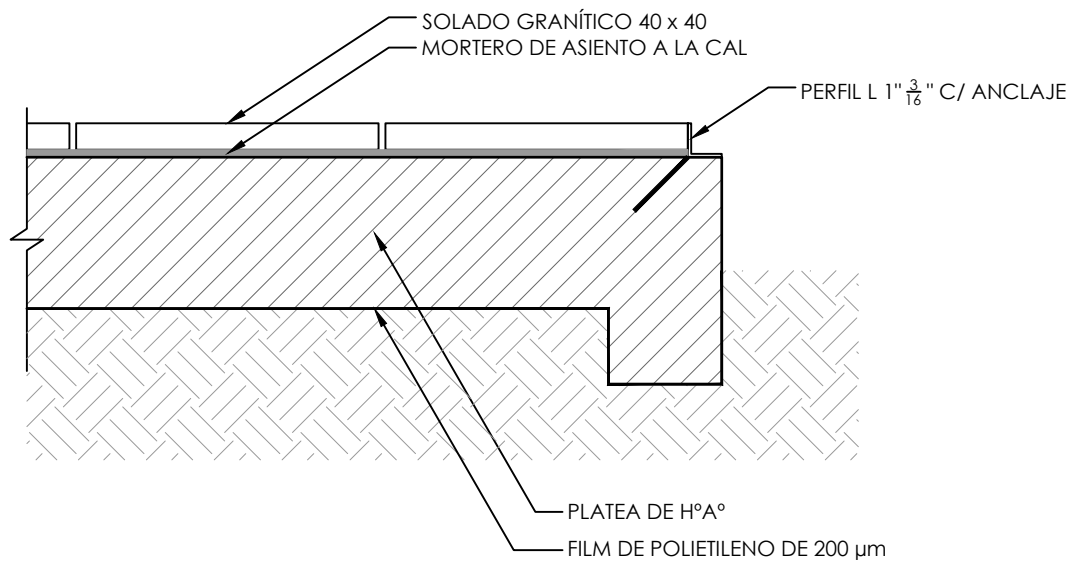


DETALLE PERFIL L DE TERMINACIÓN  
PLATEA DE FUNDACIÓN

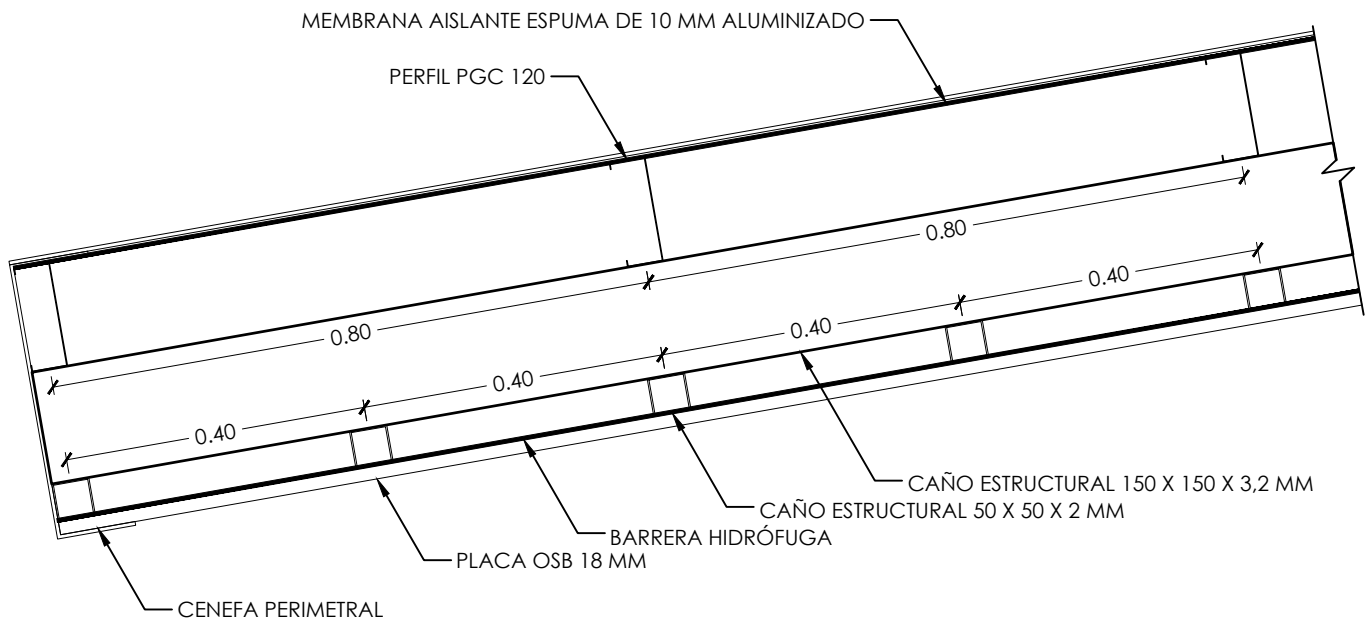

DETALLE CUBIERTA

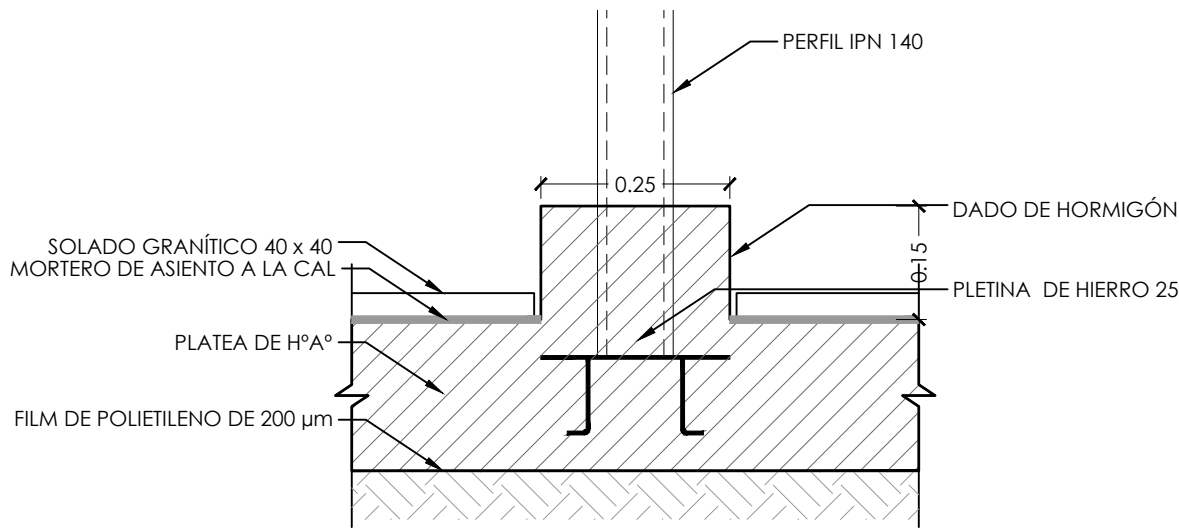


DETALLE FUNDACIÓN PÉRGOLA

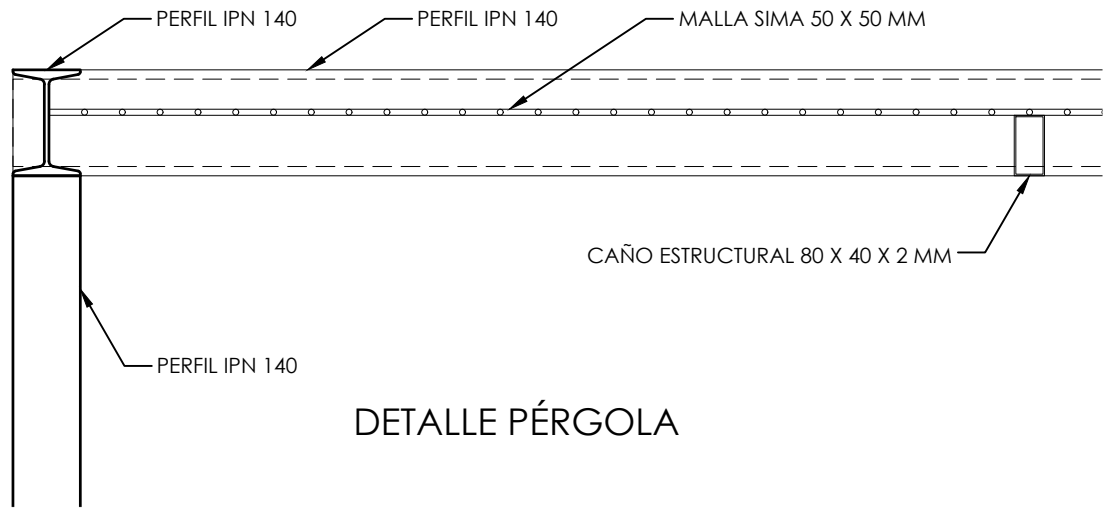

DETALLE PÉRGOLA



NOTAS

|   |                                  |   |            |                                       |                     |
|---|----------------------------------|---|------------|---------------------------------------|---------------------|
| NOTAS   |                                  | LA PRESENTE DOCUMENTACIÓN ES INDICATIVA. EL CONTRATISTA EJECUTARÁ LA DOCUMENTACIÓN CONSTRUCTIVA DE LA OBRA, GENERAL Y DE DETALLE, LA CUAL DEBERÁ SER APROBADA POR LA DIRECCIÓN GENERAL DE ÁREAS DE CONSERVACIÓN Y RESTAURACIÓN AMBIENTAL. TODAS LAS MEDIDAS Y NIVELES SERÁN VERIFICADAS EN OBRA. |            |                                       |                     |
| GOBIERNO DE LA CIUDAD DE BUENOS AIRES<br>SUBSECRETARÍA DE AMBIENTE<br>DIRECCIÓN GENERAL DE ÁREAS DE CONSERVACIÓN Y RESTAURACIÓN AMBIENTAL |                                  |   |            | GERENCIA OPERATIVA DE INFRAESTRUCTURA |                     |
| OBRA   | RESERVA ECOLÓGICA COSTANERA SUR  |   |            | DIBUJO                                |                     |
| PLANO   | DETALLE PLATEA, CUBIERTA PÉRGOLA |   |            | REVISO                                |                     |
| ARCHIVO   | RECS - BAÑOS VIAMONTE            | EXPTE. N°   |            | APROBO                                |                     |
| ESCALA   | 1:10                             | FECHA   | ENERO 2025 | N° PLANO                              | RECS_BV_DET_SAN_3.4 |

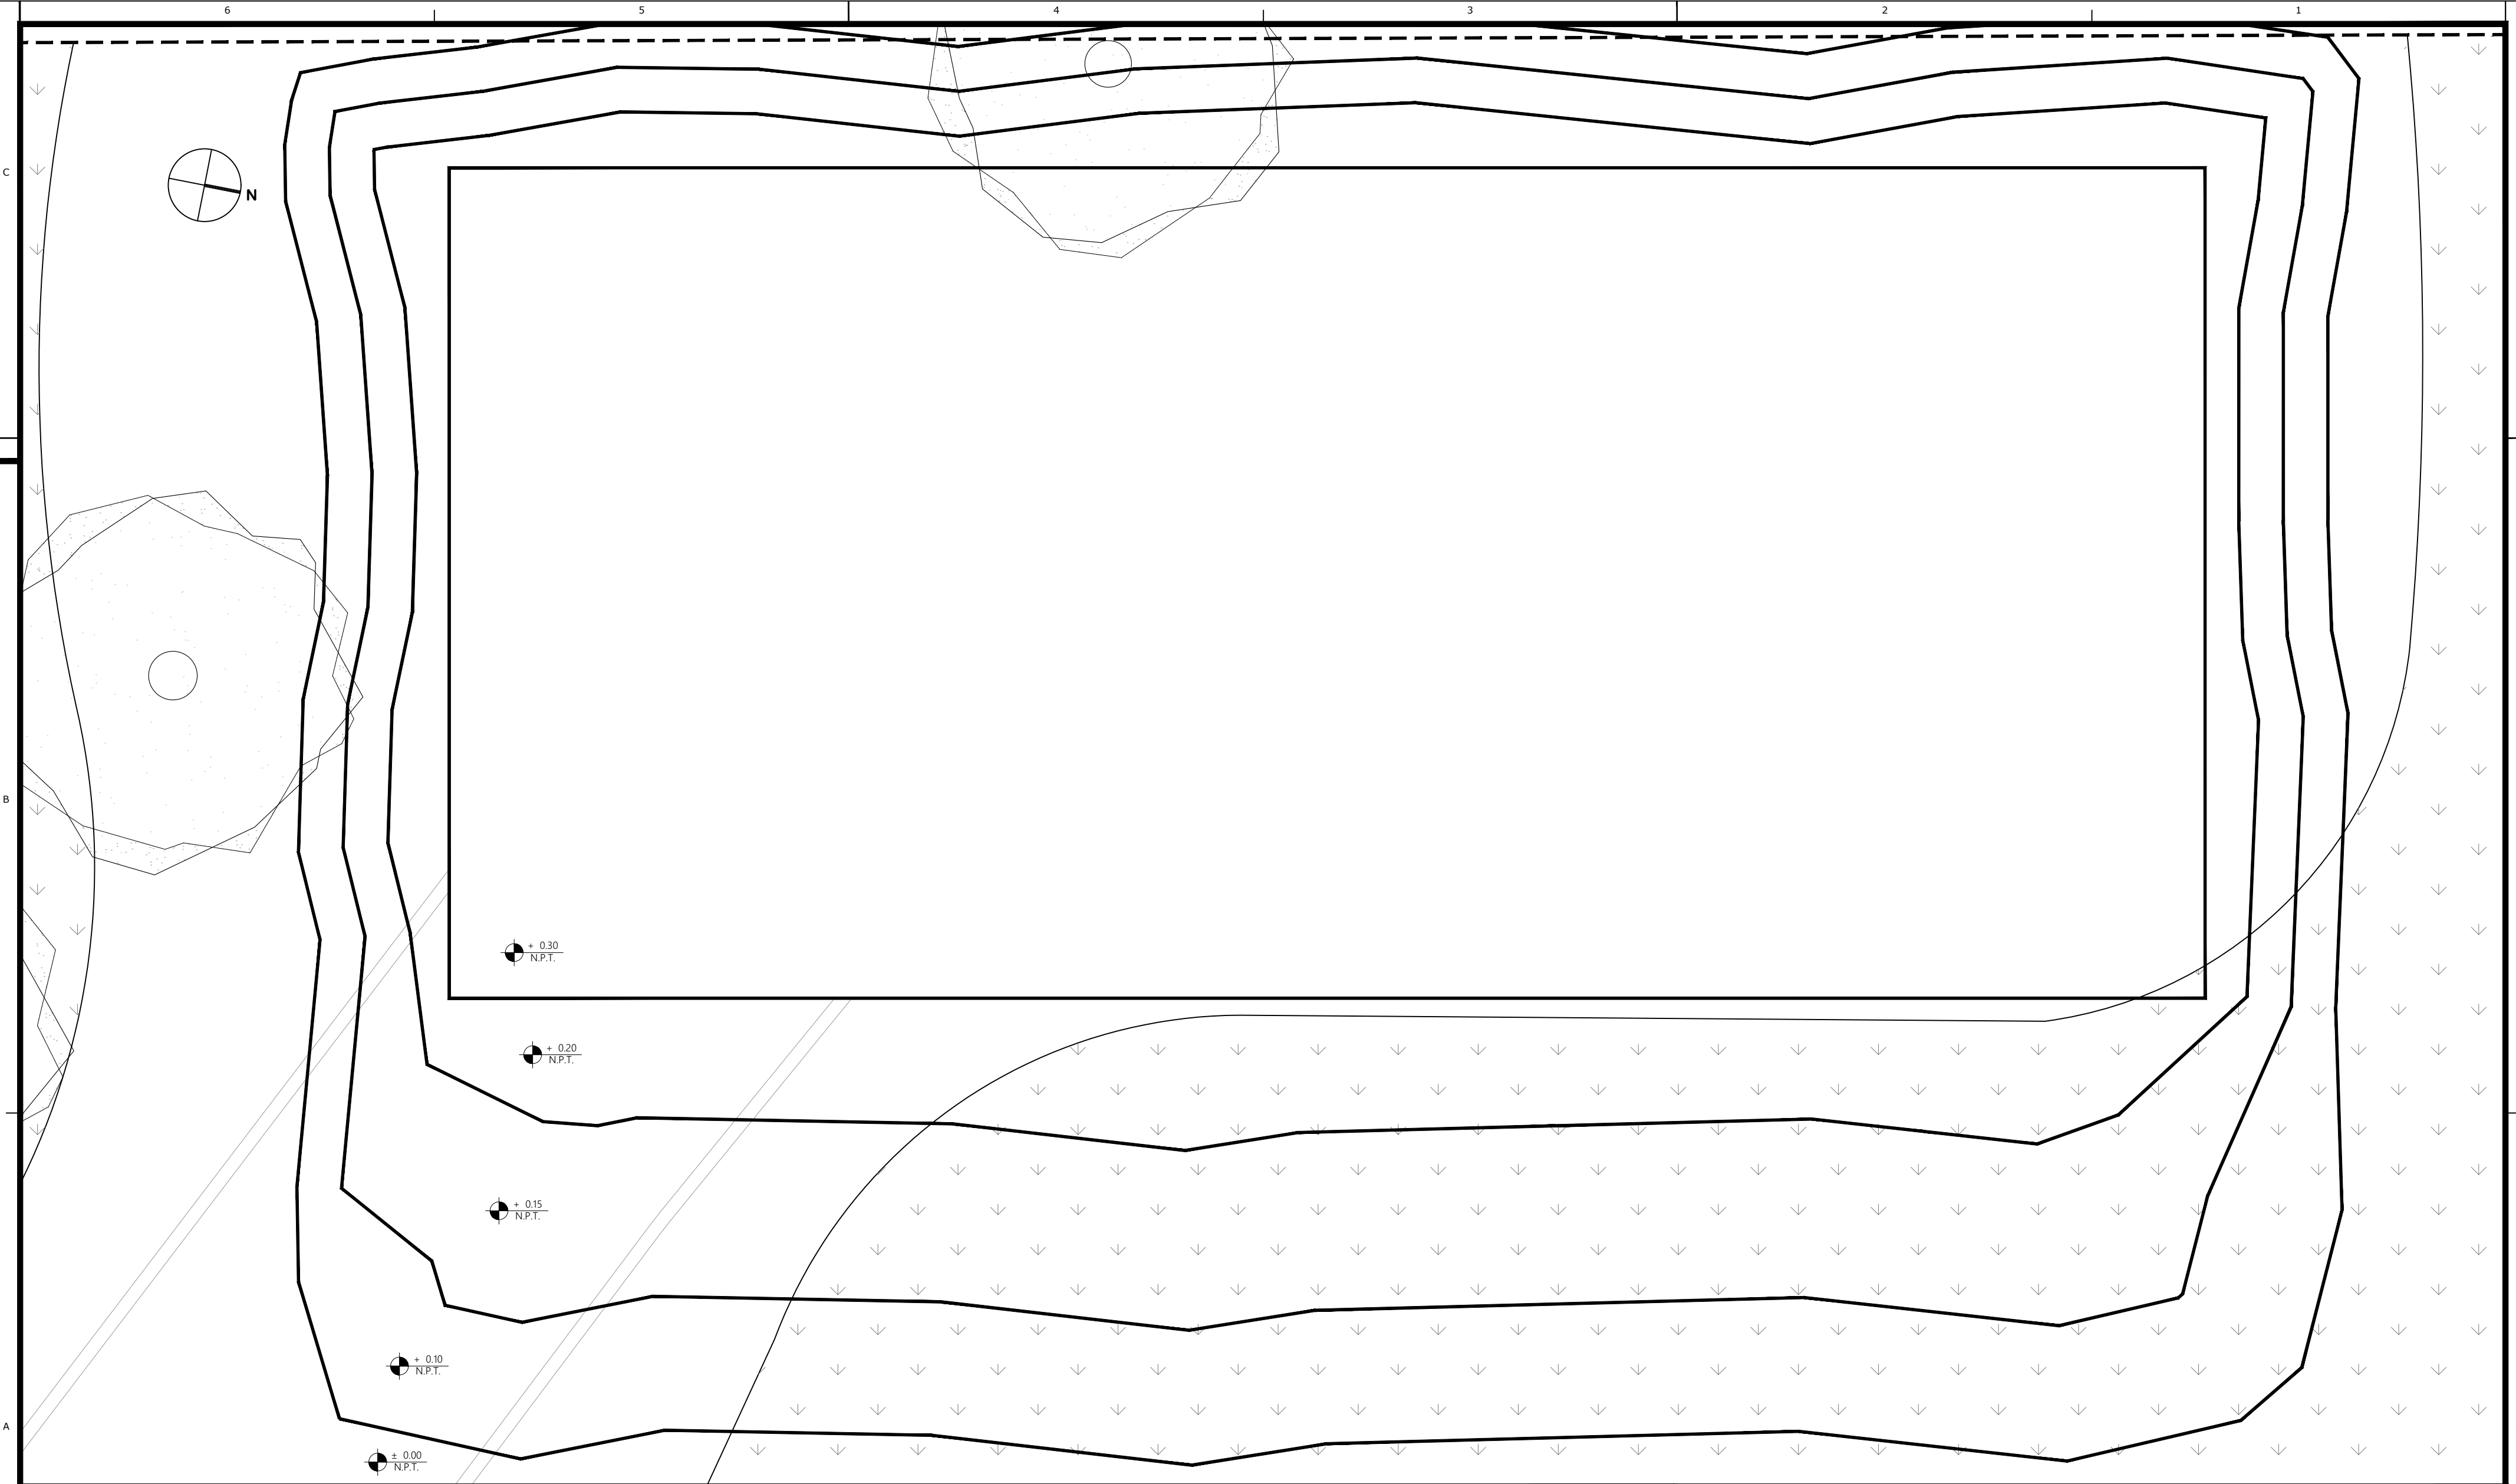

NOTAS


|   |  |                                 |           |   |          |                                                                                       |  |
|---|--|---------------------------------|-----------|---|----------|---------------------------------------------------------------------------------------|--|
| NOTAS   |  |                                 |           | LA PRESENTE DOCUMENTACIÓN ES INDICATIVA. EL CONTRATISTA EJECUTARÁ LA DOCUMENTATCIÓN CONSTRUCTIVA DE LA OBRA, GENERAL Y DE DETALLE, LA CUAL DEBERÁ SER APROBADA POR LA DIRECCIÓN GENERAL DE ÁREAS DE CONSERVACIÓN Y RESTAURACIÓN AMBIENTAL. TODAS LAS MEDIDAS Y NIVELES SERÁN VERIFICADAS EN OBRA. |          |                                                                                       |  |
| GOBIERNO DE LA CIUDAD DE BUENOS AIRES<br>SUBSECRETARIA DE AMBIENTE<br>DIRECCION GENERAL DE AREAS DE CONSERVACION Y RESTAURACION AMBIENTAL |  |                                 |           | GERENCIA OPERATIVA DE INFRAESTRUCTURA   |          |  |  |
| OBRA   |  | RESERVA ECOLÓGICA COSTANERA SUR |           |   | DIBUJO   |                                                                                       |  |
| PLANO   |  | MOVIMIENTO DE SUELOS            |           |   | REVISO   |                                                                                       |  |
| ARCHIVO   |  | RECS - BAÑOS VIAMONTE           | EXpte. Nº | 1F-2025-21464165-GCABA-DGACRA   | APROBO   |                                                                                       |  |
| ESCALA   |  |                                 | FECHA     | ENERO 2025   | Nº PLANO | RECS_BV_MOVSUE_4.0                                                                    |  |

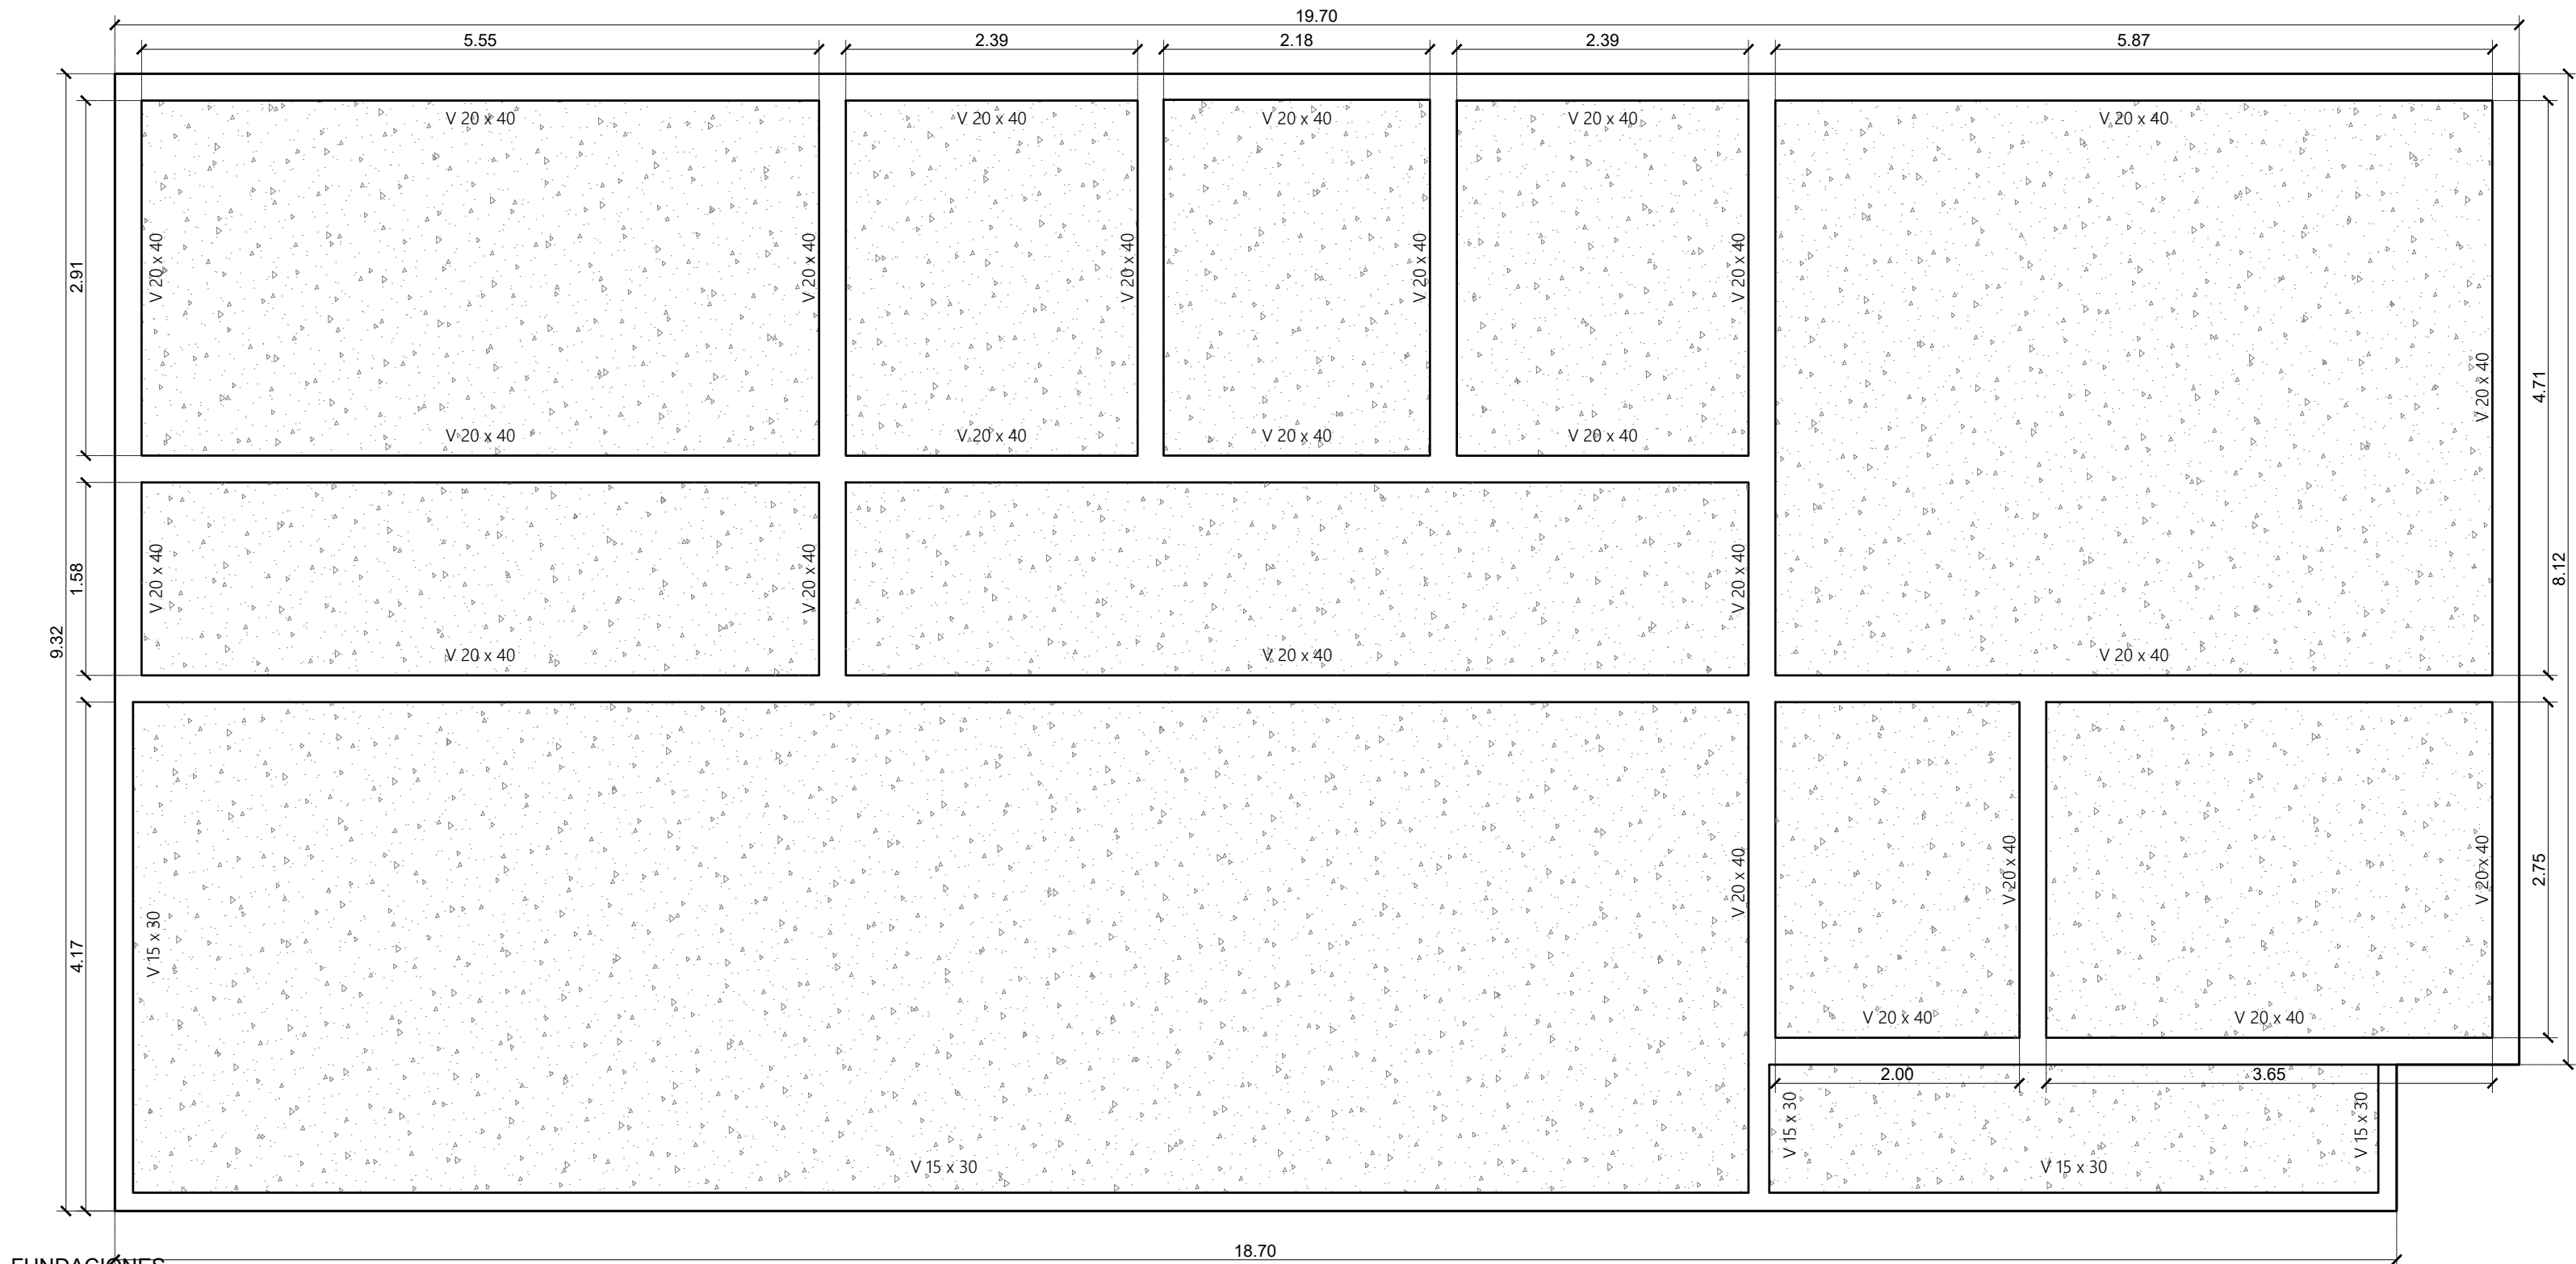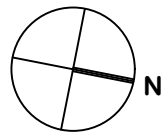

FUNDACIONES  
ESC 1:50

NOTAS

|   |                       |   |                                       |                               |                                                                                       |
|---|-----------------------|---|---------------------------------------|-------------------------------|---------------------------------------------------------------------------------------|
| NOTAS   |                       | LA PRESENTE DOCUMENTACIÓN ES INDICATIVA. EL CONTRATISTA EJECUTARÁ LA DOCUMENTACIÓN CONSTRUCTIVA DE LA OBRA, GENERAL Y DE DETALLE, LA CUAL DEBERÁ SER APROBADA POR LA DIRECCIÓN GENERAL DE ÁREAS DE CONSERVACIÓN Y RESTAURACIÓN AMBIENTAL. TODAS LAS MEDIDAS Y NIVELES SERÁN VERIFICADAS EN OBRA. |                                       |                               |                                                                                       |
| GOBIERNO DE LA CIUDAD DE BUENOS AIRES<br>SUBSECRETARIA DE AMBIENTE<br>DIRECCION GENERAL DE AREAS DE CONSERVACION Y RESTAURACION AMBIENTAL |                       |   | GERENCIA OPERATIVA DE INFRAESTRUCTURA |                               |  |
| OBRA<br>RESERVA ECOLÓGICA COSTANERA SUR                                                                                                   |                       |   | DIBUJO                                |                               |                                                                                       |
| PLANO<br>FUNDACIONES   |                       |   | REVISO                                |                               |                                                                                       |
|   |                       |   | APROBO                                |                               |                                                                                       |
| ARCHIVO   | RECS - BAÑOS VIAMONTE | EXPTE. Nº   | 25-21464165-GCABA-DGACRA              | 1F-2025-21464165-GCABA-DGACRA |                                                                                       |
| ESCALA   |                       | FECHA   | ENERO 2025                            | Nº PLANO                      | RECS_BV_FUN_5.0                                                                       |

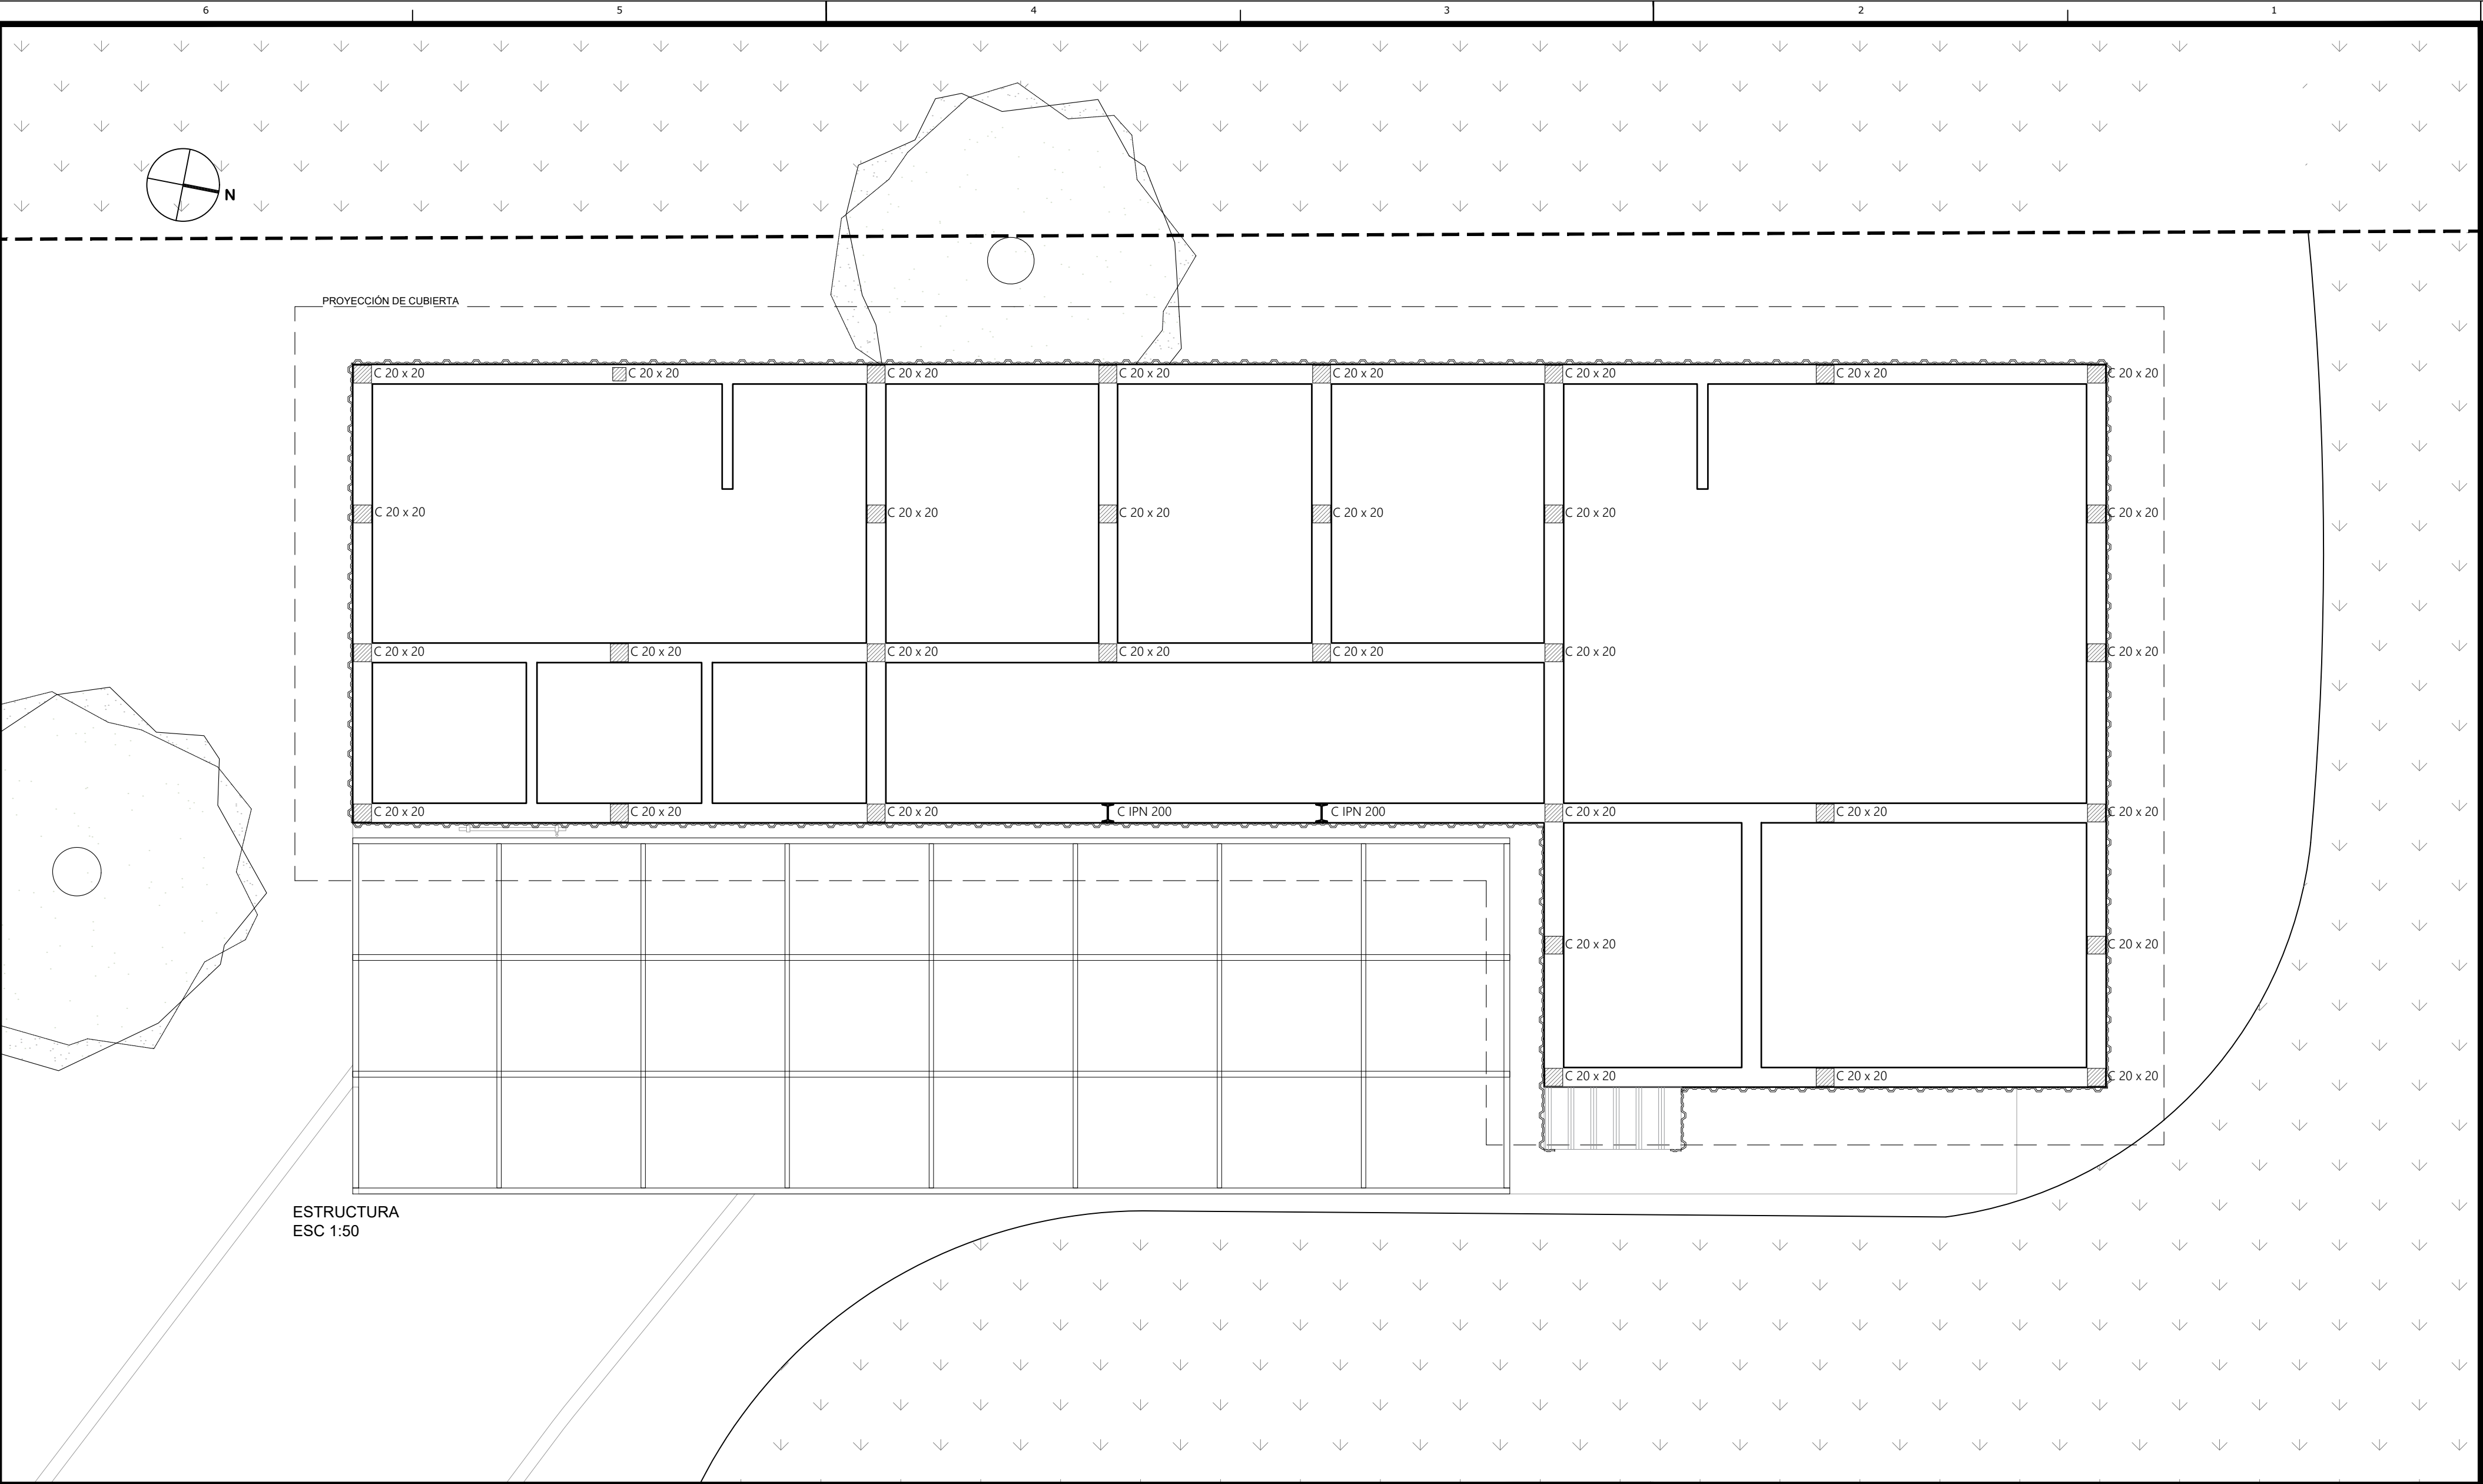

NOTAS

|   |                       |   |                               |                                              |                 |                                                                                       |  |
|---|-----------------------|---|-------------------------------|----------------------------------------------|-----------------|---------------------------------------------------------------------------------------|--|
| NOTAS   |                       | LA PRESENTE DOCUMENTACIÓN ES INDICATIVA. EL CONTRATISTA EJECUTARÁ LA DOCUMENTACIÓN CONSTRUCTIVA DE LA OBRA, GENERAL Y DE DETALLE, LA CUAL DEBERÁ SER APROBADA POR LA DIRECCIÓN GENERAL DE ÁREAS DE CONSERVACIÓN Y RESTAURACIÓN AMBIENTAL. TODAS LAS MEDIDAS Y NIVELES SERÁN VERIFICADAS EN OBRA. |                               |                                              |                 |                                                                                       |  |
| <b>GOBIERNO DE LA CIUDAD DE BUENOS AIRES</b><br>SUBSECRETARÍA DE AMBIENTE<br>DIRECCION GENERAL DE AREAS DE CONSERVACION Y RESTAURACION AMBIENTAL |                       |   |                               | <b>GERENCIA OPERATIVA DE INFRAESTRUCTURA</b> |                 |  |  |
| OBRA   |                       | RESERVA ECOLÓGICA COSTANERA SUR   |                               | DIBUJO                                       |                 |                                                                                       |  |
| PLANO   |                       | ESTRUCTURA   |                               | REVISO                                       |                 |                                                                                       |  |
|   |                       |   |                               | APROBO                                       |                 |                                                                                       |  |
| ARCHIVO   | RECS - BAÑOS VIAMONTE | EXPTE. Nº   | 1F-2025-21464165-GCABA-DGACRA |                                              |                 |                                                                                       |  |
| ESCALA   |                       | FECHA   | ENERO 2025                    | Nº PLANO                                     | RECS_BV_EST_5.1 |                                                                                       |  |

PLANILLA DE CARPINTERIAS

ABERTURAS PLANTA BAJA

| |
|---|
| P1   | UBICACION: ANTEBAÑO                           | CANTIDAD  | 2         | P2        | UBICACION: BAÑO PERSONAS C/ DISCAPACIDAD | CANTIDAD  | 1     | P3   | UBICACION: ACCESO BAÑO FAMILIAR, ACCESO ANTEBAÑO | CANTIDAD | 3               | P4        | UBICACION: DEPÓSITO, SALA DE MÁQUINAS | CANTIDAD   | 2         | P5        | UBICACION: NICHOS CALENTADOR AGUA Y TÓTEM DE CARGA | CANTIDAD | 1     | P6    | UBICACION: SALA DE MÁQUINAS | CANTIDAD | 1     | |
|   |                                               | ANCHO     | 1.00      |           |                                          | ANCHO     | 1.00  |      |                                                  | ANCHO    | 1.20            |           |                                       | ANCHO   | 1.00      |           |                                                    | ANCHO    | 1.30  |       |                             | ANCHO    | 1.60  | |
| |
| <table><tr><td>DESTINO</td><td>SS</td><td>PB</td><td>1°P</td><td>2°P</td><td>3°P</td><td>4°P</td></tr><tr><td>MANO</td><td>IZQ. DER.</td><td>IZQ. DER.</td><td>IZQ. DER.</td><td>IZQ. DER.</td><td>IZQ. DER.</td><td>IZQ. DER.</td></tr><tr><td>CANTIDAD</td><td>-</td><td>-</td><td>1</td><td>1</td><td>-</td><td>-</td></tr></table> |                                               |           |           | DESTINO   | SS                                       | PB        | 1°P   | 2°P  | 3°P                                              | 4°P      | MANO            | IZQ. DER. | IZQ. DER.                             | IZQ. DER.   | IZQ. DER. | IZQ. DER. | IZQ. DER.                                          | CANTIDAD | -     | -     | 1                           | 1        | -     | -        | <table><tr><td>DESTINO</td><td>SS</td><td>PB</td><td>1°P</td><td>2°P</td><td>3°P</td><td>4°P</td></tr><tr><td>MANO</td><td>IZQ. DER.</td><td>IZQ. DER.</td><td>IZQ. DER.</td><td>IZQ. DER.</td><td>IZQ. DER.</td><td>IZQ. DER.</td></tr><tr><td>CANTIDAD</td><td>-</td><td>-</td><td>-</td><td>1</td><td>-</td><td>-</td></tr></table> |          |           |   | DESTINO | SS | PB | 1°P   | 2°P   | 3°P   | 4°P   | MANO | IZQ. DER.         | IZQ. DER. | IZQ. DER.       | IZQ. DER. | IZQ. DER. | IZQ. DER.   | CANTIDAD | - | - | -     | 1     | -     | -     | <table><tr><td>DESTINO</td><td>SS</td><td>PB</td><td>1°P</td><td>2°P</td><td>3°P</td><td>4°P</td></tr><tr><td>MANO</td><td>IZQ. DER.</td><td>IZQ. DER.</td><td>IZQ. DER.</td><td>IZQ. DER.</td><td>IZQ. DER.</td><td>IZQ. DER.</td></tr><tr><td>CANTIDAD</td><td>-</td><td>-</td><td>2</td><td>1</td><td>-</td><td>-</td></tr></table> |       |          |                 | DESTINO  | SS       | PB   | 1°P | 2°P | 3°P | 4°P   | MANO  | IZQ. DER. | IZQ. DER. | IZQ. DER. | IZQ. DER.         | IZQ. DER. | IZQ. DER.       | CANTIDAD | -             | -   | 2 | 1 | - | -     | <table><tr><td>DESTINO</td><td>SS</td><td>PB</td><td>1°P</td><td>2°P</td><td>3°P</td><td>4°P</td></tr><tr><td>MANO</td><td>IZQ. DER.</td><td>IZQ. DER.</td><td>IZQ. DER.</td><td>IZQ. DER.</td><td>IZQ. DER.</td><td>IZQ. DER.</td></tr><tr><td>CANTIDAD</td><td>-</td><td>-</td><td>-</td><td>2</td><td>-</td><td>-</td></tr></table> |       |       |      | DESTINO | SS       | PB              | 1°P      | 2°P            | 3°P | 4°P | MANO | IZQ. DER. | IZQ. DER. | IZQ. DER. | IZQ. DER. | IZQ. DER. | IZQ. DER. | CANTIDAD | - | - | - | 2 | - | - | <table><tr><td>DESTINO</td><td>SS</td><td>PB</td><td>1°P</td><td>2°P</td><td>3°P</td><td>4°P</td></tr><tr><td>MANO</td><td>IZQ. DER.</td><td>IZQ. DER.</td><td>IZQ. DER.</td><td>IZQ. DER.</td><td>IZQ. DER.</td><td>IZQ. DER.</td></tr><tr><td>CANTIDAD</td><td>-</td><td>-</td><td>-</td><td>-</td><td>-</td><td>-</td></tr></table> |  |  |  | DESTINO | SS | PB | 1°P | 2°P | 3°P | 4°P | MANO | IZQ. DER. | IZQ. DER. | IZQ. DER. | IZQ. DER. | IZQ. DER. | IZQ. DER. | CANTIDAD | - | - | - | - | - | - | <table><tr><td>DESTINO</td><td>SS</td><td>PB</td><td>1°P</td><td>2°P</td><td>3°P</td><td>4°P</td></tr><tr><td>MANO</td><td>IZQ. DER.</td><td>IZQ. DER.</td><td>IZQ. DER.</td><td>IZQ. DER.</td><td>IZQ. DER.</td><td>IZQ. DER.</td></tr><tr><td>CANTIDAD</td><td>-</td><td>-</td><td>-</td><td>-</td><td>-</td><td>-</td></tr></table> |  |  |  | DESTINO | SS | PB | 1°P | 2°P | 3°P | 4°P | MANO | IZQ. DER. | IZQ. DER. | IZQ. DER. | IZQ. DER. | IZQ. DER. | IZQ. DER. | CANTIDAD | - | - | - | - | - | - |
| DESTINO   | SS                                            | PB        | 1°P       | 2°P       | 3°P                                      | 4°P       | |
| MANO   | IZQ. DER.                                     | IZQ. DER. | IZQ. DER. | IZQ. DER. | IZQ. DER.                                | IZQ. DER. | |
| CANTIDAD   | -                                             | -         | 1         | 1         | -                                        | -         | |
| DESTINO   | SS                                            | PB        | 1°P       | 2°P       | 3°P                                      | 4°P       | |
| MANO   | IZQ. DER.                                     | IZQ. DER. | IZQ. DER. | IZQ. DER. | IZQ. DER.                                | IZQ. DER. | |
| CANTIDAD   | -                                             | -         | -         | 1         | -                                        | -         | |
| DESTINO   | SS                                            | PB        | 1°P       | 2°P       | 3°P                                      | 4°P       | |
| MANO   | IZQ. DER.                                     | IZQ. DER. | IZQ. DER. | IZQ. DER. | IZQ. DER.                                | IZQ. DER. | |
| CANTIDAD   | -                                             | -         | 2         | 1         | -                                        | -         | |
| DESTINO   | SS                                            | PB        | 1°P       | 2°P       | 3°P                                      | 4°P       | |
| MANO   | IZQ. DER.                                     | IZQ. DER. | IZQ. DER. | IZQ. DER. | IZQ. DER.                                | IZQ. DER. | |
| CANTIDAD   | -                                             | -         | -         | 2         | -                                        | -         | |
| DESTINO   | SS                                            | PB        | 1°P       | 2°P       | 3°P                                      | 4°P       | |
| MANO   | IZQ. DER.                                     | IZQ. DER. | IZQ. DER. | IZQ. DER. | IZQ. DER.                                | IZQ. DER. | |
| CANTIDAD   | -                                             | -         | -         | -         | -                                        | -         | |
| DESTINO   | SS                                            | PB        | 1°P       | 2°P       | 3°P                                      | 4°P       | |
| MANO   | IZQ. DER.                                     | IZQ. DER. | IZQ. DER. | IZQ. DER. | IZQ. DER.                                | IZQ. DER. | |
| CANTIDAD   | -                                             | -         | -         | -         | -                                        | -         | |
| <table><tr><td>COLOR</td><td>NEGRO</td></tr><tr><td>MARCO</td><td>CHAPA</td></tr><tr><td>HOJA</td><td>CHAPA</td></tr><tr><td>HERRAJES</td><td>DOBLE CERRADURA</td></tr><tr><td>APERTURA</td><td>DE ABRIR</td></tr></table>   |                                               |           |           | COLOR     | NEGRO                                    | MARCO     | CHAPA | HOJA | CHAPA                                            | HERRAJES | DOBLE CERRADURA | APERTURA  | DE ABRIR                              | <table><tr><td>COLOR</td><td>NEGRO</td></tr><tr><td>MARCO</td><td>CHAPA</td></tr><tr><td>HOJA</td><td>CHAPA</td></tr><tr><td>HERRAJES</td><td>DOBLE CERRADURA, RIEL, RODAMIENTOS, PASAMANOS</td></tr><tr><td>APERTURA</td><td>CORREDIZA</td></tr></table> |           |           |                                                    | COLOR    | NEGRO | MARCO | CHAPA                       | HOJA     | CHAPA | HERRAJES | DOBLE CERRADURA, RIEL, RODAMIENTOS, PASAMANOS   | APERTURA | CORREDIZA | <table><tr><td>COLOR</td><td>NEGRO</td></tr><tr><td>MARCO</td><td>CHAPA</td></tr><tr><td>HOJA</td><td>CHAPA TRAPEZOIDAL</td></tr><tr><td>HERRAJES</td><td>DOBLE CERRADURA</td></tr><tr><td>APERTURA</td><td>CORREDIZA</td></tr></table> |         |    |    | COLOR | NEGRO | MARCO | CHAPA | HOJA | CHAPA TRAPEZOIDAL | HERRAJES  | DOBLE CERRADURA | APERTURA  | CORREDIZA | <table><tr><td>COLOR</td><td>NEGRO</td></tr><tr><td>MARCO</td><td>CHAPA</td></tr><tr><td>HOJA</td><td>CHAPA</td></tr><tr><td>HERRAJES</td><td>DOBLE CERRADURA</td></tr><tr><td>APERTURA</td><td>DE ABRIR</td></tr></table> |          |   |   | COLOR | NEGRO | MARCO | CHAPA | HOJA   | CHAPA | HERRAJES | DOBLE CERRADURA | APERTURA | DE ABRIR | <table><tr><td>COLOR</td><td>NEGRO</td></tr><tr><td>MARCO</td><td>CHAPA</td></tr><tr><td>HOJA</td><td>CHAPA TRAPEZOIDAL</td></tr><tr><td>HERRAJES</td><td>DOBLE CERRADURA</td></tr><tr><td>APERTURA</td><td>DOBLE PLEGADO</td></tr></table> |     |     |     | COLOR | NEGRO | MARCO     | CHAPA     | HOJA      | CHAPA TRAPEZOIDAL | HERRAJES  | DOBLE CERRADURA | APERTURA | DOBLE PLEGADO | <table><tr><td>COLOR</td><td>NEGRO</td></tr><tr><td>MARCO</td><td>CHAPA</td></tr><tr><td>HOJA</td><td>CHAPA</td></tr><tr><td>HERRAJES</td><td>DOBLE CERRADURA</td></tr><tr><td>APERTURA</td><td>DOBLE DE ABRIR</td></tr></table> |   |   |   | COLOR | NEGRO   | MARCO | CHAPA | HOJA | CHAPA   | HERRAJES | DOBLE CERRADURA | APERTURA | DOBLE DE ABRIR | |
| COLOR   | NEGRO                                         | |
| MARCO   | CHAPA                                         | |
| HOJA   | CHAPA                                         | |
| HERRAJES   | DOBLE CERRADURA                               | |
| APERTURA   | DE ABRIR                                      | |
| COLOR   | NEGRO                                         | |
| MARCO   | CHAPA                                         | |
| HOJA   | CHAPA                                         | |
| HERRAJES   | DOBLE CERRADURA, RIEL, RODAMIENTOS, PASAMANOS | |
| APERTURA   | CORREDIZA                                     | |
| COLOR   | NEGRO                                         | |
| MARCO   | CHAPA                                         | |
| HOJA   | CHAPA TRAPEZOIDAL                             | |
| HERRAJES   | DOBLE CERRADURA                               | |
| APERTURA   | CORREDIZA                                     | |
| COLOR   | NEGRO                                         | |
| MARCO   | CHAPA                                         | |
| HOJA   | CHAPA                                         | |
| HERRAJES   | DOBLE CERRADURA                               | |
| APERTURA   | DE ABRIR                                      | |
| COLOR   | NEGRO                                         | |
| MARCO   | CHAPA                                         | |
| HOJA   | CHAPA TRAPEZOIDAL                             | |
| HERRAJES   | DOBLE CERRADURA                               | |
| APERTURA   | DOBLE PLEGADO                                 | |
| COLOR   | NEGRO                                         | |
| MARCO   | CHAPA                                         | |
| HOJA   | CHAPA                                         | |
| HERRAJES   | DOBLE CERRADURA                               | |
| APERTURA   | DOBLE DE ABRIR                                | |

NOTAS

LA PRESENTE DOCUMENTACIÓN ES INDICATIVA. EL CONTRATISTA EJECUTARÁ LA DOCUMENTACIÓN CONSTRUCTIVA DE LA OBRA, GENERAL Y DE DETALLE, LA CUAL DEBERÁ SER APROBADA POR LA DIRECCIÓN GENERAL DE ÁREAS DE CONSERVACIÓN Y RESTAURACIÓN AMBIENTAL. TODAS LAS MEDIDAS Y NIVELES SERÁN VERIFICADAS EN OBRA.

GOBIERNO DE LA CIUDAD DE BUENOS AIRES

SUBSECRETARÍA DE AMBIENTE

DIRECCIÓN GENERAL DE ÁREAS DE CONSERVACIÓN Y RESTAURACIÓN AMBIENTAL

GERENCIA OPERATIVA DE INFRAESTRUCTURA

OBRA

RESERVA ECOLÓGICA COSTANERA SUR

PLANO

PLANILLA DE CARPINTERÍAS

ARCHIVO

RECS - BAÑOS VIAMONTE

EXPTE. Nº

1F-2025-21464165-GCABA-DGACRA

ESCALA

FECHA


ENERO 2025

1F-2025-21464165-GCABA-DGACRA

Nº PLANO

RECS\_BV\_CAR\_6.0

PLANILLA DE HERRERÍA

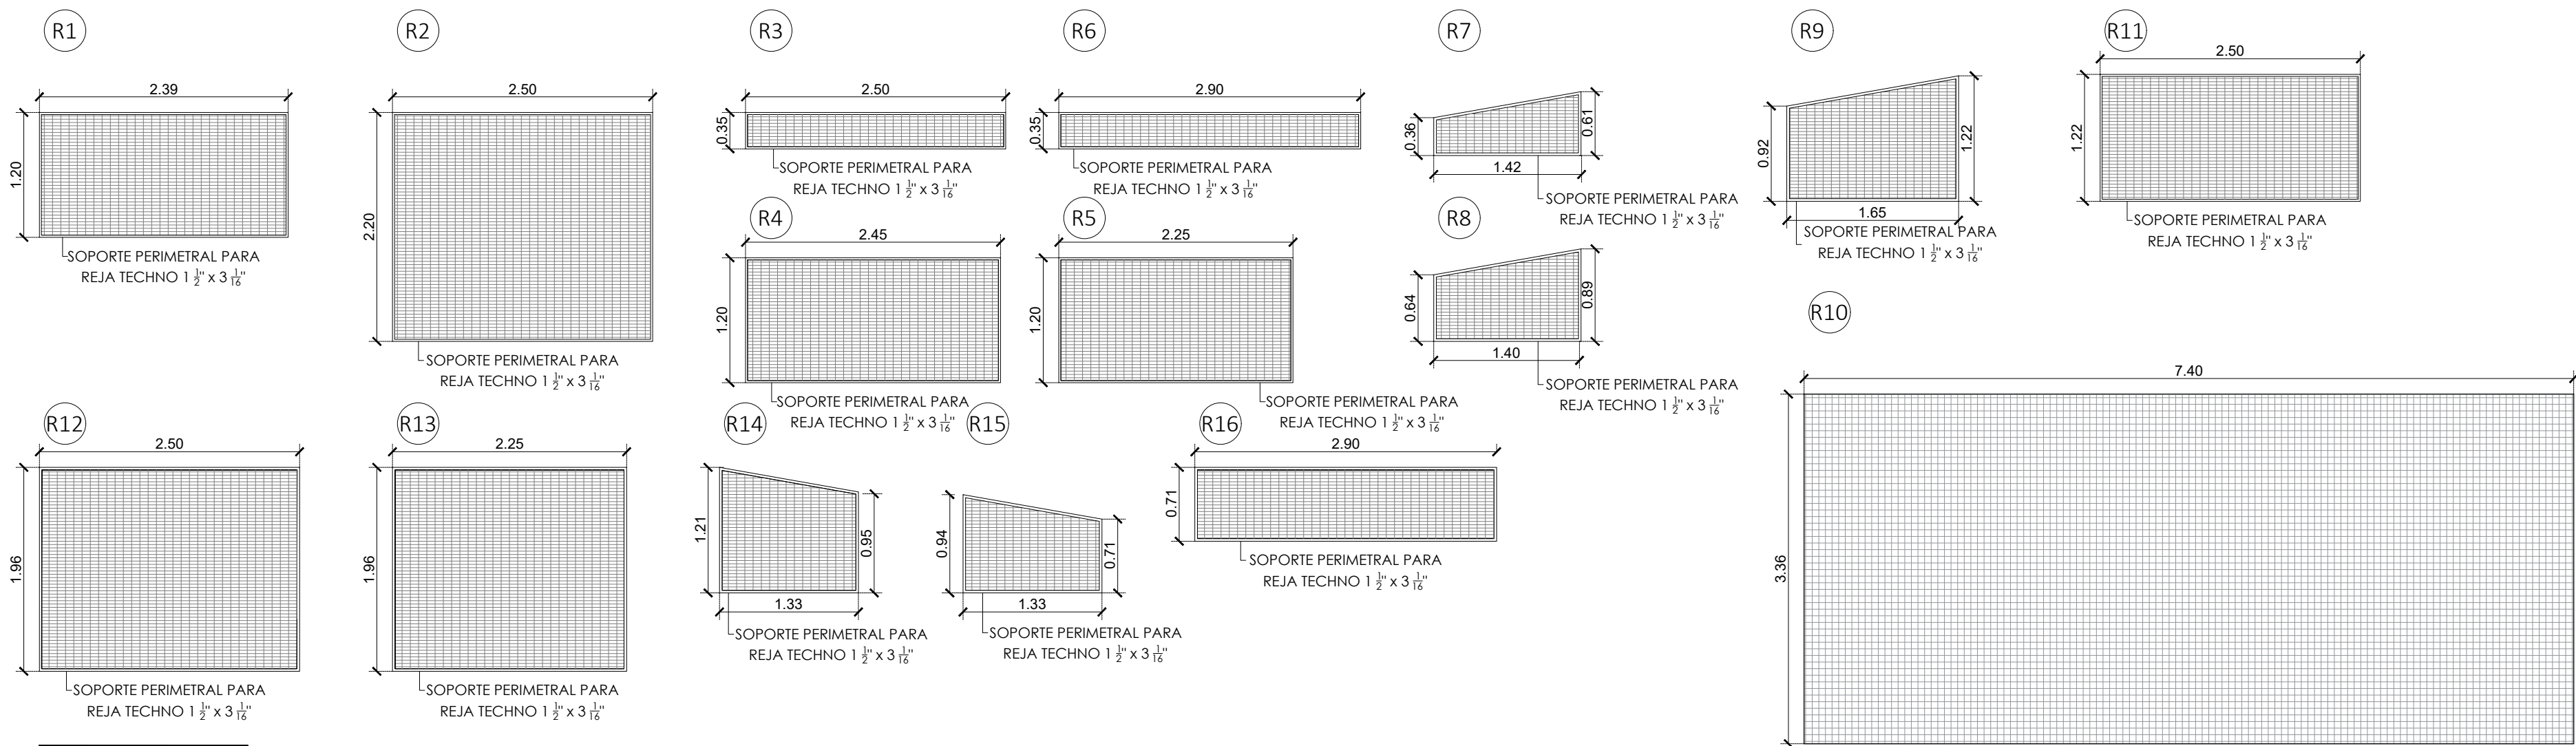

| REF | ÁREA     | RECuento |
|-----|----------|----------|
| R1  | 2.86 M²  | 2        |
| R2  | 5.50 M²  | 2        |
| R3  | 0.87 M²  | 2        |
| R4  | 2.94 M²  | 2        |
| R5  | 2.70 M²  | 1        |
| R6  | 1.00 M²  | 2        |
| R7  | 0.70 M²  | 2        |
| R8  | 1.00 M²  | 2        |
| R9  | 5.45 M²  | 2        |
| R10 | 24.85 M² | 1        |
| R11 | 3.00 M²  | 2        |
| R12 | 4.90 M²  | 2        |
| R13 | 4.40 M²  | 1        |
| R14 | 1.45 M²  | 2        |
| R15 | 1.10 M²  | 2        |
| R16 | 2.00 M²  | 2        |

NOTAS

LA PRESENTE DOCUMENTACIÓN ES INDICATIVA. EL CONTRATISTA EJECUTARÁ LA DOCUMENTATCIÓN CONSTRUCTIVA DE LA OBRA, GENERAL Y DE DETALLE, LA CUAL DEBERÁ SER APROBADA POR LA DIRECCIÓN GENERAL DE ÁREAS DE CONSERVACIÓN Y RESTAURACIÓN AMBIENTAL. TODAS LAS MEDIDAS Y NIVELES SERÁN VERIFICADAS EN OBRA.

GOBIERNO DE LA CIUDAD DE BUENOS AIRES

SUBSECRETARIA DE AMBIENTE

DIRECCION GENERAL DE AREAS DE CONSERVACION Y RESTAURACION AMBIENTAL

GERENCIA OPERATIVA DE INFRAESTRUCTURA

OBRA

RESERVA ECOLÓGICA COSTANERA SUR

DIBUJO

PLANO

PLANILLA DE CARPINTERÍAS

REVISO

ARCHIVO

RECS - BAÑOS VIAMONTE

EXpte. Nº

1F-2025-21464165-GCABA-DGACRA


Nº PLANO

RECS\_BV\_HER\_7.0

ESCALA

FECHA

ENERO 2025

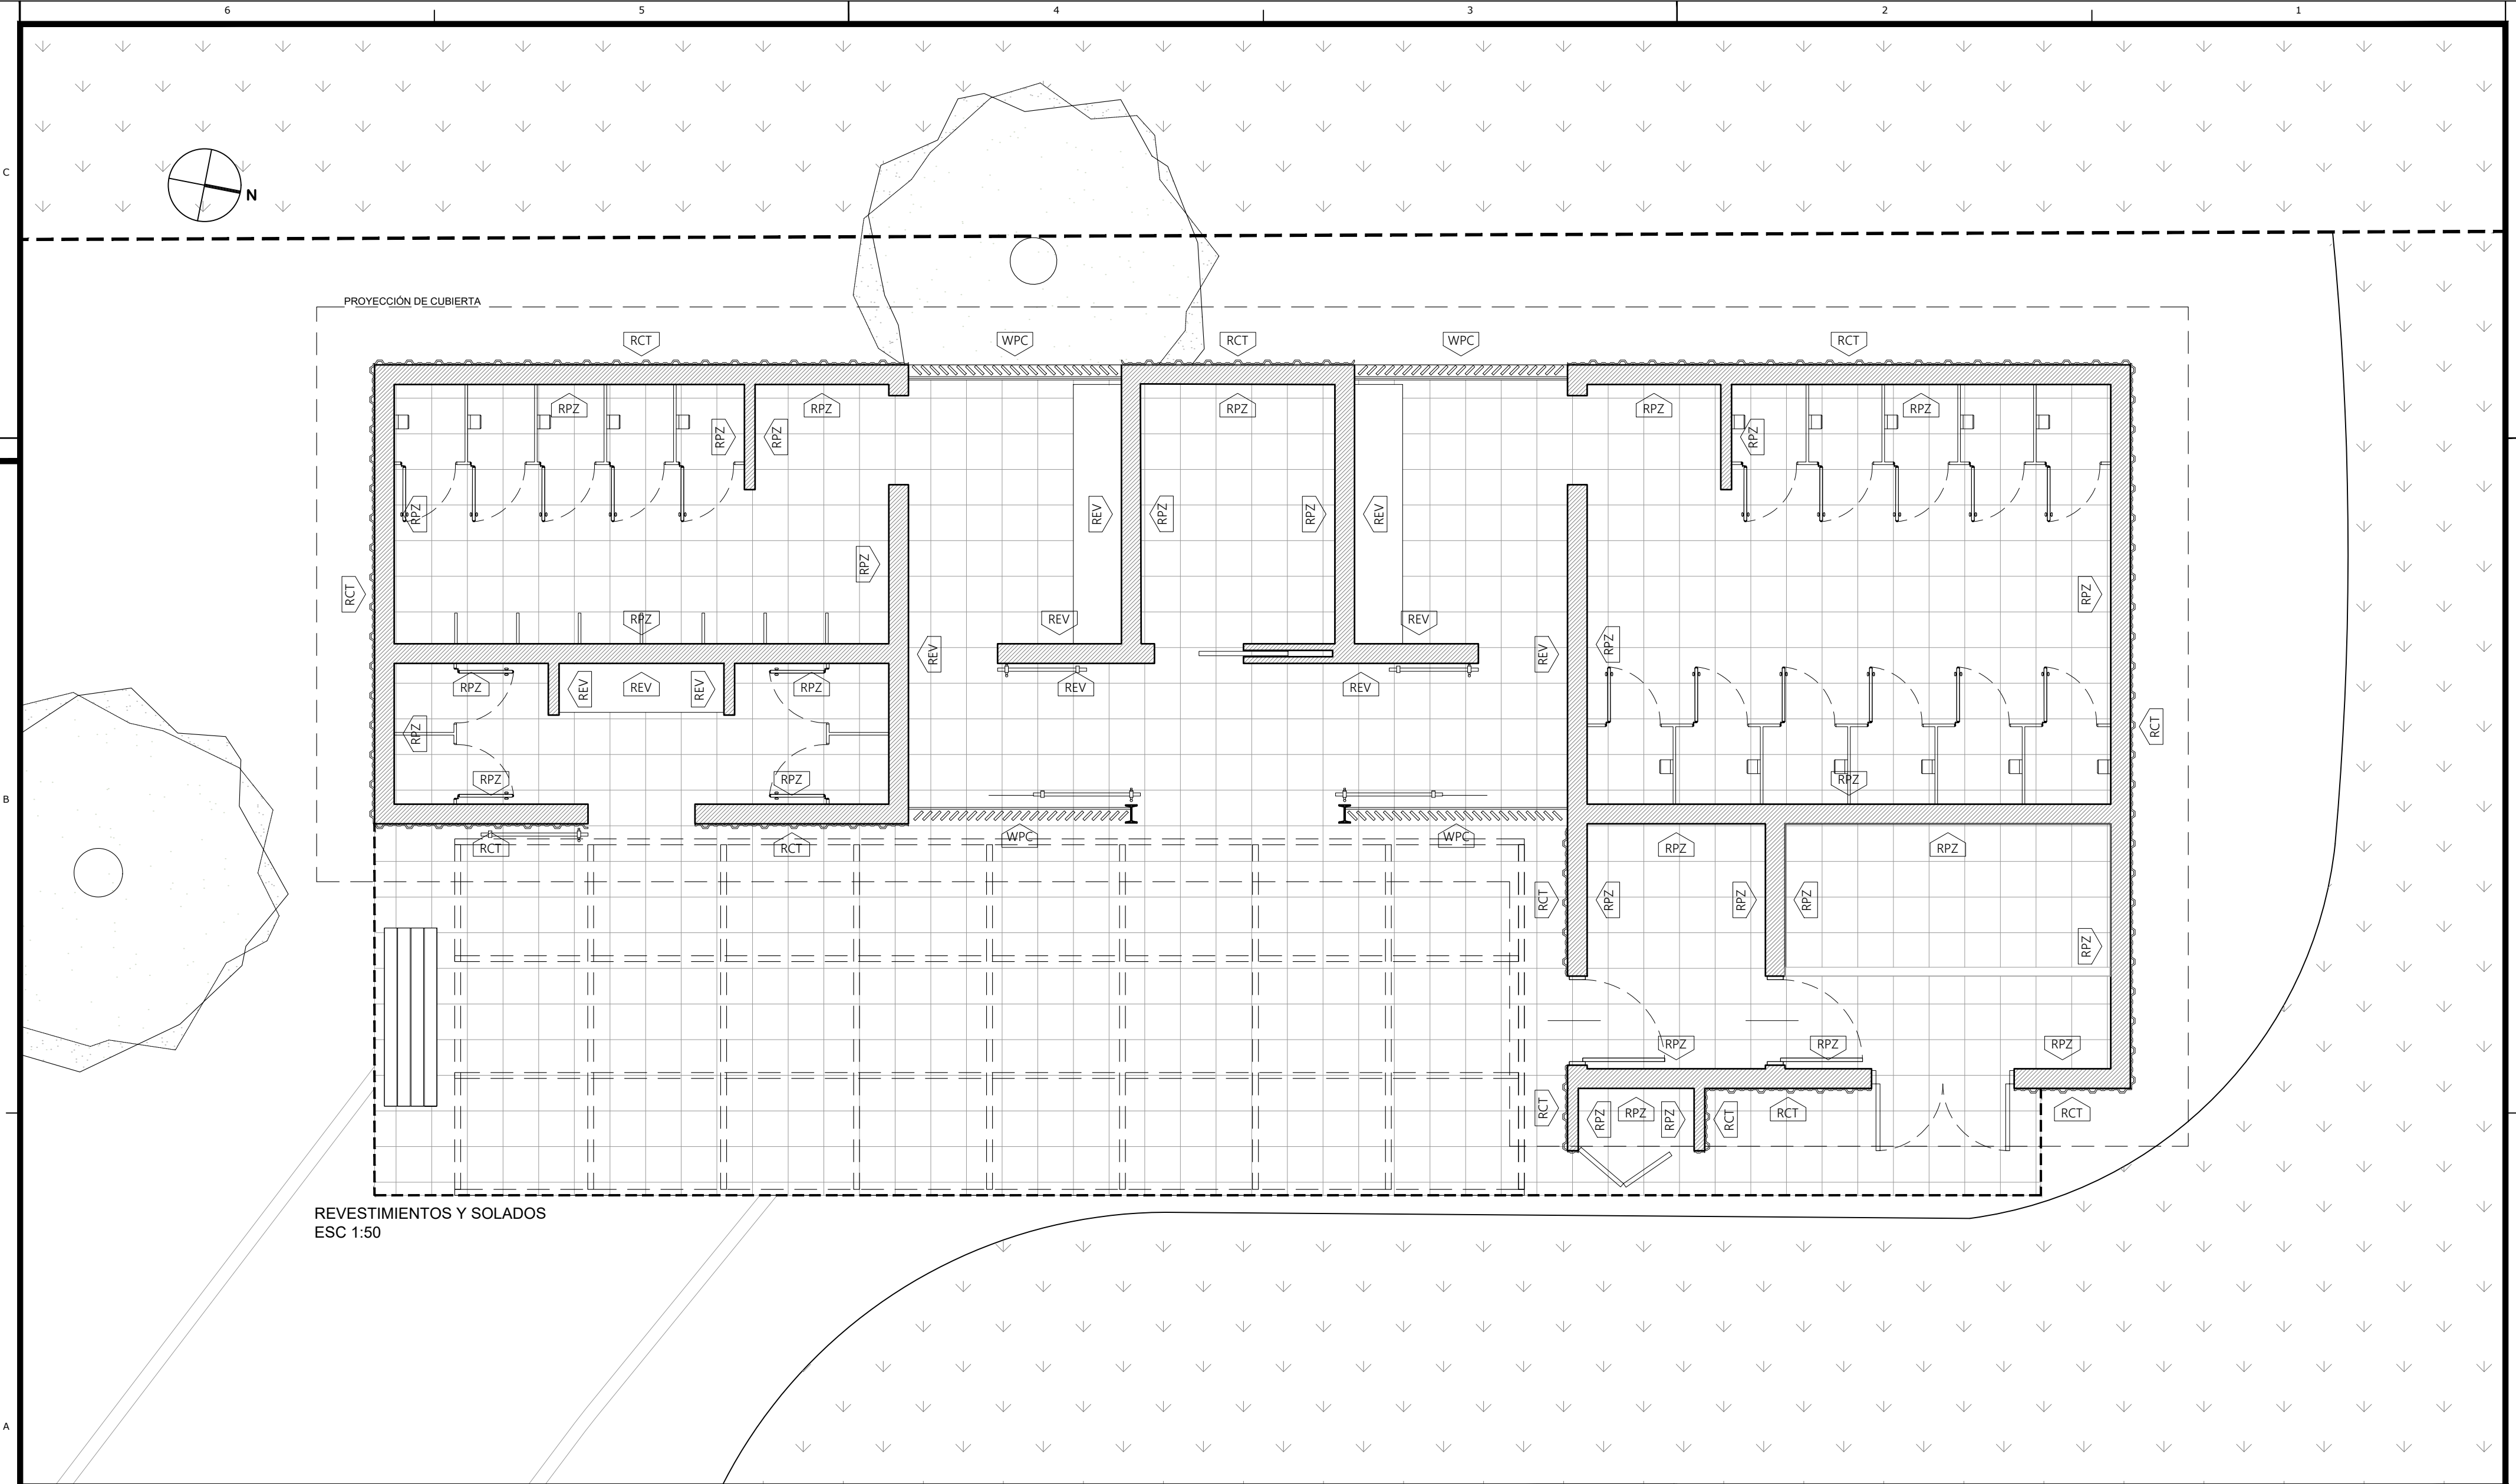

REVESTIMIENTOS Y SOLADOS  
ESC 1:50

REFERENCIAS

- 

Revestimiento Chapa Trapezoidal
- 

Revestimiento Pintura + Zócalo
- 


Revestimiento Estuco Veneciano
- 

Revestimiento Parasoles WPC
- 

Solado Granítico 40 x 40
- 


Perfil L

|   |  |  |  |   |  |                                                                                       |  |
|---|--|--|--|---|--|---------------------------------------------------------------------------------------|--|
| NOTAS   |  |  |  | LA PRESENTE DOCUMENTACIÓN ES INDICATIVA. EL CONTRATISTA EJECUTARÁ LA DOCUMENTACIÓN CONSTRUCTIVA DE LA OBRA, GENERAL Y DE DETALLE, LA CUAL DEBERÁ SER APROBADA POR LA DIRECCIÓN GENERAL DE ÁREAS DE CONSERVACIÓN Y RESTAURACIÓN AMBIENTAL. TODAS LAS MEDIDAS Y NIVELES SERÁN VERIFICADAS EN OBRA. |  |                                                                                       |  |
| <b>GOBIERNO DE LA CIUDAD DE BUENOS AIRES</b><br>SUBSECRETARIA DE AMBIENTE<br>DIRECCION GENERAL DE AREAS DE CONSERVACION Y RESTAURACION AMBIENTAL |  |  |  | <b>GERENCIA OPERATIVA DE INFRAESTRUCTURA</b>   |  |  |  |
| OBRA   |  |  |  | RESERVA ECOLÓGICA COSTANERA SUR   |  | DIBUJO                                                                                |  |
| PLANO   |  |  |  | <b>REVESTIMIENTOS Y SOLADOS</b>   |  | REVISO                                                                                |  |
| ARCHIVO   |  |  |  | RECS - BAÑOS VIAMONTE   |  | EXPT. Nº                                                                              |  |
| ESCALA   |  |  |  | FECHA   |  | ENERO 2025                                                                            |  |
|   |  |  |  |   |  | Nº PLANO                                                                              |  |
|   |  |  |  |   |  | RECS_BV_REVYSOL_8.0                                                                   |  |

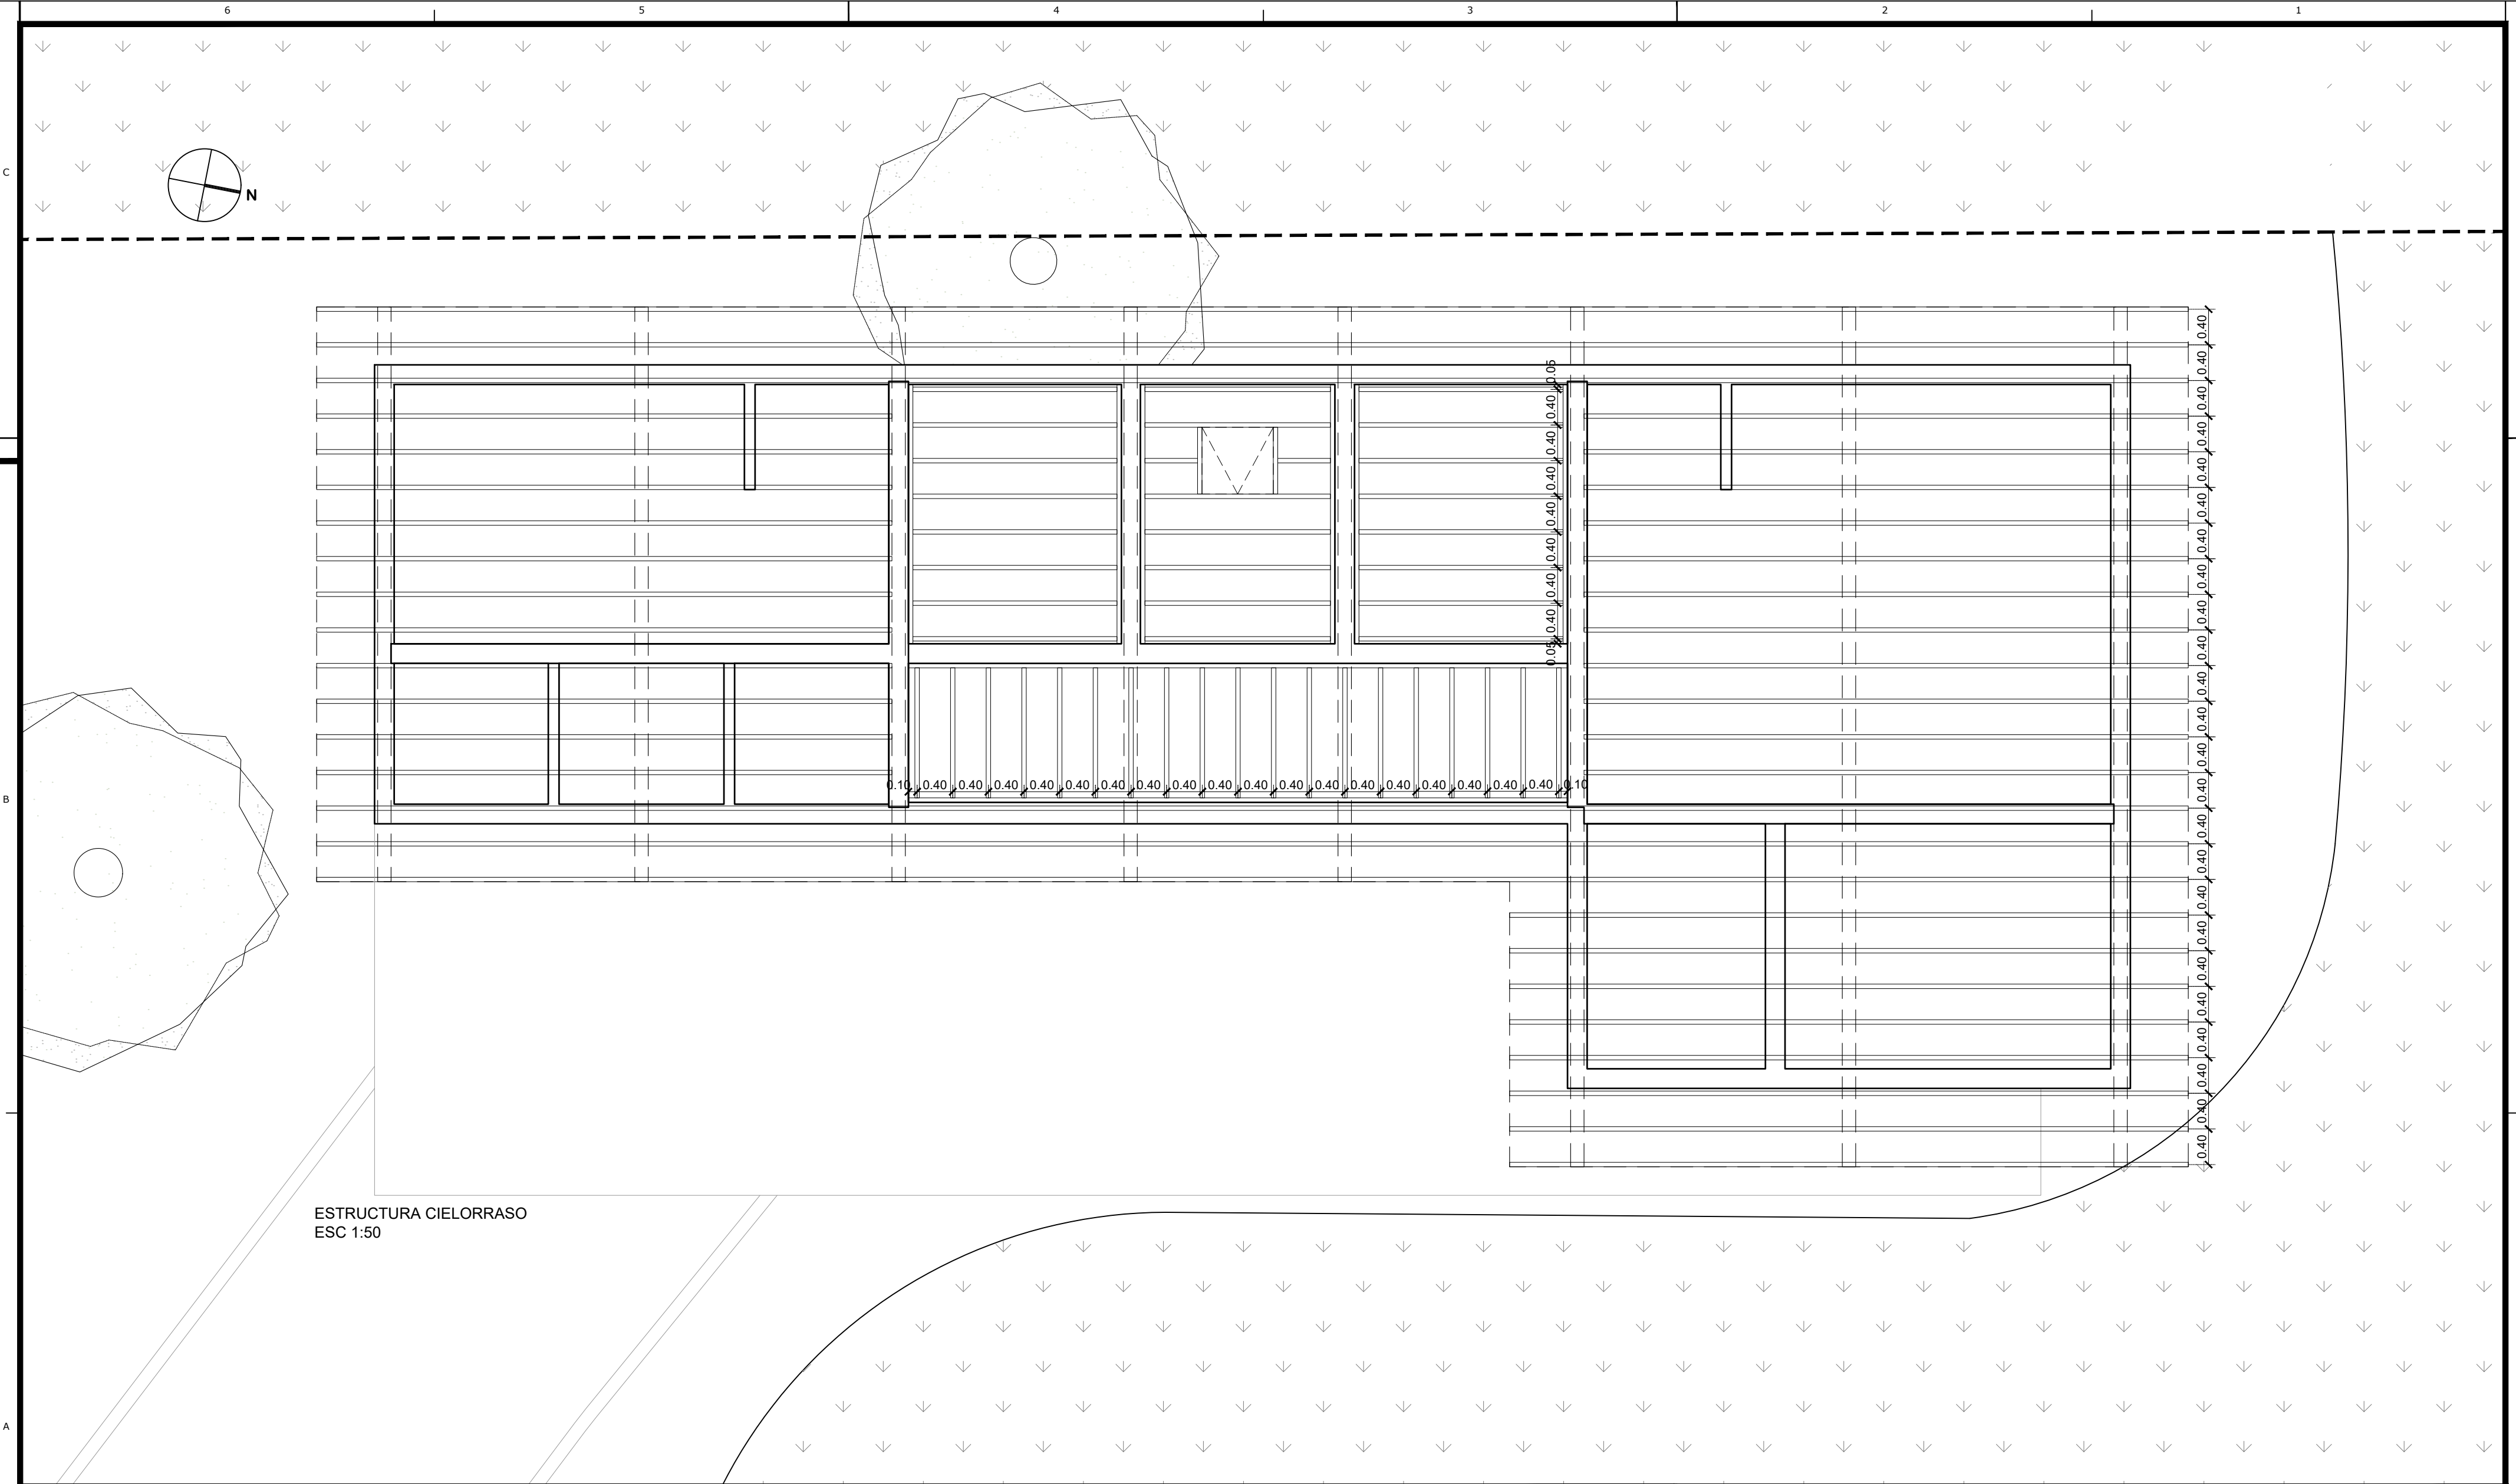

NOTAS  
Caño estructural 50x50x2 mm

|   |  |                                 |  |   |  |                                                                                       |  |
|---|--|---------------------------------|--|---|--|---------------------------------------------------------------------------------------|--|
| NOTAS   |  |                                 |  | LA PRESENTE DOCUMENTACIÓN ES INDICATIVA. EL CONTRATISTA EJECUTARÁ LA DOCUMENTACIÓN CONSTRUCTIVA DE LA OBRA, GENERAL Y DE DETALLE, LA CUAL DEBERÁ SER APROBADA POR LA DIRECCIÓN GENERAL DE ÁREAS DE CONSERVACIÓN Y RESTAURACIÓN AMBIENTAL. TODAS LAS MEDIDAS Y NIVELES SERÁN VERIFICADAS EN OBRA. |  |                                                                                       |  |
| GOBIERNO DE LA CIUDAD DE BUENOS AIRES<br>SUBSECRETARIA DE AMBIENTE<br>DIRECCION GENERAL DE AREAS DE CONSERVACION Y RESTAURACION AMBIENTAL |  |                                 |  | GERENCIA OPERATIVA DE INFRAESTRUCTURA   |  |  |  |
| OBRA   |  | RESERVA ECOLÓGICA COSTANERA SUR |  | DIBUJO   |  |                                                                                       |  |
| PLANO   |  | ESTRUCTURA CIELORRASO           |  | REVISO   |  |                                                                                       |  |
| ARCHIVO   |  | RECS - BAÑOS VIAMONTE           |  | EXpte. Nº   |  | 1F-2025-21464165-GCABA-DGACRA                                                         |  |
| ESCALA   |  |                                 |  | FECHA   |  | ENERO 2025                                                                            |  |
|   |  |                                 |  |   |  | Nº PLANO                                                                              |  |
|   |  |                                 |  |   |  | RECS_BV_CIEL_9.0                                                                      |  |

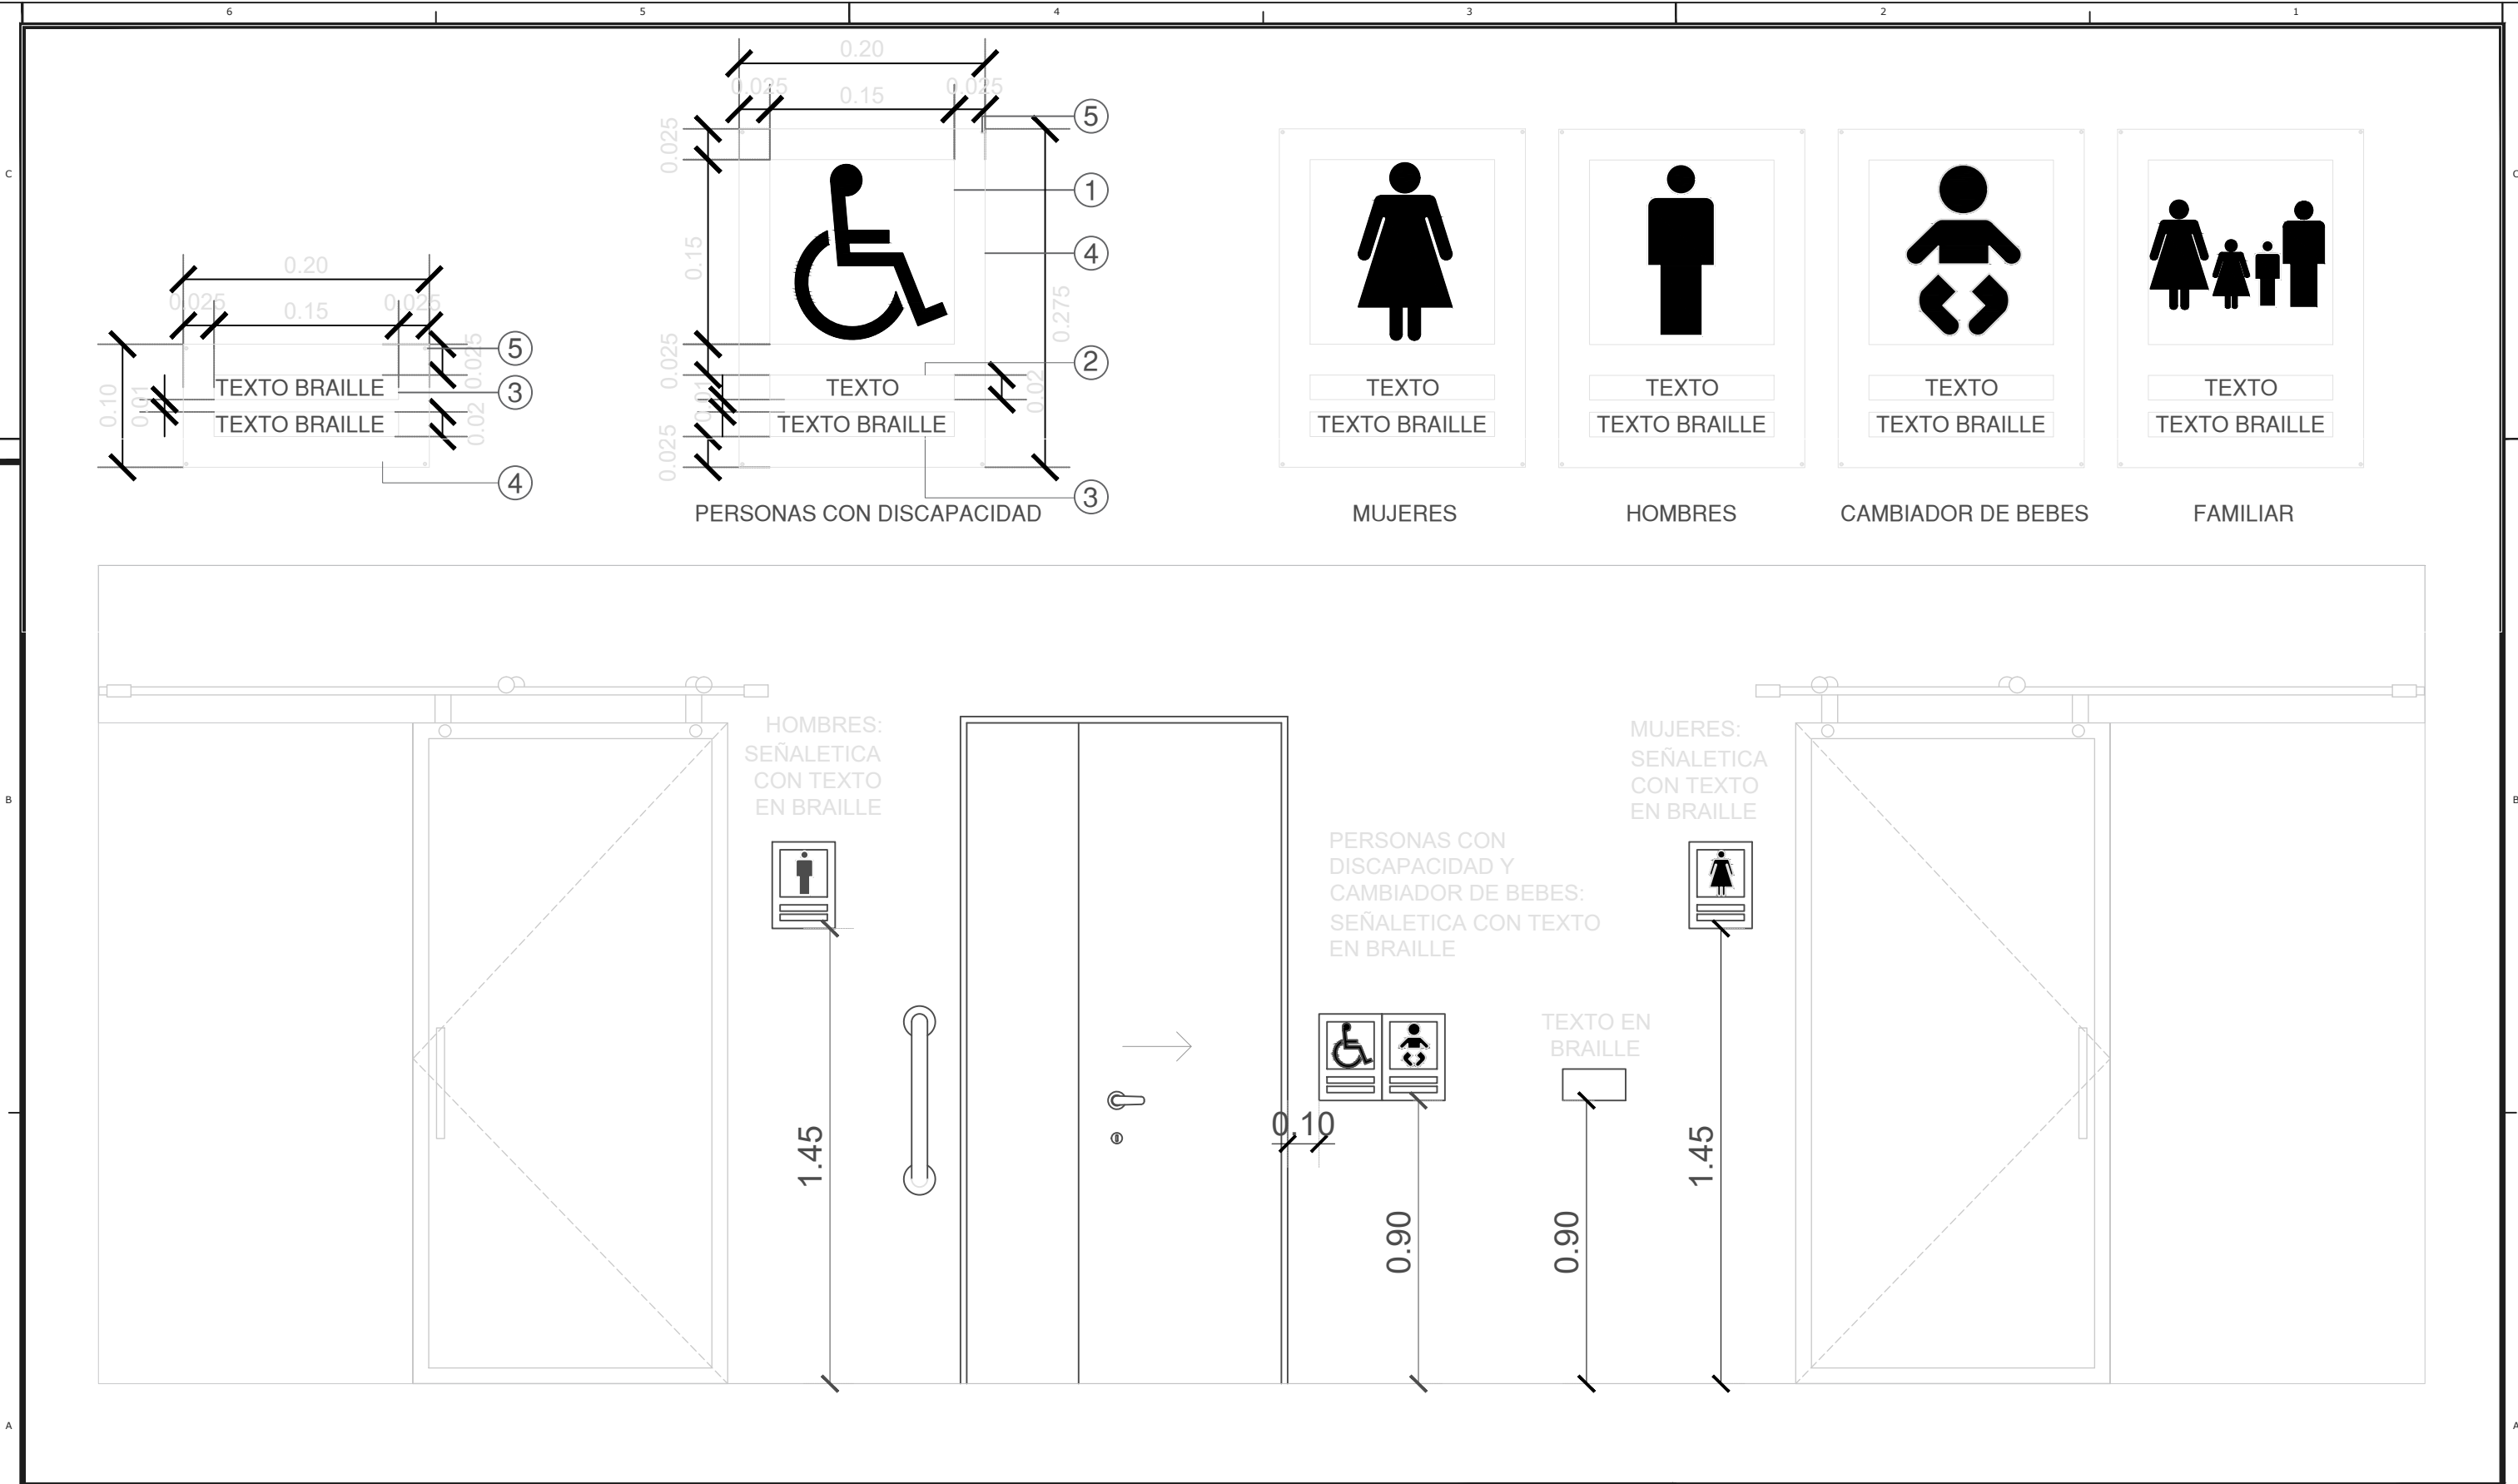

REFERENCIAS

- 1 - ÍCONO COLOR NEGRO CON FONDO DE COLOR BLANCO
- 2- TEXTO COLOR NEGRO CON ALINEACIÓN CENTRADA SOBRE ACRILICO CON FONDO BLANCO. TIPOGRAFIA: SANS SERIF
- 3- TEXTO EN BRAILLE SOBRE BANDA DE COLOR BLANCO CON PLASTIFICADO EN FRIO,AUTOADHESIVA. EL TEXTO DEBERA ESTAR ALINEADO A LA IZQUIERDA
- 4- ACRILICO TRANSPARENTE
- 5- FIJACIÓN CON TORNILLOS EN TODAS LAS ESQUINAS

|   |  |   |                                       |  |                                                                                       |
|---|--|---|---------------------------------------|--|---------------------------------------------------------------------------------------|
| NOTAS   |  | LA PRESENTE DOCUMENTACIÓN ES INDICATIVA. EL CONTRATISTA EJECUTARÁ LA DOCUMENTATCIÓN CONSTRUCTIVA DE LA OBRA, GENERAL Y DE DETALLE, LA CUAL DEBERÁ SER APROBADA POR LA DIRECCIÓN GENERAL DE ÁREAS DE CONSERVACIÓN Y RESTAURACIÓN AMBIENTAL. TODAS LAS MEDIDAS Y NIVELES SERÁN VERIFICADAS EN OBRA. |                                       |  |                                                                                       |
| GOBIERNO DE LA CIUDAD DE BUENOS AIRES<br>SUBSECRETARIA DE AMBIENTE<br>DIRECCION GENERAL DE AREAS DE CONSERVACION Y RESTAURACION AMBIENTAL |  |   | GERENCIA OPERATIVA DE INFRAESTRUCTURA |  |  |
| OBRA RESERVA ECOLÓGICA COSTANERA SUR   |  |   | ID-2025-21464165-CCABA-DGACRA         |  |                                                                                       |
| PLANO PLANO SEÑALÉTICA   |  |   | DIBUJO                                |  |                                                                                       |
| ARCHIVO   |  |   | REVISO                                |  |                                                                                       |
| ESCALA   |  |   | APROBO                                |  |                                                                                       |
| RECS - BAÑOS VIAMONTE   |  |   | Página 25 de 27                       |  | RECS_BV_SEÑA_10.0                                                                     |
| EXPTE. Nº   |  |   | Nº PLANO                              |  |                                                                                       |
| FECHA   |  |   | ENERO 2025                            |  |                                                                                       |

PLANILLA DE EQUIPAMIENTO


|        |   |                                                                                     |
|--------|---|-------------------------------------------------------------------------------------|
| 23.1.1 | GRIFERIA PARA PERSONAS CON DISCAPACIDAD<br>-Modelo: Canilla monocomando y mango de palanca a presion.<br>Linea espacio<br>-Ubicacion: Baño de personas con discapacidad<br>Cantidad: 1 unidad |    |
| 23.1.1 | BACHA PARA PERSONAS CON DISCAPACIDAD<br>-Modelo: Linea Espacio<br>-Ubicacion: Baño de personas con discapacidad<br>Cantidad: 1 unidad                                                         |    |
| 23.1.1 | INODORO PARA PERSONAS CON DISCAPACIDAD<br>-Modelo: Con deposito, Linea Espacio<br>-Ubicacion: Baño de personas con discapacidad<br>Cantidad: 1 unidad                                         |    |
| 23.1.1 | BARRAL REBATIBLE PARA PERSONAS CON DISCAPACIDAD<br>-Modelo: Rebatible de 80 cm<br>-Ubicacion: Baño personas con discapacidad (al lado del inodoro)<br>Cantidad: 1 unidad                      |    |
| 23.1.1 | BARRAL FIJO PARA PERSONAS CON DISCAPACIDAD<br>-Modelo: Fijo de 80 cm<br>-Ubicacion: Baño personas con discapacidad (al lado del inodoro)<br>Cantidad: 1 unidad                                |   |
| 23.1.1 | BARRAL FIJO PARA PERSONAS CON DISCAPACIDAD<br>-Modelo: Fijo de 60 cm<br>-Ubicacion: Baño personas con discapacidad (al lado de la bacha)<br>Cantidad: 2 unidades                              |  |
| 23.1.1 | BARRAL FIJO PARA PERSONAS CON DISCAPACIDAD<br>-Ubicacion: Baño personas con discapacidad (puerta de ingreso lado interior)<br>Cantidad: 1 unidad                                              |  |
| 23.1.1 | ESPEJO BASCULANTE PARA BAÑO DE PERSONAS CON DISCAPACIDAD<br>-Modelo: Linea espacio<br>-Ubicacion: Baño para personas con discapacidad (arriba de la bacha)<br>Cantidad: 1 unidad              |  |
| 23.1.2 | PULSADOR DE EMERGENCIA DISCAPACITADOS<br>-Ubicacion: Baño para personas con discapacidad<br>Cantidad: 1 unidad                                                                                |  |

|         |   |                                                                                       |
|---------|---|---------------------------------------------------------------------------------------|
| 23.1.3  | BRAZO DE CIERRE PARA PUERTA<br>-Modelo: hidraulico<br>-Ubicacion: Deposito y Sala de maquinas<br>Cantidad: 2 unidades                                                           |    |
| 23.1.4  | BACHA DE APOYO<br>-Modelo: Kira, linea Inspira<br>-Ubicacion: Baño familiar - Baño Hombres y Mujeres<br>Cantidad: 11 unidades                                                   |    |
| 23.1.5  | GRIFERIA DE PARED<br>-Modelo: Pressmatic temporizada antivandalica<br>-Ubicacion: Baño familiar - Baño Hombres y Mujeres<br>Cantidad: 11 unidades                               |    |
| 23.1.6  | DISPENSER DE JABON LIQUIDO<br>-Modelo: 900 ml<br>-Ubicacion: Baño familiar - Baño Hombres , Mujeres y personas con discapacidad<br>Cantidad: 4 unidades                         |    |
| 23.1.7  | DISPENSER DE TOALLAS INTERCALADAS<br>-Modelo: capacidad 500 toallas<br>-Ubicacion: Baño familiar - Baño Hombres , Mujeres y personas con discapacidad<br>Cantidad: 4 unidades   |   |
| 23.1.8  | DISPENSER DE PAPEL HIGIENICO<br>-Modelo: capacidad para rollos 400 m<br>-Ubicacion: Baño familiar - Baño Hombres , Mujeres y personas con discapacidad<br>Cantidad: 21 unidades |  |
| 23.1.9  | PERCHEROS DE PARED<br>-Modelo: Zinc cromado<br>-Ubicacion: Baño familiar - Baño Hombres , Mujeres y personas con discapacidad<br>Cantidad: 21 unidades                          |  |
| 23.1.10 | TACHO DE RESIDUO<br>-Modelo: Acero inoxidable de 14 lts<br>-Ubicacion: Baño familiar - Baño Hombres , Mujeres y personas con discapacidad<br>Cantidad: 21 unidades              |  |
| 23.1.11 | ESPEJO FLOAT<br>-Modelo: 6 mm de espesor<br>-Ubicacion: Baño familiar - Baño Hombres y Mujeres<br>Cantidad: 7 m2                                                                |  |

|         |   |                                                                                       |
|---------|---|---------------------------------------------------------------------------------------|
| 23.1.12 | INODORO CON TAPA NIÑOS<br>-Modelo: para niños<br>-Ubicacion: Baño familiar<br>Cantidad: 4 unidades                                                                       |    |
| 23.1.13 | CAMBIADOR DE BEBES RIGIDO<br>-Ubicacion: Baño de personas con discapacidad<br>Cantidad: 1 unidad                                                                         |    |
| 23.1.14 | INODORO CON TAPA ADULTOS<br>-Modelo: Bari corto<br>-Ubicacion: Baño Hombres y Mujeres<br>Cantidad: 16 unidades                                                           |    |
| 23.1.15 | MINGITORIO<br>-Modelo: Mural corto antivandalico<br>-Ubicacion: Baño Hombres<br>Cantidad: 8 unidades                                                                     |    |
| 23.1.16 | VALVULA PARA INODORO<br>-Modelo: Antivandalica<br>-Ubicacion: Baño familiar - Baño Hombres y Mujeres<br>Cantidad: 20 unidades                                            |   |
| 23.1.17 | VALVULA PARA MINGITORIO<br>-Modelo: 0362.01<br>-Ubicacion: Baño Hombres<br>Cantidad: 8 unidades                                                                          |  |
| 23.1.18 | DESAGUE PARA BACHAS<br>-Modelo: de acero inoxidable con sifon<br>-Ubicacion: Baño familiar - Baño Hombres , Mujeres y personas con discapacidad<br>Cantidad: 11 unidades |  |

|                                            |   |                                       |                                |
|--------------------------------------------|---|---------------------------------------|--------------------------------|
| NOTAS                                      | LA PRESENTE DOCUMENTACIÓN ES INDICATIVA. EL CONTRATISTA EJECUTARÁ LA DOCUMENTACIÓN CONSTRUCTIVA DE LA OBRA, GENERAL Y DE DETALLE, LA CUAL DEBERÁ SER APROBADA POR LA DIRECCIÓN GENERAL DE ÁREAS DE CONSERVACIÓN. TODAS LAS MEDIDAS Y NIVELES SERÁN VERIFICADAS EN OBRA. |                                       |                                |
| GOBIERNO DE LA CIUDAD DE BUENOS AIRES      |   | GERENCIA OPERATIVA DE INFRAESTRUCTURA |                                |
| SECRETARIA DE AMBIENTE                     |   |                                       |                                |
| DIRECCION GENERAL DE AREAS DE CONSERVACION |   |                                       |                                |
| OBRA                                       | RESERVA ECOLOGICA COSTANERA SUR   | DIBUJO                                |                                |
| PLANO                                      | PLANILLA DE EQUIPAMIENTO   | REVISO                                |                                |
| ARCHIVO                                    |   | APROBO                                |                                |
| ESCALA                                     |   | EXPT. N°                              | IE-2025-21464155-GCABA-DG-AGRA |
|                                            |   | FECHA                                 | 15/05/2025                     |

PLANILLA DE EQUIPAMIENTO
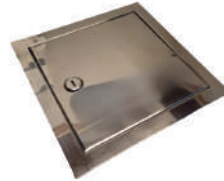
|         |   |                                                                                     |
|---------|---|-------------------------------------------------------------------------------------|
| 23.1.19 | BOMBA CENTRIFUGA<br>-Modelo: 0,75 HP<br>-Marca: tipo Vasser<br>-Ubicacion: Sala de maquinas<br>Cantidad: 4 unidades   |    |
| 23.1.20 | TANQUE DE AGUA<br>-Modelo: 1.500 litros<br><br>-Ubicacion: Sala de maquinas<br><br>Cantidad: 2 unidades   |    |
| 23.1.21 | TANQUE DE AGUA CHATO<br>-Modelo: chato de 1.000 litros<br>-Ubicacion: Arriba del baño de personas con discapacidad<br><br>Cantidad: 3 unidades   |    |
| 23.1.22 | CARTELERIA CON SISTEMA BRAILE<br>Baño familiar ,mujeres, hombres, personas con discapacidad y cambiador de bebes<br>-Modelo: acero inoxidable<br>-Ubicacion: Baño familiar - Baño Hombres , Mujeres y personas con discapacidad<br>Cantidad: 5 unidades |    |
| 23.1.23 | NICHO PARA CANILLA DE SERVICIO<br>-Modelo: de embutir de acero inoxidable<br>-Ubicacion: Baño familiar - Baño Hombres , Mujeres y exterior<br>Cantidad: 6 unidades                                                                                      |   |
| 23.1.24 | EXPENDEDORA DE AGUA CALIENTE<br><br>-Modelo: con conexion a 220v<br><br>Cantidad: 1 unidad   |  |
| 23.1.25 | TOTÉM DE CARGA PARA CELULARES<br><br><br>Cantidad: 1 unidades   |  |
| 23.1.26 | TOPE DE PISO PARA PUERTAS<br><br>-Ubicacion: Deposito y sala de maquinas<br><br>Cantidad: 2 unidades   |  |
| 23.1.27 | ARTEFACTO DE LUZ INTERIOR<br>-Modelo: aplique cilindrico de 4 watts orientable apto para aplicar sobre bandeja. Color: negro<br>-Ubicacion: Baño familiar - Baño Hombres , Mujeres, deposito y sala de maquinas<br>Cantidad: 18 unidades                |  |

|         |   |                                                                                       |
|---------|---|---------------------------------------------------------------------------------------|
| 23.1.28 | ARTEFACTO DE LUZ INTERIOR<br>-Modelo: plafon de 18 watts. aplique 22 cm.<br>Color: negro<br>-Ubicacion: Antebañó y baño de personas con discapacidad<br>Cantidad: 22 unidades |    |
| 23.1.29 | ARTEFACTO DE LUZ EXTERIOR<br>-Modelo: reflector negro de 4 watts<br><br>-Ubicacion: exterior en el ingreso<br><br>Cantidad: 1 unidad                                          |    |
| 23.1.30 | BANDEJA PORTACABLES PERFORADA 100mm X 3m 0.7mm<br><br><br>Cantidad: 22 M   |    |
| 23.1.31 | CARTELERÍA BAÑO CERRADO<br><br><br>Cantidad: 2 unidades   |    |
| 23.1.32 | TRABA LIBRE/OCUPADO<br><br><br>Cantidad: 20 unidades   |   |
| 23.1.33 | BANCO DE MADERA<br><br>-Modelo: igual a los existentes que se encuentran en la reserva<br><br>Cantidad: 4 unidades                                                            |  |
|         |   |                                                                                       |
|         |   |                                                                                       |
|         |   |                                                                                       |

|  |  |  |
|--|--|--|
|  |  |  |
|  |  |  |
|  |  |  |
|  |  |  |
|  |  |  |
|  |  |  |
|  |  |  |
|  |  |  |

|                                            |                                 |   |                                |
|--------------------------------------------|---------------------------------|---|--------------------------------|
| NOTAS                                      |                                 | LA PRESENTE DOCUMENTACIÓN ES INDICATIVA. EL CONTRATISTA EJECUTARÁ LA DOCUMENTACIÓN CONSTRUCTIVA DE LA OBRA, GENERAL Y DE DETALLE, LA CUAL DEBERÁ SER APROBADA POR LA DIRECCIÓN GENERAL DE ÁREAS DE CONSERVACIÓN. TODAS LAS MEDIDAS Y NIVELES SERÁN VERIFICADAS EN OBRA. |                                |
| GOBIERNO DE LA CIUDAD DE BUENOS AIRES      |                                 | GERENCIA OPERATIVA DE INFRAESTRUCTURA   |                                |
| SECRETARIA DE AMBIENTE                     |                                 |   |                                |
| DIRECCION GENERAL DE AREAS DE CONSERVACION |                                 |   |                                |
| OBRA                                       | RESERVA ECOLOGICA COSTANERA SUR | DIBUJO   |                                |
| PLANO                                      | PLANILLA DE EQUIPAMIENTO        | REVISO   |                                |
| ARCHIVO                                    |                                 | APROBO   |                                |
| ESCALA                                     |                                 | EXpte. Nº   | IE-2025-21464165-GCABA-DC-AQUA |
|                                            |                                 | FECHA   | 11.1                           |



G O B I E R N O D E L A C I U D A D D E B U E N O S A I R E S

**Hoja Adicional de Firmas**  
**Informe gráfico**

**Número:** IF-2025-21464165-GCABA-DGACRA

Buenos Aires, Viernes 23 de Mayo de 2025

**Referencia:** S/ PLANOS

---

El documento fue importado por el sistema GEDO con un total de 27 pagina/s.

Digitally signed by Comunicaciones Oficiales  
Date: 2025.05.23 13:12:52 -03:00

SUAREZ DE LA ROSA IGNACIO  
Director General  
D.G. AREAS DE CONSERVACION Y RESTAURACION AMBIENTAL  
AREA VICEJEFE DE GOBIERNO

Digitally signed by Comunicaciones Oficiales  
Date: 2025.05.23 13:12:53 -03:00